


AN ARCHED RETREAT — GUEST ROOM
ELEVATION STUDY · VISUALISATION

Alaa



DESIGN DEVELOPMENT
DIAGRAM

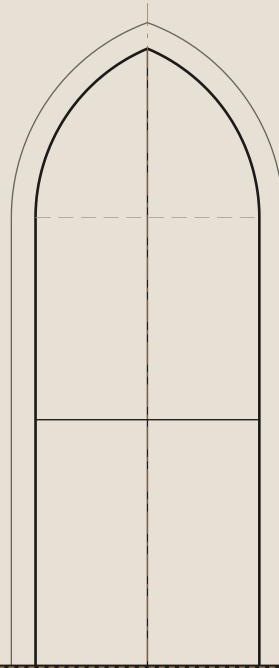

VISUALISATION
FIG. 07

Masri

Interior design and interior architecture — from the first concept to the final handover.

Design. Technical development. Execution.

PRACTICE

15+

years in interior design, interior architecture, fit-out and coordination

COUNTRIES

4

Saudi Arabia · Qatar · United Arab Emirates · Lebanon

SELECTED WORKS

7


residential, hospitality and architectural projects

STUDIES

25+

drawings and material studies prepared for this book


FOUR DISCIPLINES — DETAILS FROM THE SELECTED WORKS

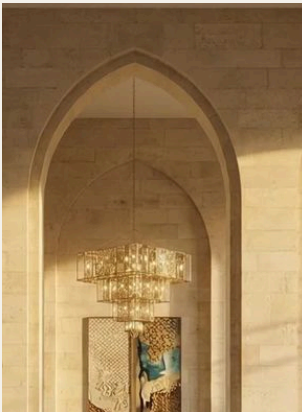


Architecture An arched retreat



Joinery The walnut suite

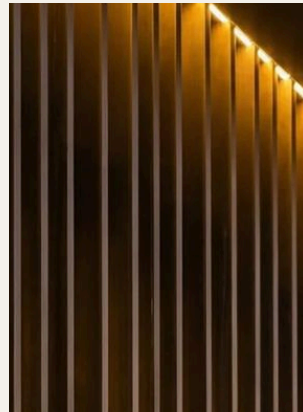

Facade The illuminated villa

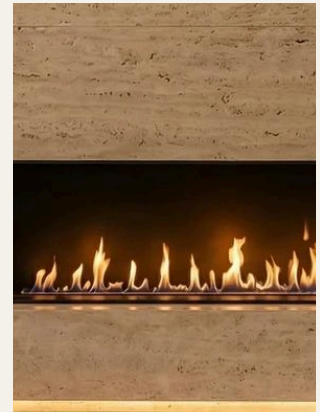

Material Living by the garden

BASED IN

Riyadh, Saudi Arabia

EMAIL

info@alaamasri.com

PHONE

+966 57 053 3358 · WhatsApp

ONLINE

alaamasri.com

Each project is shown through its visualisations and through studies drawn from them — the way it would be explained in a design review.

Contents

ALAA MASRI
INTERIOR DESIGNER
INTERIOR ARCHITECT

	Profile	04
	Expertise	06
	Selected works	08
01	An arched retreat	09
02	The skyline suite	15
03	The walnut suite	20
04	The illuminated villa	26
05	Living by the garden	30
06	The burgundy salon	34
07	An earthy welcome	36
	Technical capability	38
	Experience	40
	Contact	41

HOW TO READ THE DRAWINGS

The studies in this book were drawn for this portfolio to explain each design. They read the visualisations: they are not surveys, approved drawings or construction documents. Every drawing carries its status.

CODE	STATUS — WHAT IT CLAIMS
DD	Design development / space study — read from a named render
CD	Concept detail — how a visible junction could be built
RE	Representative example — generic, typical sizes
MS	Material study — swatches cropped from renders
—	“To survey”: size not known, never invented

PROFILE

Imagination.


With the knowledge to make it real.

Interior design and interior architecture — from the first concept to the final handover.

ALAA MASRI · RIYADH, SAUDI ARABIA




SELECTED WORK

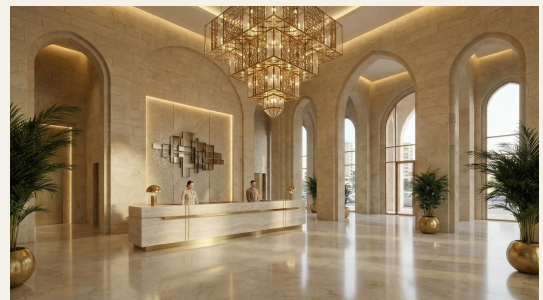

01 An arched retreat · p. 09



03 The walnut suite · p. 20

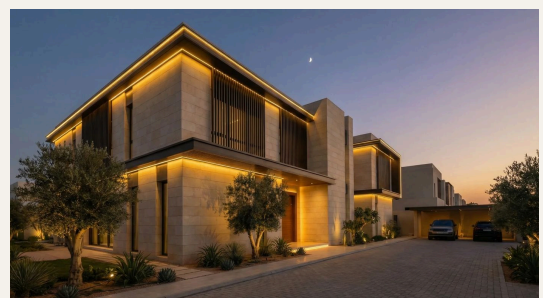

04 The illuminated villa · p. 26

I'm Alaa Masri, a Lebanese interior designer and interior architect based in Riyadh. Over 15 years of practice across the Gulf and Lebanon have shaped my approach to space.

I work from the first concept through to final handover, connecting design, materials and craftsmanship with the precision that execution demands.

My work spans luxury residential, hospitality, commercial and retail interiors — coordinating clients, consultants, contractors, workshops, factories and site teams so that the design holds from drawing to site.

15+

years in interior design, interior architecture, fit-out and project coordination.

PRACTICE ACROSS

Saudi Arabia
Qatar
United Arab Emirates
Lebanon

SECTORS

Residential · commercial ·
hospitality · retail

EDUCATION

BT — Interior Decoration /
Interior Design, Lebanon ·
TS studies, Interior Design

LANGUAGES

Arabic — native
English — professional
working proficiency


DESIGN TOOLKIT

AutoCAD · 3ds Max · V-Ray · Chaos Vantage · Blender ·
Photoshop · Illustrator

BEYOND THE DRAWING BOARD

AI-assisted design & visualization · Figma · Design
presentation

CONCEPT TO HANDOVER — HOW A PROJECT IS CARRIED

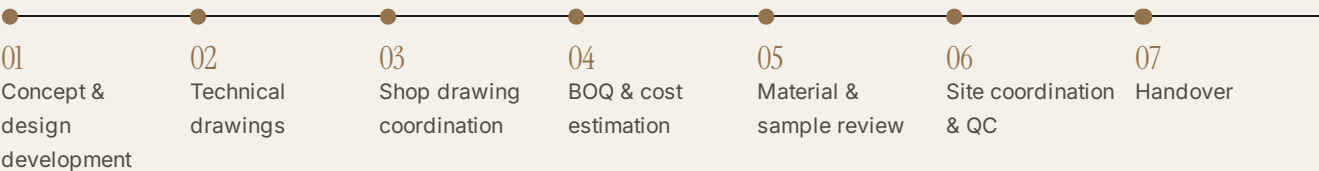

Steps condensed from the professional profile: concept and design development, technical drawings, material selection, BOQ preparation and pricing, supplier and contractor coordination, execution on site.

Every space. *Every detail.*

From the first sketch to the final handover — design authorship backed by the technical and site knowledge to deliver it.

01 Interior design

Creative, functional concepts for luxury residential, commercial and retail interiors — planned around the way each space will be lived in and used.


Space planning & furniture layouts · Concept design & mood boards · Material & finish selection · Furniture design & custom joinery



WD Walnut



UP Velvet

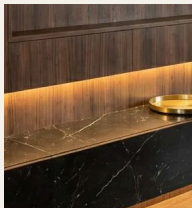

ST Marble




MATERIAL STUDY · THE WALNUT SUITE

02 Interior architecture

The architectural elements of the interior — entrances, ceilings, partitions and feature walls — designed as one coherent whole.

Entrance & foyer design · Decorative ceilings · Feature walls & partitions · Staircase areas

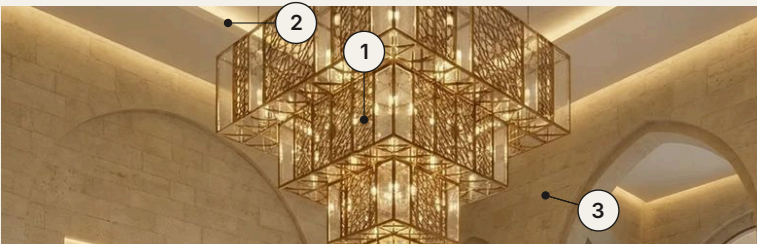


1 Chandelier on the axis 2 Ceiling cove 3 Stone arch

03 Technical & shop drawings

Preparing technical drawings and coordinating shop drawings so that the design can be built exactly as intended.

Technical drawings · Shop drawing coordination · Construction & execution details

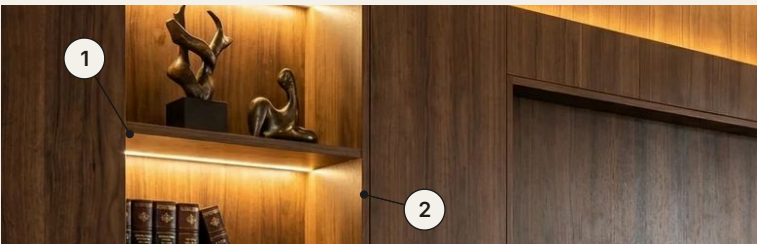

1 Lit shelf → CD-01, p. 24 2 Media wall → DD-02, p. 23

04 BOQ & cost estimation

Bills of quantities, take-offs and cost estimates, with interior works priced and quotations coordinated with suppliers and subcontractors.

BOQ & quantity take-off · Cost estimation & pricing · Supplier quotations


REF	ITEM	UNIT	QTY	RATE
1.01	Gypsum ceiling with lighting cove	m ²	48.0	—
1.02	Veneer wall panelling on battens	m ²	22.5	—
1.03	Built-in wardrobe, glass doors, LED	m	4.8	—

BOQ FORMAT · SAMPLE VALUES · RATES OMITTED

05 Fit-out & coordination

Coordinating clients, contractors, suppliers, factories and site teams, and reviewing material samples against the project specifications.

Joinery & woodwork · Stone, marble & glass · Steel & metal fabrication · Lighting coordination

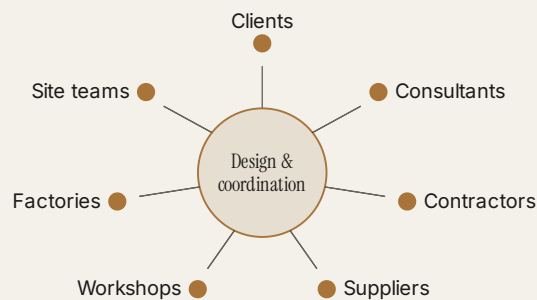

COORDINATION — PARTNERS NAMED IN THE PROFILE

06 Site supervision

Following execution on site, resolving technical and design issues and maintaining quality from design approval through to final handover.

Site inspections · Quality control · Handover

- ☒ Material samples reviewed against specification
- ☒ Shop drawings coordinated for execution
- ☒ Site inspection — quality standards
- ☒ Technical and design issues resolved
- ☒ Detail managed through to handover

REPRESENTATIVE CHECKLIST FORMAT


07 3D visualization

Concepts made tangible through 3D modeling, rendering and design presentation — exploring proportion, light and texture before execution begins.

3ds Max · V-Ray · Chaos Vantage · Blender · Design presentation



Render Reception hall, Fig. 01

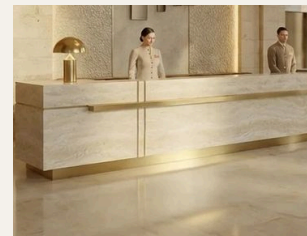

Detail Counter and floor

FROM RENDER TO DETAIL · AN ARCHED RETREAT

TOOLKIT

AutoCAD · 3ds Max · V-Ray · Chaos Vantage · Blender · Photoshop · Illustrator · Figma


TYPICAL DELIVERABLES

Concept and mood boards · space planning and furniture layouts · technical and shop drawings · BOQs and cost estimates · material selections · 3D visualisation


REPRESENTATIVE FORMATS The table, diagram and checklist on this spread were prepared for this portfolio to show method. Renders are Alaa Masri's visualisations.

Selected *works*

A closer look. *Seven design stories — each told through its own strengths.*

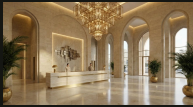01		An arched retreat	HOSPITALITY — DESIGN STUDY	09
02		The skyline suite	RESIDENTIAL — BEDROOM	15
03		The walnut suite	RESIDENTIAL — BEDROOM	20
04		The illuminated villa	ARCHITECTURE — EXTERIOR	26
05		Living by the garden	RESIDENTIAL — LIVING	30
06		The burgundy salon	RESIDENTIAL — LIVING	34
07		An earthy welcome	RESIDENTIAL — MAJLIS	36

Locations, years, roles, scope and project status are marked "To confirm" until verified.

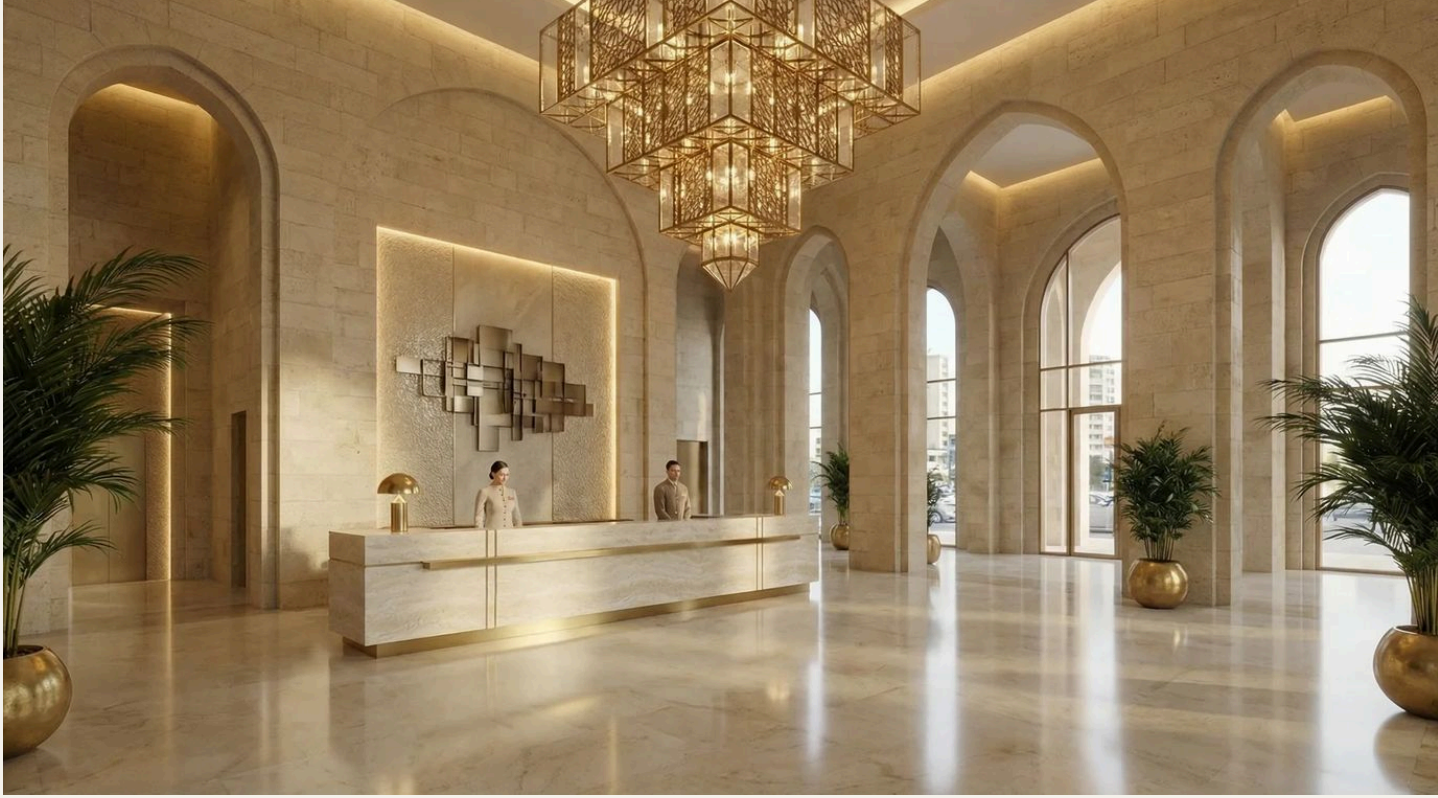

SELECTED WORKS — 01 / 07

Fig. 01 Arched reception hall with a stone-clad counter, gold chandelier and polished marble floor.

01 An arched retreat

CONCEPT

A hospitality design study connecting vaulted interiors, dining spaces, guest accommodation and quiet leisure areas.

CATEGORY Hospitality — Design study

LOCATION To confirm

YEAR To confirm

ROLE To confirm

SCOPE To confirm




Limestone
#957953



Marble
#AC9B80



Gold
#916733

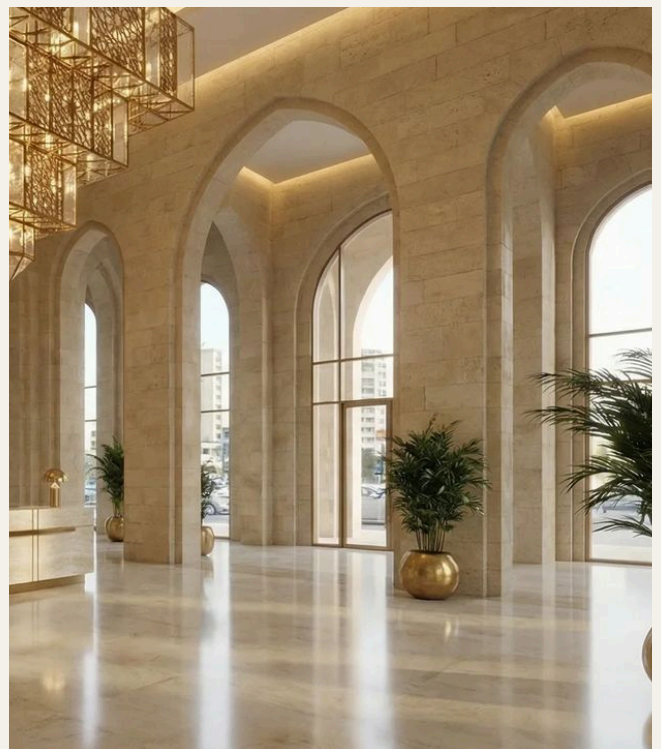


A Arched glazing and cove light, reception — Fig. 01

The arch as a system — *pier, opening, light.*



Fig. 03 All-day dining space with timber tables, a central bar and arched stone walls.


- KEY ELEMENTS
- 01 Pointed stone arches
 - 02 Stone piers and columns
 - 03 Integrated cove lighting
 - 04 Gold chandeliers
 - 05 Polished marble floors

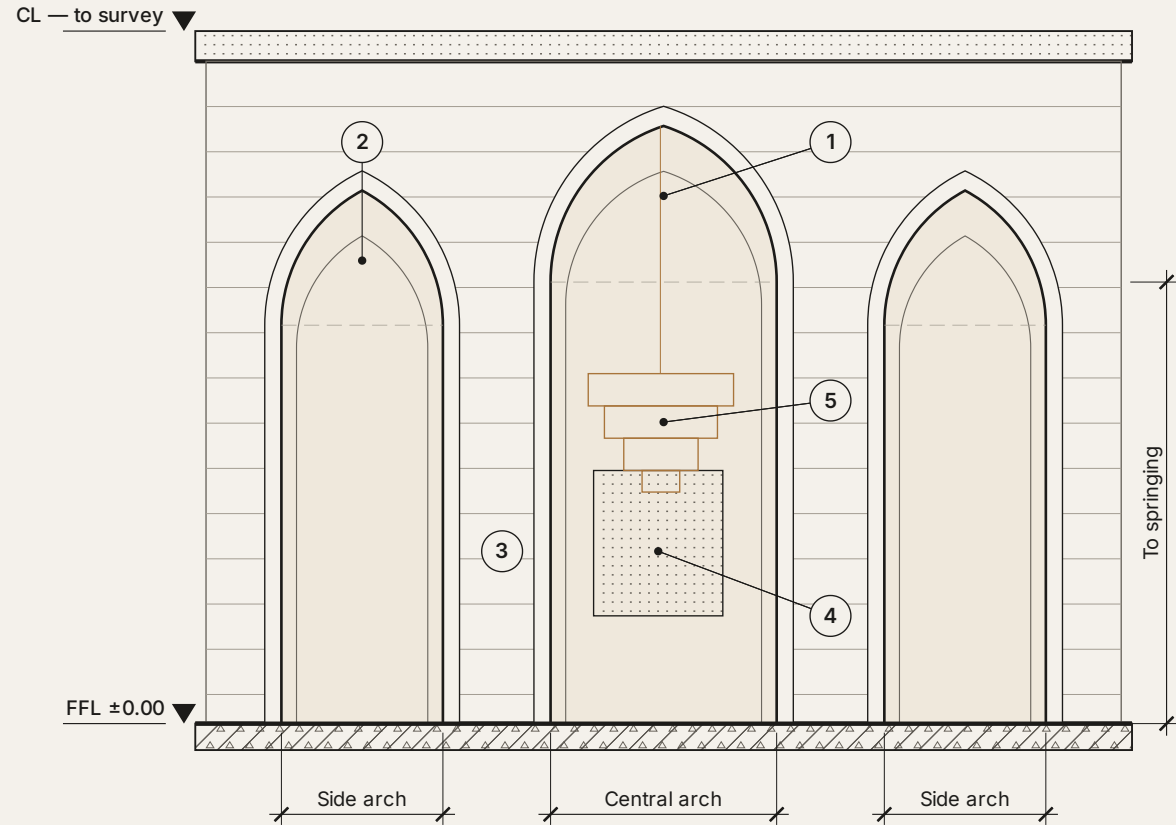

E1
DD-A1 **DINING — END WALL, ARCADE ELEVATION**
NTS · DESIGN DEVELOPMENT DIAGRAM · TRACED FROM FIG. 03


- | | | |
|--------------------------------|-----------------------------|--------------------------|
| 1 Central pointed arch | 3 Stone piers, coursed | 5 Chandelier on the axis |
| 2 Side arches, lower springing | 4 Artwork panel on the axis | — Arch sizes: to survey |

One arch language — *five openings, drawn to one span.*

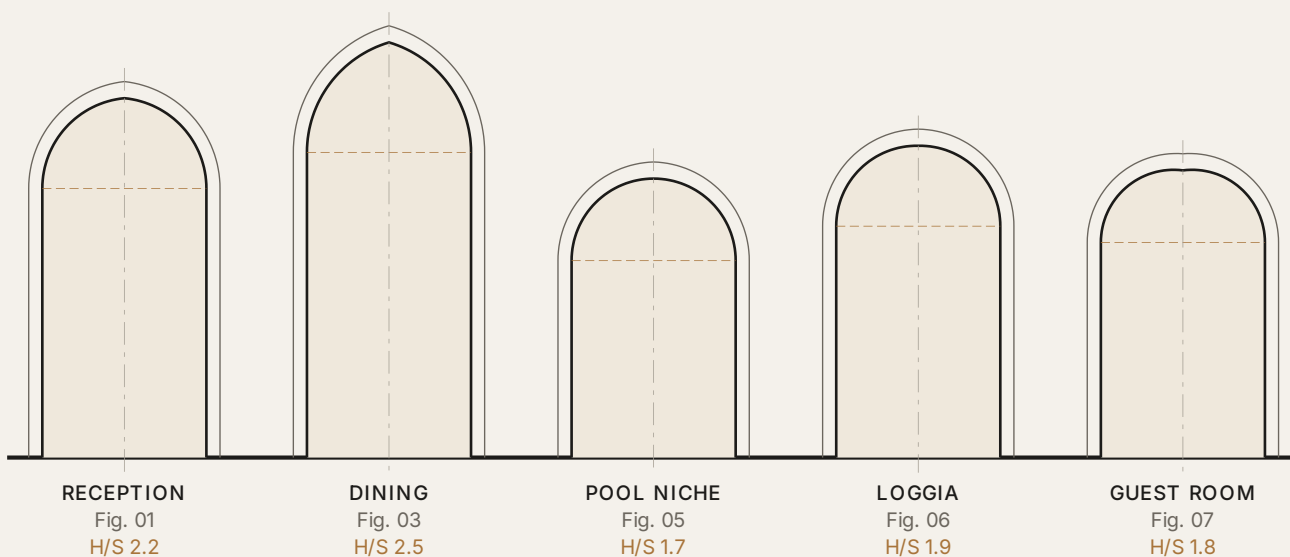

ARCH FAMILY — COMPARATIVE ELEVATION

COMMON SPAN · DESIGN DEVELOPMENT DIAGRAM · RATIOS READ FROM FIGS. 01-07

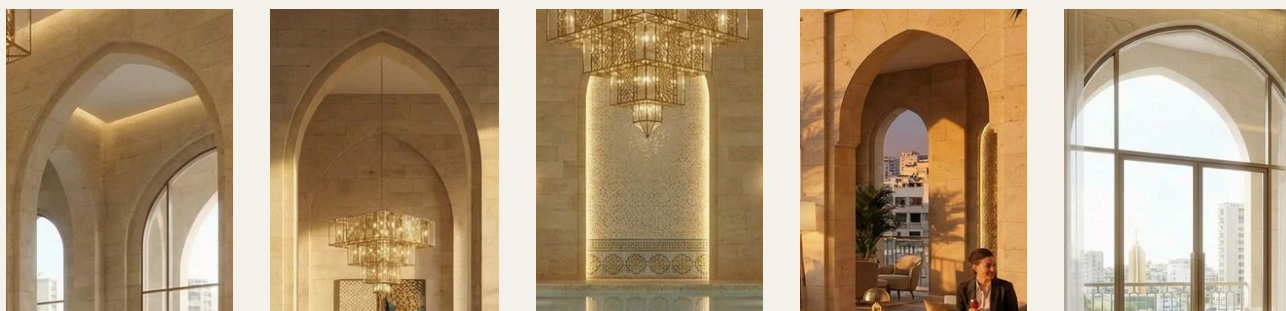

Above, each opening drawn to one span; below, the same opening as visualised. H/S compares overall height with span, read from the renders with their perspective.

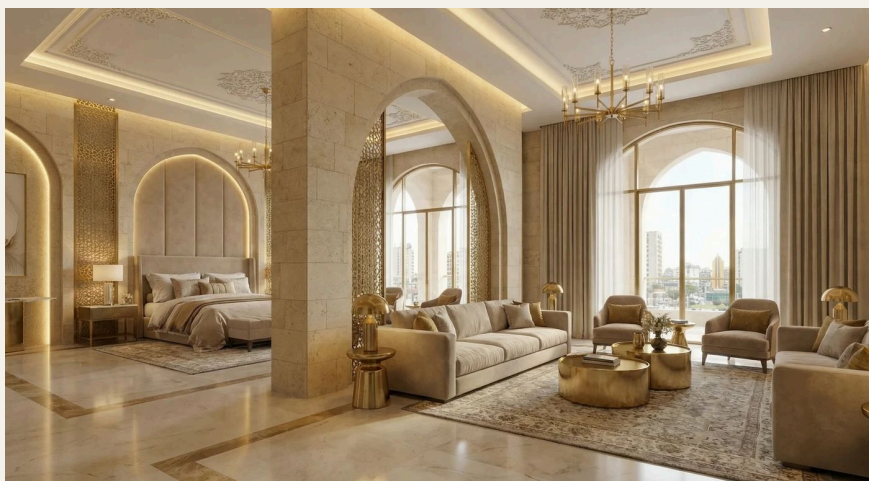


Fig. 02 Guest suite set beneath tall arches, with a lounge and city views.

SPACES IN THE STUDY

Reception hall	01
Guest suite	02
All-day dining	03
Banquet hall	04
Indoor pool	05
Rooftop lounge · guest room	06-07




01 — AN ARCHED RETREAT

Fig. 05 Indoor pool framed by illuminated arched niches and stone columns.

Light as material — *the pool hall.*

CL — to survey ▼

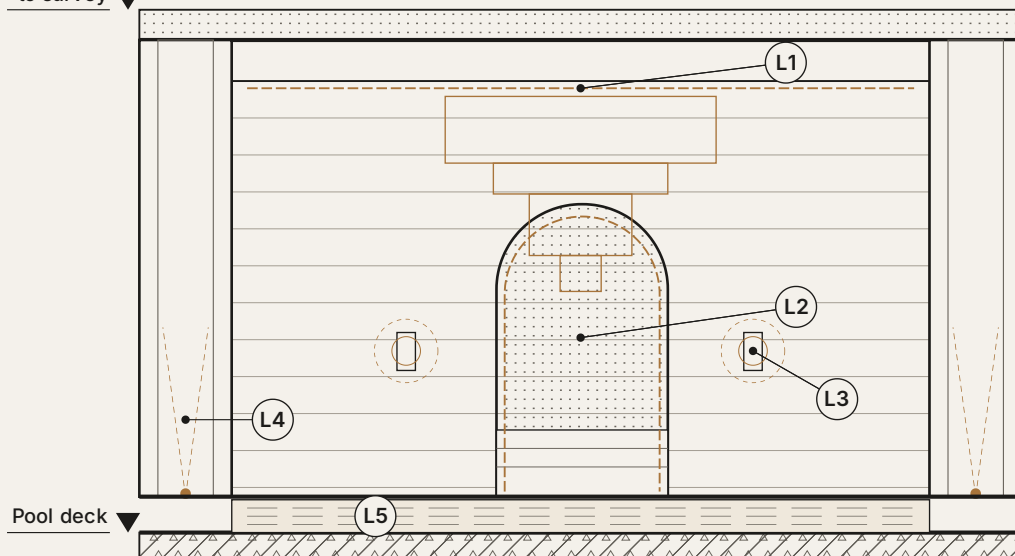

E1
DD-A3

POOL HALL — BACK WALL AND LIGHTING LAYERS

NTS · DESIGN DEVELOPMENT DIAGRAM · TRACED FROM FIG. 05

L1 Cove around the ceiling tray

L2 Back-lit mosaic niche

L3 Wall sconces either side

L4 Up-light washing each pier

L5 Underwater light


— Sizes: to survey

DIAGRAM Reads the lighting visible in the render; it is not a lighting design.



Fig. 04 Banquet hall laid for an event beneath chandeliers and tall arched windows at dusk.

01 — AN ARCHED RETREAT

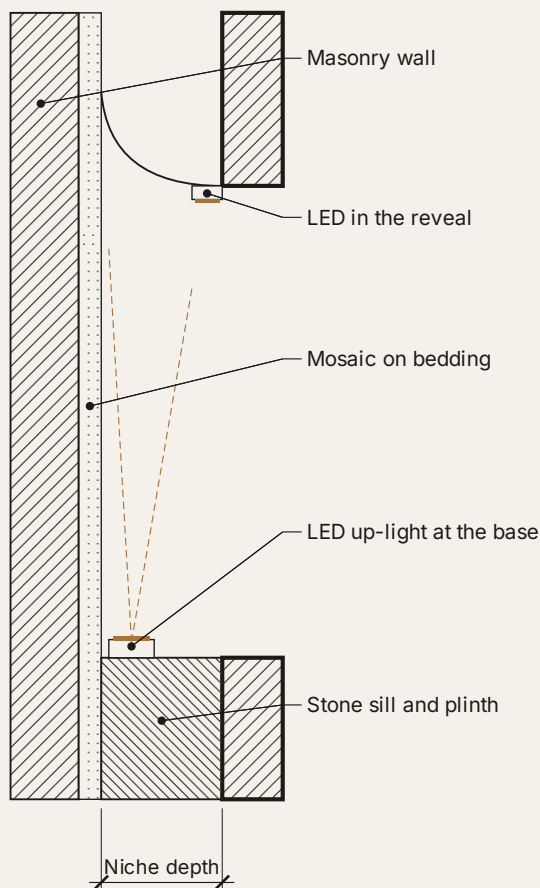

01
CD-A1

LIT NICHE — SECTION

NTS · CONCEPT DETAIL · FIG. 05



Fig. 06 Rooftop lounge beneath an arched loggia at sunset.

GOLD METALWORK — ONE FAMILY

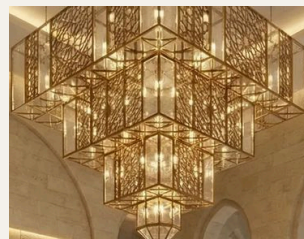


Fig. 01 Reception

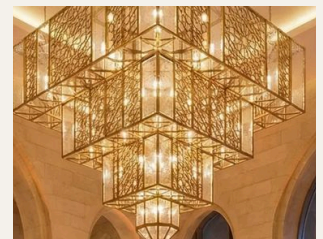



Fig. 04 Banquet hall

CONCEPT DETAIL CD-A1 suggests how a lit niche like the one in Fig. 05 could be built: stone reveal, mosaic back, concealed light at the base and perimeter. Sizes to be confirmed.




Fig. 07 Guest bedroom with arched windows, a stone feature wall and integrated cove lighting.


MATERIAL STUDY — CROPPED FROM THE VISUALISATIONS

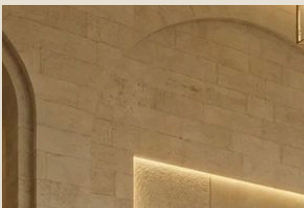


ST-01 Limestone
Walls, arches · Fig. 01

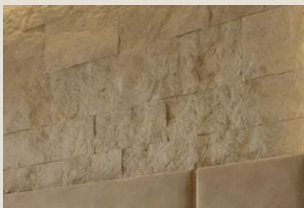

ST-02 Split-face stone
Feature wall · Fig. 07

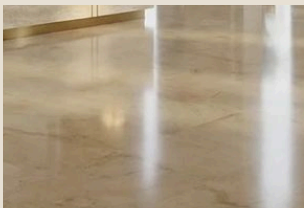


ST-03 Polished marble
Floors · Fig. 01

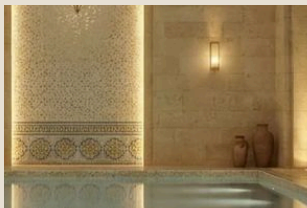

MO-01 Mosaic
Pool niche · Fig. 05



MT-01 Gold metalwork
Chandeliers · Fig. 01

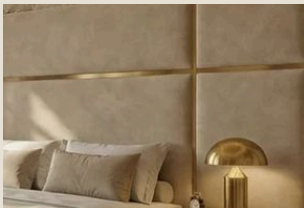

UP-01 Upholstery
Headboard · Fig. 07



Limestone
#957953 · Fig. 01



Polished marble floor
#AC9B80 · Fig. 01



Gold metalwork
#916733 · Fig. 01

FINISH CODES — MATERIAL STUDY, NOT A SPECIFICATION

ST-01 Limestone — walls, arches, piers
ST-03 Polished marble — floors

MT-01 Gold metalwork — chandeliers, planters
LT-01 Integrated cove and niche light


MATERIAL STUDY Swatches are pixels of the renders; colours are medians of named regions. Products and suppliers: to specify.



SELECTED WORKS — 02 / 07

Fig. 01 Timber-lined bedroom with floor-to-ceiling windows overlooking a city skyline at night.

02 The skyline suite

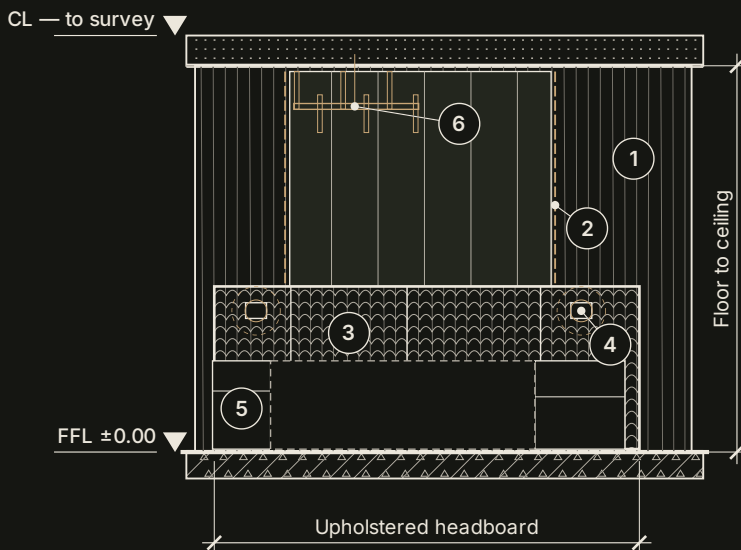

A timber-lined bedroom with skyline views, illuminated wardrobes and coordinated material details.

CATEGORY Bedroom

LOCATION To confirm

YEAR To confirm

ROLE To confirm

SCOPE To confirm

E1
DD-S1

HEADBOARD WALL

NTS · DESIGN DEVELOPMENT · FIG. 01

- | | | | |
|---|------------|---|-------------|
| 1 | Walnut | 4 | Wall lights |
| 2 | Lit reveal | 6 | Pendant |
| 3 | Headboard | 5 | Bedside |




02 — THE SKYLINE SUITE


Fig. 02 The bedroom looking towards the illuminated glass-fronted wardrobes.

Wood, fabric, leather — *warm tones.*


PALETTE — CROPPED FROM THE PROJECT MATERIAL BOARD, FIG. 06, LABELS AS ON THE BOARD

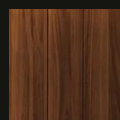


Wall panelling
Walnut, vertical grain

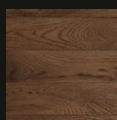


Flooring
Dark oak hardwood

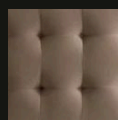


Headboard
Taupe velvet

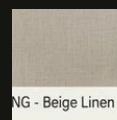


Bedding
Beige linen

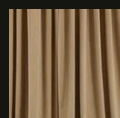

Curtains
Gold-beige drapery

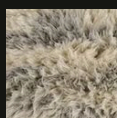

Rug
Cream shag pile

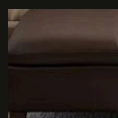

Bench
Dark brown leather



Accent pillow
Woven brown leather



Fig. 06 Material palette board: panelling, flooring, bedding, curtains, rug and leather.

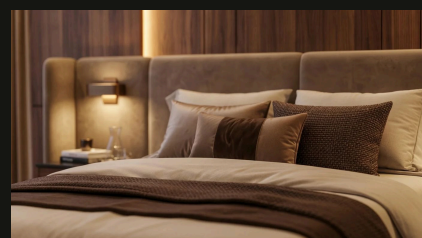


Fig. 03 Layered linens, upholstered headboard.



Walnut panel
#552D14




Taupe velvet
#533721



Fig. 04 Illuminated walk-in wardrobe with glass doors and walnut frames.

02 — WARDROBE DEVELOPMENT

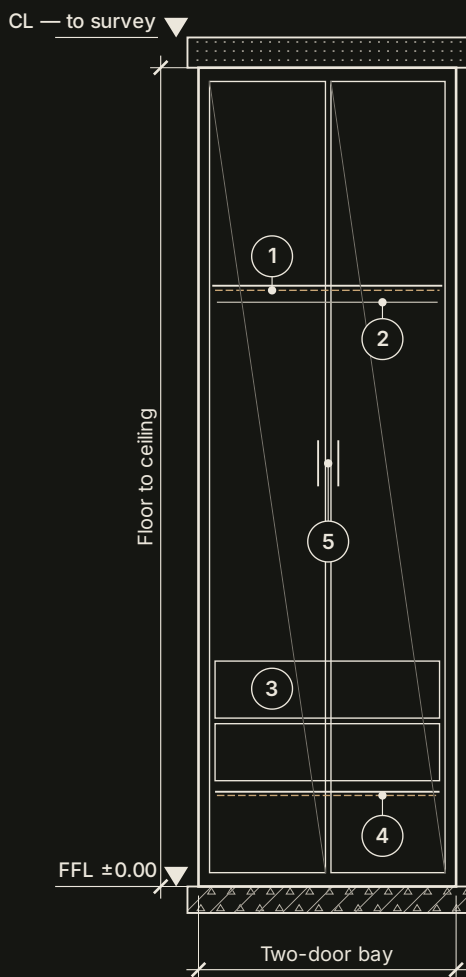

One bay



Fig. 05 Brass and glass pendant.

DD-S4 · KEYNOTES

- 1 LED to the top shelf
- 2 Hanging rail
- 3 Drawers
- 4 Lit shoe display
- 5 Glass doors, walnut frames



4 Lit shoe display along the base, enlarged


DIAGRAM DD-S4 is traced from the proportions of Fig. 04; it is not a shop drawing.

E3
DD-S4

WARDROBE BAY


NTS · DESIGN DEVELOPMENT · FIG. 04

Sleep, lounge, dress — *one room, three zones.*

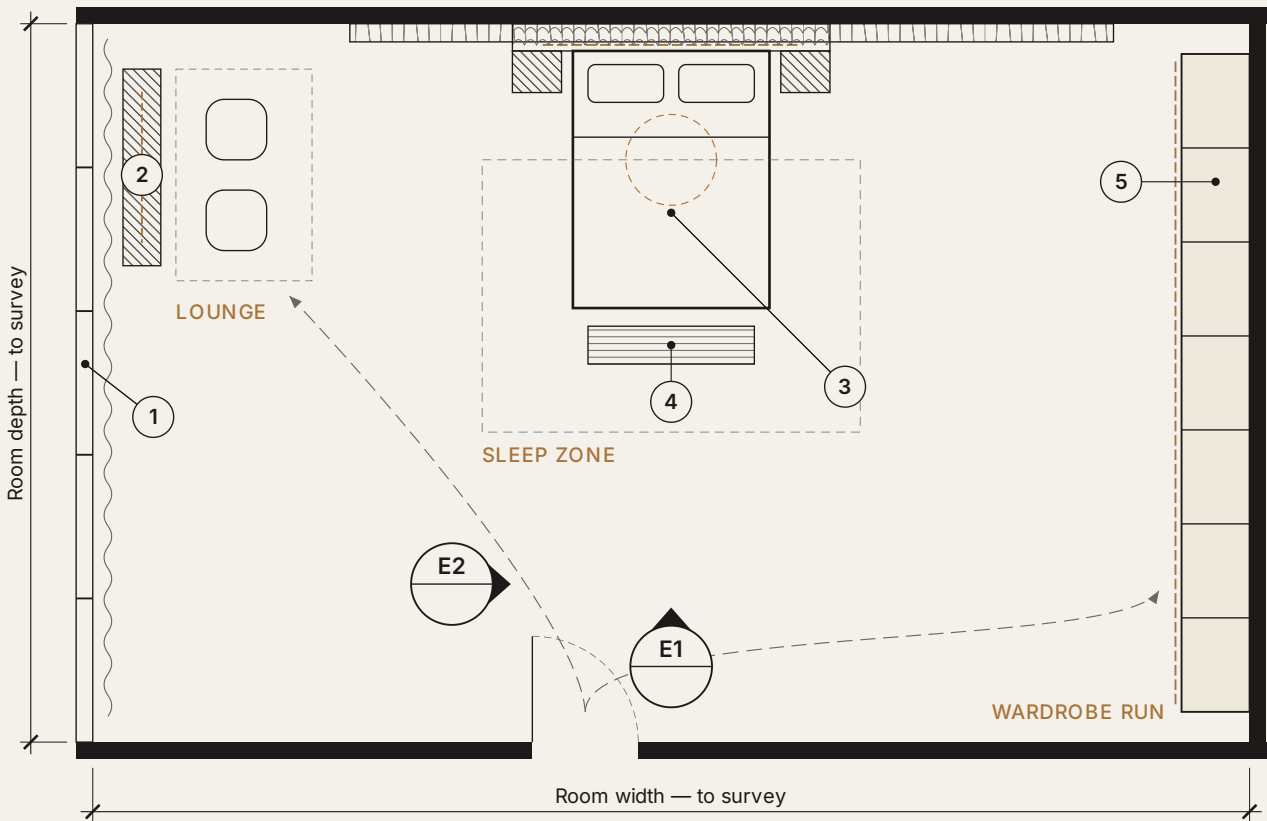

01 LAYOUT READING — BEDROOM

NTS · CONCEPTUAL SPACE STUDY · READS FIGS. 01 + 02

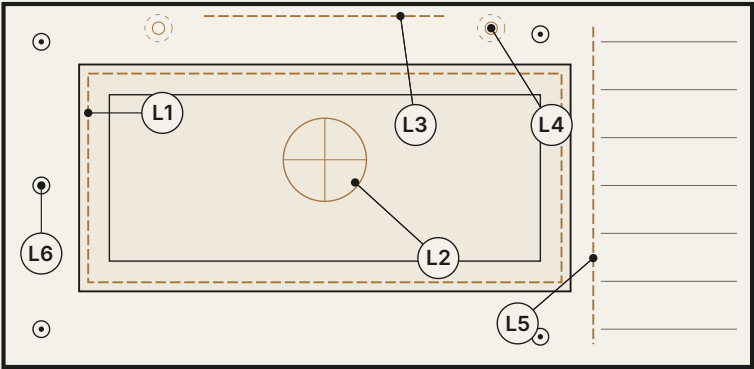

01 · KEYNOTES

- 1 Full-height glazing
- 2 Linear fire feature
- 3 Bed, panelled wall
- 4 Leather bench
- 5 Glass-fronted wardrobes

02 · LIGHTING LAYERS

- L1 Cove in the ceiling tray
- L2 Pendant — Fig. 05
- L3 Lit headboard recess
- L4 Wall lights either side
- L5 LED inside the wardrobes
- L6 Recessed downlights

02 LIGHTING LAYERS

NTS · READS FIGS. 01, 02, 04


PROJECT	SHEET TITLE	DWG NO.	STATUS	SCALE	ISSUE
The skyline suite	Layout · lighting layers	DD-S2/S3	Conceptual space study	NTS	2026–27



L2 Pendant — brass frame, glass rods · Fig. 05



L4 Wall lights on the headboard · Fig. 01

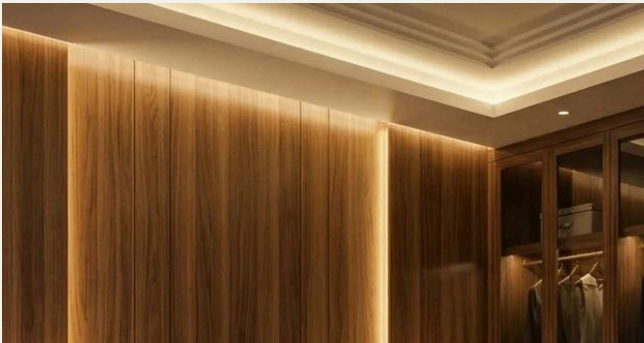

L1 · L3 Cove and lit panel reveals · Fig. 02



L5 Lit hanging bays behind glass · Fig. 04

MATERIAL STUDY — SAMPLED FROM THE VISUALISATIONS



Walnut wall panelling
#552D14 · Fig. 01

TIMBER

Walnut panelling, vertical grain; dark oak floor



Taupe velvet headboard
#533721 · Fig. 01

FABRIC

Taupe velvet, beige linen, gold-beige drapery



Dark oak floor
#4D2711 · Fig. 01

LEATHER

Dark brown bench, woven leather pillow



Dark leather bench
#462D1B · Fig. 01

LIGHT

Cove, lit reveals, wall lights, wardrobe LED



Fig. 06 Board



Fig. 02 Wardrobe



Fig. 03 Bed

Design intent — to confirm, in Alaa's words.



SELECTED WORKS — 03 / 07

Fig. 01 Symmetrical bedroom with an upholstered burgundy headboard wall, walnut panelling and a glass pendant.

03 The walnut suite

CONCEPT

Rich walnut, burgundy accents and integrated lighting connect the bedroom and its bespoke joinery.

CATEGORY Residential — Bedroom

LOCATION To confirm

YEAR To confirm

ROLE To confirm

SCOPE To confirm



Walnut

#3E2615



Velvet

#5F302D



Marble

#28251F



Brass

#F7C254



Linen

#917F6B




Light

#E8A880



A Headboard wall — walnut, velvet and lit reveals

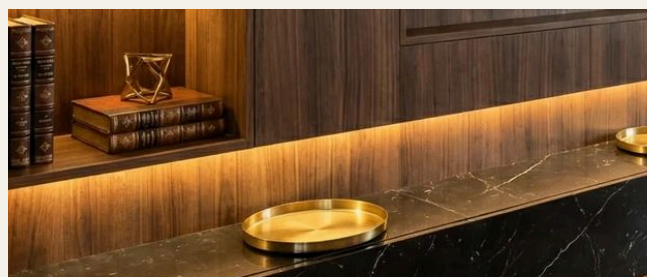


B Lit shelf, black marble ledge and brass — Fig. 03




Fig. 03 Walnut joinery, integrated shelving and concealed linear lighting.

- | | | | | | |
|---|------------------------------|---|---------------------------------------|---|---------------------------------------|
| 1 | LED under each shelf · LT-01 | 2 | Walnut veneer, vertical grain · WD-01 | 3 | Lit display niche |
| 4 | Framed media recess | 5 | Black marble ledge · ST-01 | 6 | Light line below the top band · LT-01 |


MATERIAL STUDY — CROPPED FROM THE VISUALISATIONS

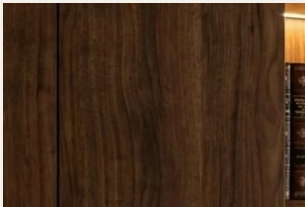

WD-01 Walnut veneer
Fig. 03

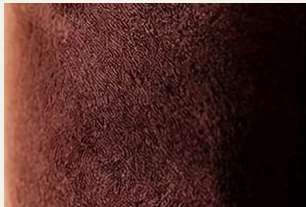

UP-01 Burgundy velvet
Fig. 05

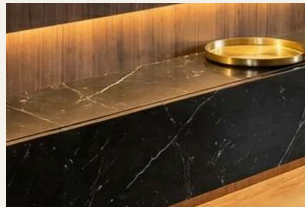

ST-01 Black marble
Fig. 03




LT-01 Lit reveal, warm white
Fig. 05

CODE	SAMPLE	MATERIAL, AS VISUALISED	CHARACTER	LOCATION	PRODUCT
WD-01		Walnut veneer	Vertical grain	Panelling, media wall, joinery	To specify
UP-01		Burgundy velvet	Channel-upholstered	Headboard wall	To specify
ST-01		Black marble, white veining	Polished	Ledge, bedside tables	To specify
LT-01		Concealed linear light	Warm white	Shelves, reveals, ledge, cove	To specify
MT-01		Brass	Polished accent	Trays, accessories	To specify

MATERIAL STUDY Samples are cropped pixels of the visualisations; codes are portfolio references, not project codes. Products and suppliers stay open until specified.

Layout reading — *sleep zone, media wall, circulation.*

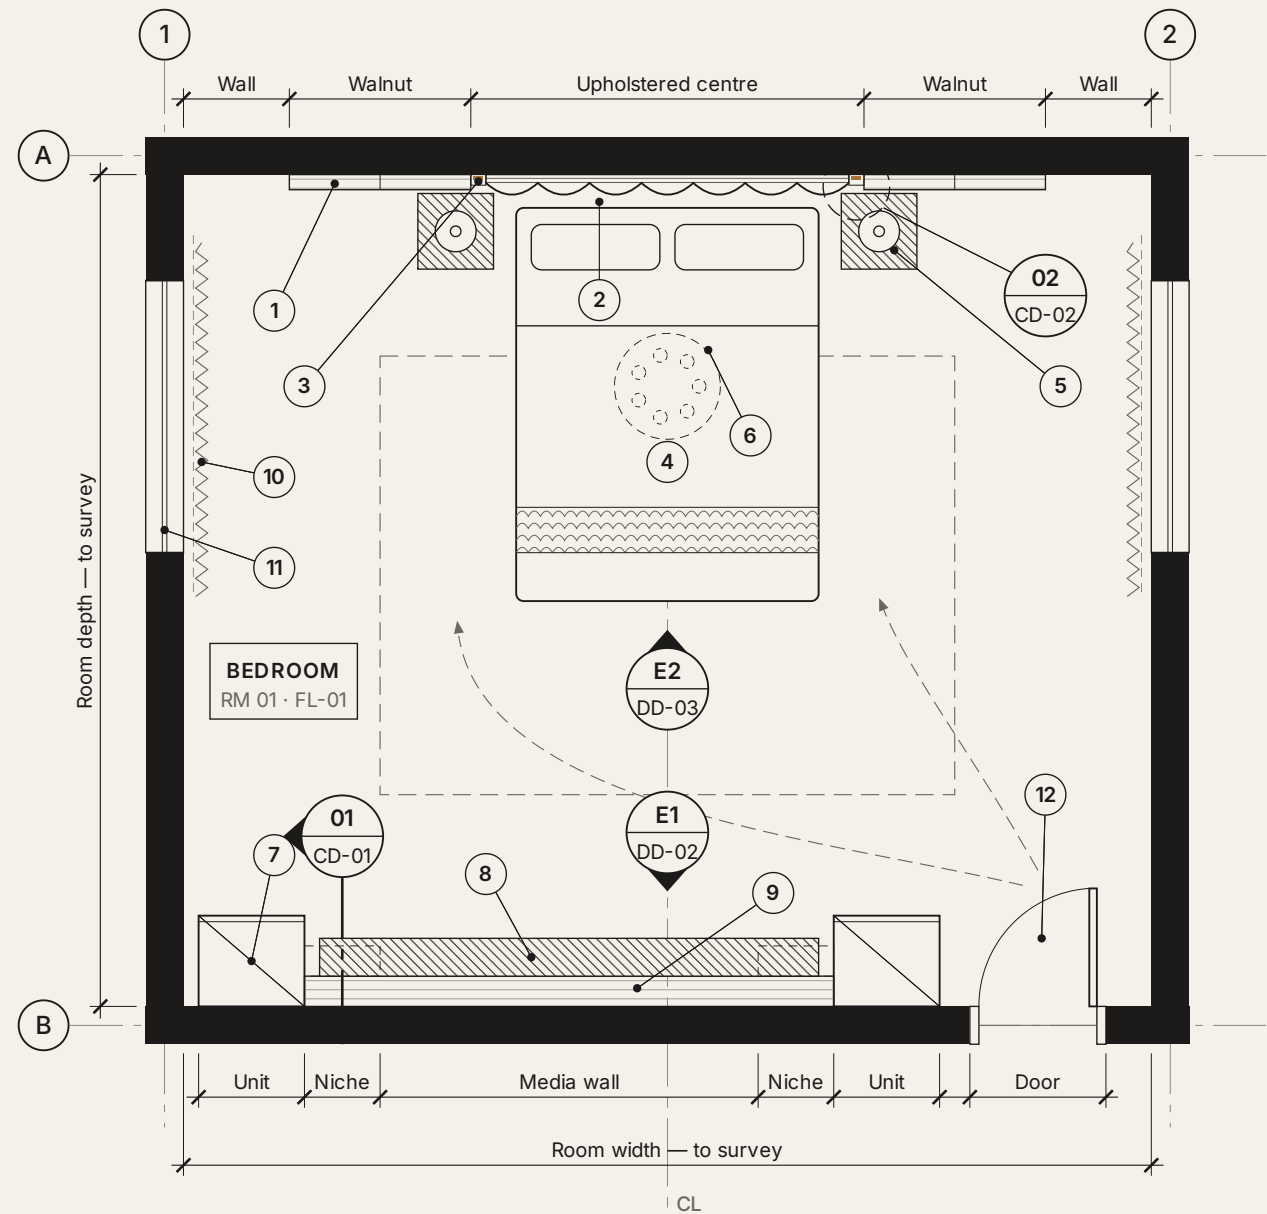

01 LAYOUT READING — BEDROOM
DD-01


NTS · CONCEPTUAL SPACE STUDY · READS FIG. 01 + 02

- | | | |
|-------------------------------|----------------------------------|----------------------------|
| 1 Walnut panelling · WD-01 | 6 Pendant cluster (above) | 11 Window |
| 2 Upholstered centre · UP-01 | 7 Tall unit, flush doors · WD-01 | 12 Door |
| 3 Lit vertical reveal · LT-01 | 8 Stone ledge · ST-01 | FL-01 Dark timber floor |
| 4 Bed | 9 Media recess (above ledge) | — Dashed: above / in front |
| 5 Bedside table · ST-01 | 10 Full-height drapery | |

CONCEPTUAL SPACE STUDY Reads the two visualised elevations, Fig. 01 and Fig. 02. Not a survey: sizes, openings and orientation are to be confirmed; dimension strings are named, not measured.

PROJECT	SHEET TITLE	DWG NO.	STATUS	SCALE	ISSUE
The walnut suite	Layout reading — bedroom	DD-01	Conceptual space study	NTS	2026–27


Elevations — *media wall and headboard wall.*

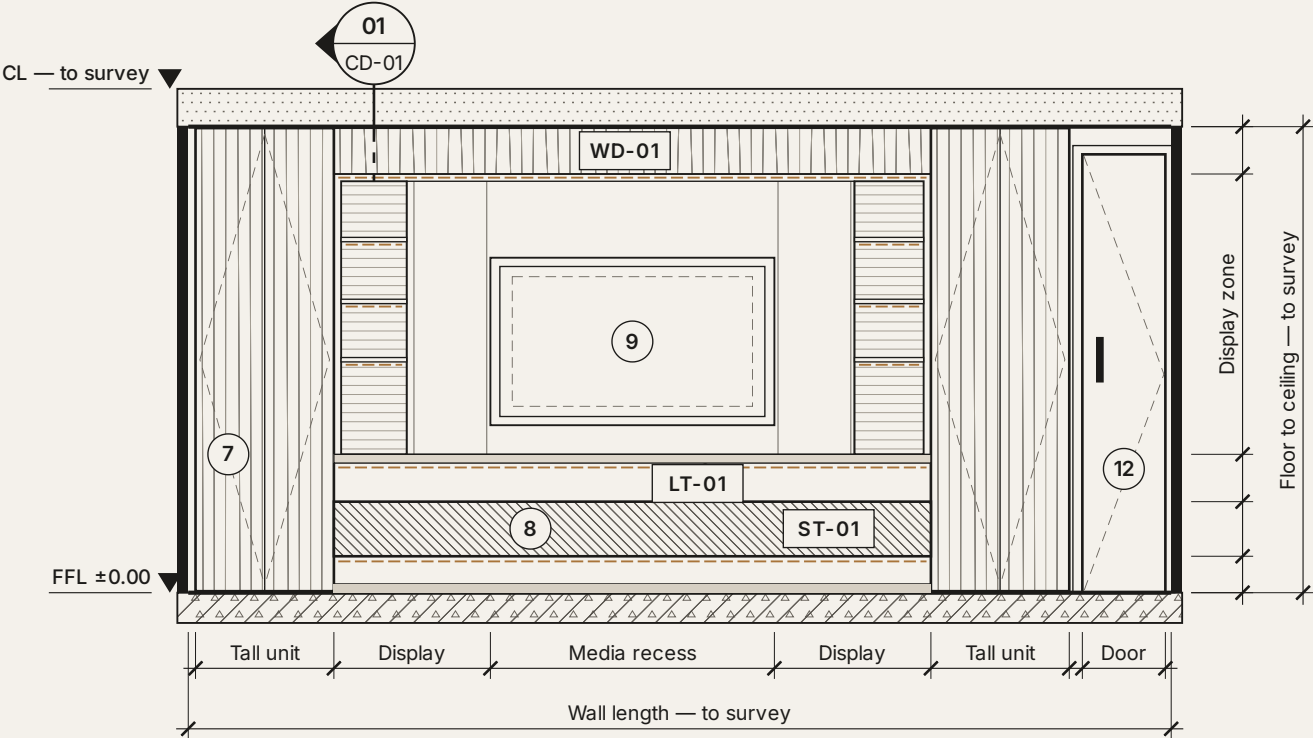

E1
DD-02

MEDIA WALL — ELEVATION

NTS · DESIGN DEVELOPMENT DIAGRAM · TRACED FROM FIG. 02

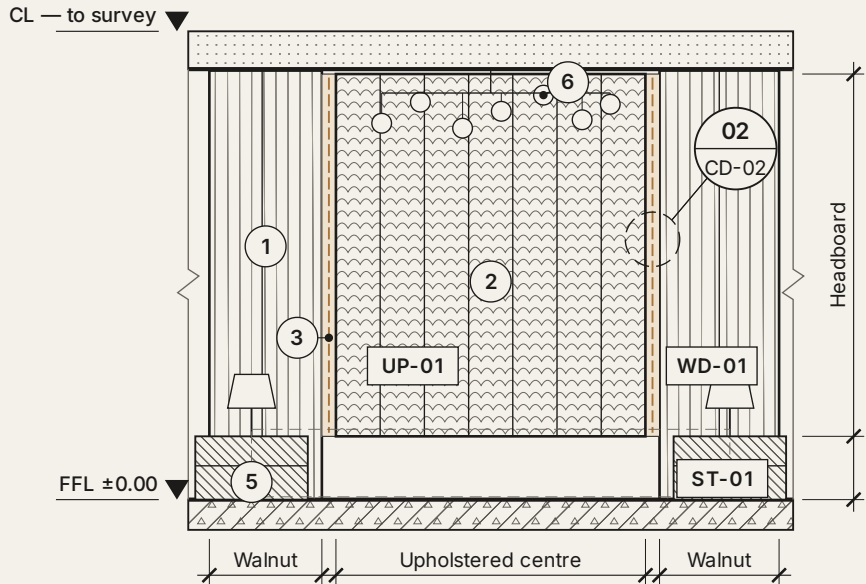

E2
DD-03

HEADBOARD WALL — ELEVATION

NTS · DESIGN DEVELOPMENT · FIG. 01

KEYNOTES

- 1 Walnut panelling
- 2 Upholstered centre
- 3 Lit vertical reveal
- 5 Bedside table
- 6 Pendant cluster
- 7 Tall unit, flush doors
- 8 Stone ledge, lit below
- 9 Media recess
- 12 Door

FINISH CODES

- WD-01 Walnut veneer
- UP-01 Burgundy velvet
- ST-01 Black marble
- LT-01 Linear light (dashed)


PROJECT	SHEET TITLE	DWG NO.	STATUS	SCALE	ISSUE
The walnut suite	Media wall · headboard wall	DD-02/03	Design development	NTS	2026-27

KEYNOTES — 01

- 1 Blockwork wall
- 2 Plaster skim
- 3 Timber batten 25 × 50 on packers
- 4 18 mm MR MDF back panel
- 5 Walnut veneer, matt lacquer · WD-01
- 6 25 mm veneered shelf, solid walnut lipping
- 7 Concealed steel support, resin-anchored
- 8 Recessed LED profile, opal diffuser · LT-01
- 9 Cable route to accessible driver void
- 10 5 mm shadow gap




Fig. 03 The shelf as visualised

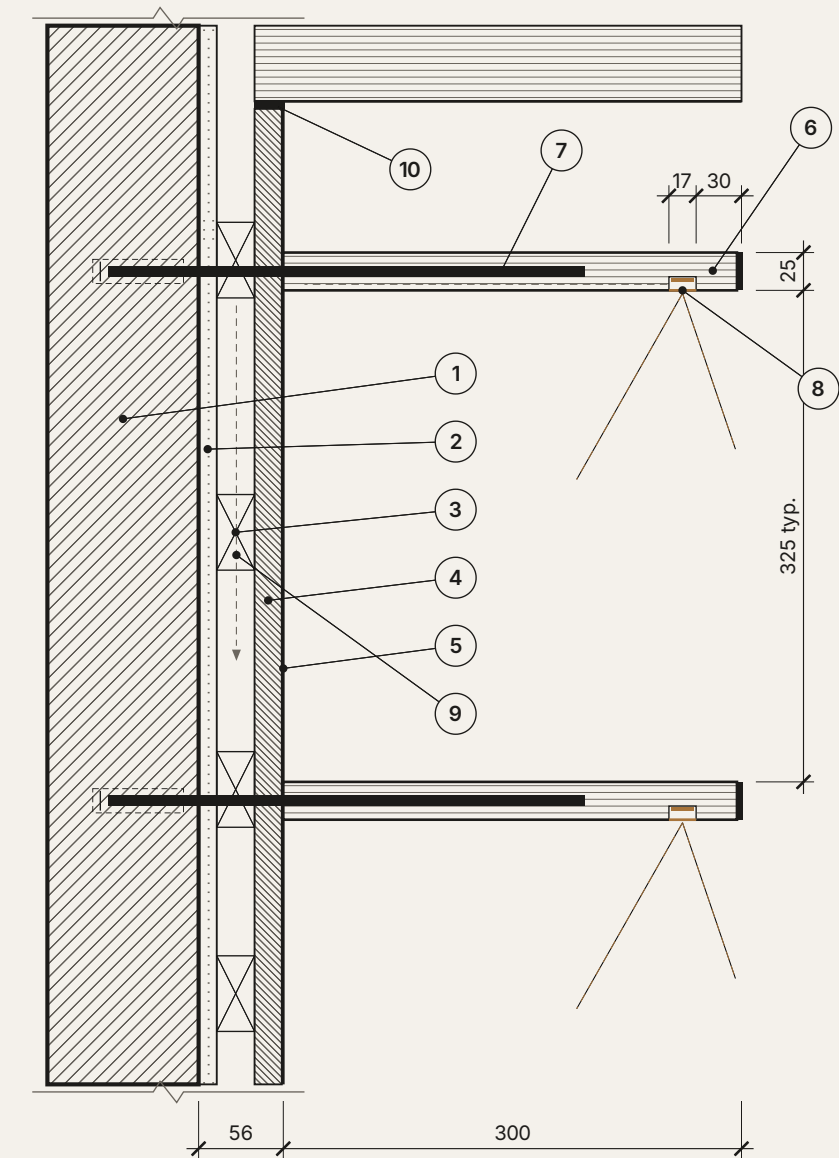

01
CD-01

LIT SHELF — SECTION

NTS · CONCEPT DETAIL · TYPICAL SIZES

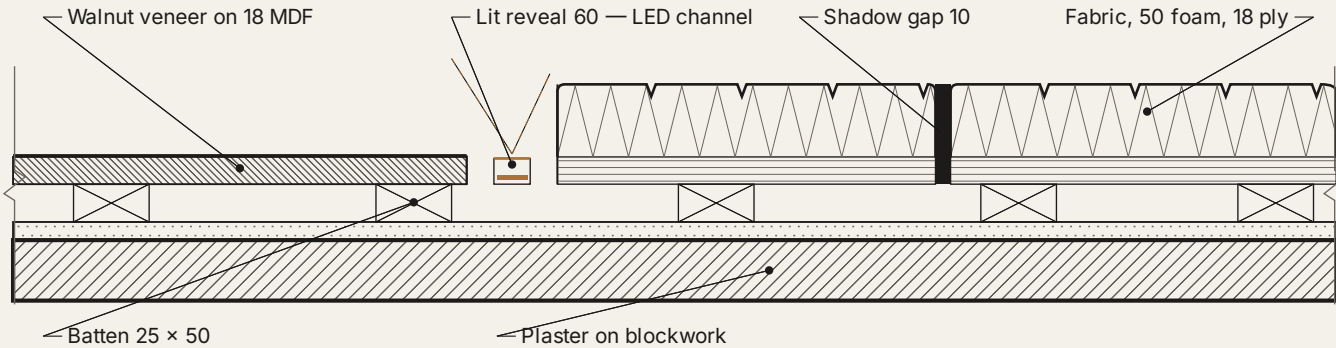

02
CD-02

WALNUT / LIT REVEAL / UPHOLSTERY — PLAN SECTION

NTS · CONCEPT DETAIL · TYPICAL SIZES · READS FIG. 05

PROJECT	SHEET TITLE	DWG NO.	STATUS	SCALE	ISSUE
The walnut suite	Lit shelf · reveal junction	CD-01/02	Concept detail	NTS · typ.	2026-27



Fig. 02 Opposite wall of the suite: a walnut media unit with lit shelving and a stone ledge.

03 — DESIGN LANGUAGE

Walnut, velvet, stone — *and light held in the joinery.*

KEY ELEMENTS — AS VISUALISED

- 01 Upholstered burgundy headboard wall
- 02 Walnut panelling and bespoke joinery
- 03 Integrated, concealed linear lighting
- 04 Lit display shelving and media recess
- 05 Black marble ledge and bedside surfaces

Design intent — to confirm, in Alaa's words.



Walnut veneer
#3E2615 · Fig. 03



Walnut, lit
#4D2A18 · Fig. 05



Burgundy velvet
#5F302D · Fig. 05



Black marble
#28251F · Fig. 02



Brass accent
#F7C254 · Fig. 03



Beige linen
#917F6B · Fig. 01

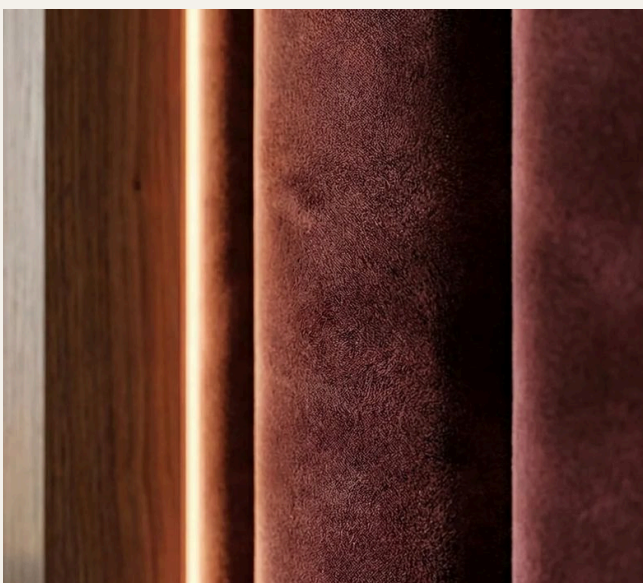


Fig. 05 Velvet meets walnut at a lit reveal — see CD-02

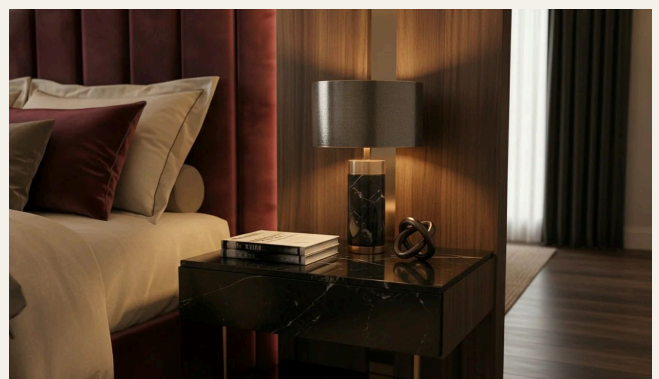


Fig. 04 Bedside: marble table, lamp, upholstered panels

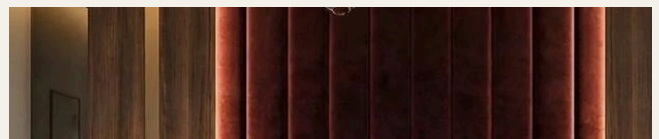


Fig. 01 Walnut panel and lit reveal, enlarged



SELECTED WORKS — 04 / 07

Fig. 02 The villa facade at dusk: cantilevered volumes, vertical screens and linear light.

04 The illuminated villa

A contemporary villa study exploring stone, vertical screening and architectural lighting from day to dusk.

CATEGORY Architecture — Exterior

LOCATION To confirm

YEAR To confirm

ROLE To confirm

SCOPE To confirm



Limestone
#F1D3B1




Timber
#5C4734



Warm light
#D09A58



A Linear light under the eaves — Fig. 02

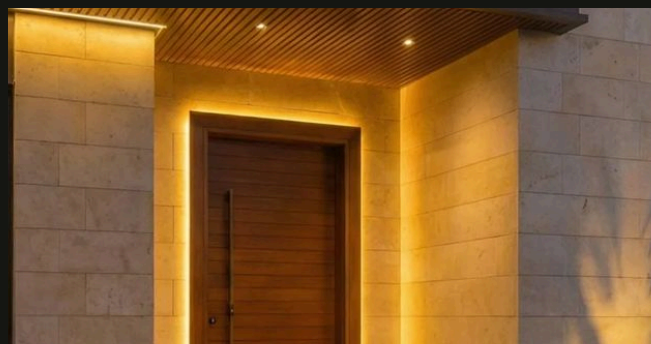


B Lit entrance canopy and timber door — Fig. 03



Fig. 04 Vertical timber screening and concealed lighting along the parapet.

04 — FACADE LIGHTING

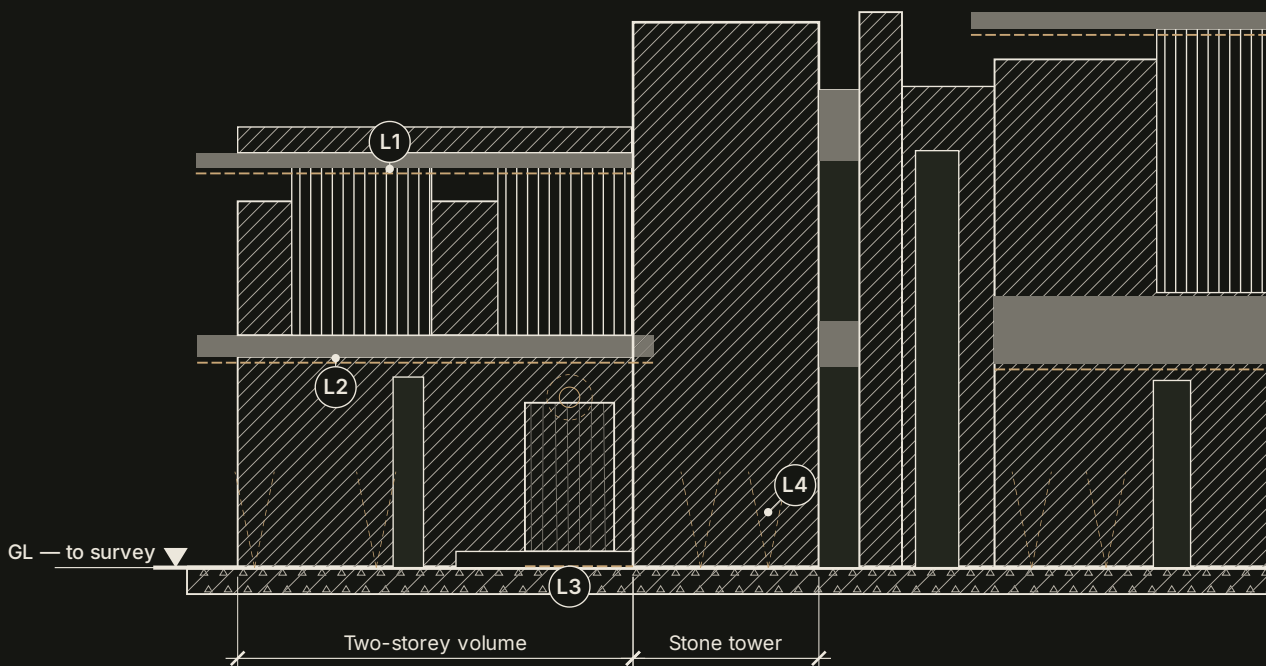

E2
DD-V2

FRONT ELEVATION — FACADE LIGHTING STRATEGY

NTS · DESIGN DEVELOPMENT DIAGRAM · FIG. 05, LIGHT READ FROM FIGS. 02–04

L1 Linear light under the roof eaves

L2 Linear light under the first-floor canopy


L3 Light line at the entrance step and door

L4 Ground up-lights washing the stone

DIAGRAM Lighting as visible in the dusk views — not a lighting or electrical layout.



Fig. 05 The villa in daylight: stone volumes, timber screens and a recessed entrance.

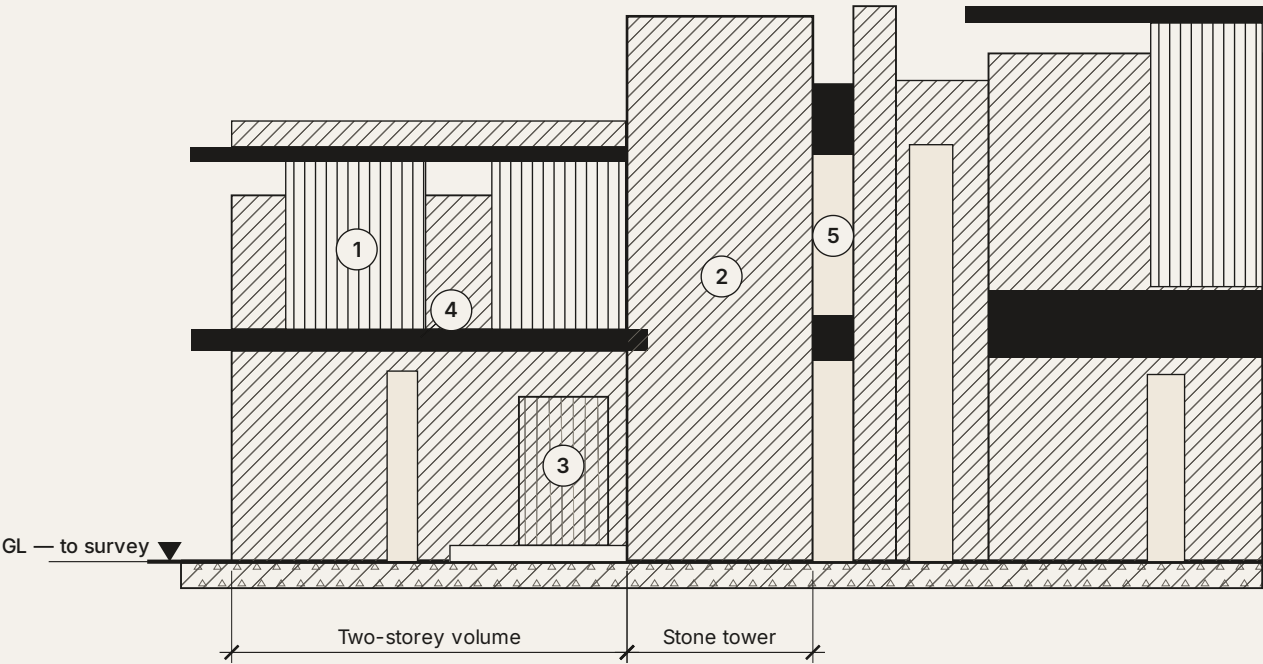

E1
DD-V1

FRONT ELEVATION — MASSING AND MATERIALS

NTS · DESIGN DEVELOPMENT DIAGRAM · TRACED FROM FIG. 05

- 1

Vertical timber screens
- 2

Stone tower, full height
- 3

Recessed timber entrance
- 4


Cantilevered canopy slab
- 5

Glazed slot between volumes
- Heights: to survey

PROJECT	SHEET TITLE	DWG NO.	STATUS	SCALE	ISSUE
The illuminated villa	Front elevation — massing	DD-V1	Design development	NTS	2026-27



Fig. 01 Aerial view with landscaped courtyards.

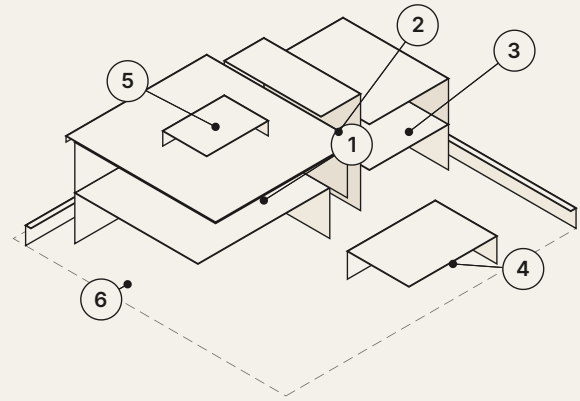

DD-V3 · VOLUMES

1	Main volume	4	Carport canopy
2	Stone tower	5	Roof screen
3	Second volume	6	Boundary wall



MASSING

NTS · CONCEPTUAL · FIG. 01

SECTION

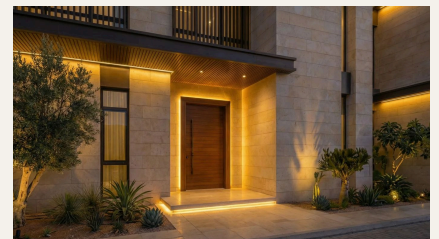
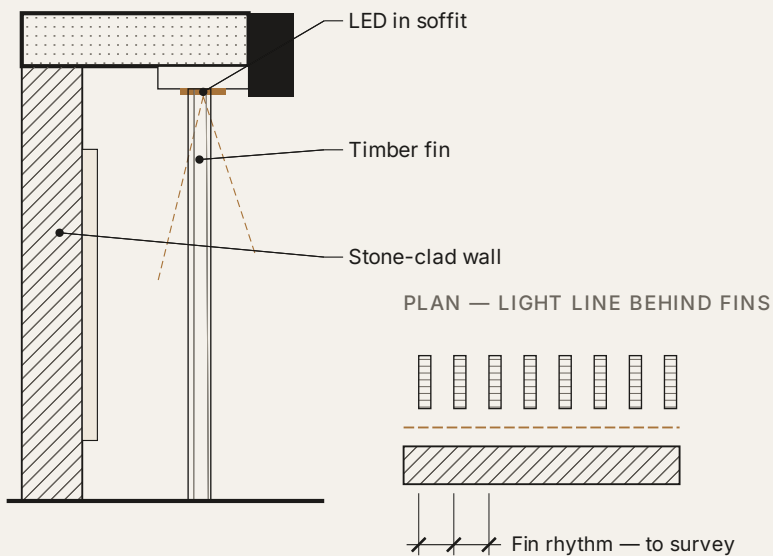


Fig. 03 Entrance canopy

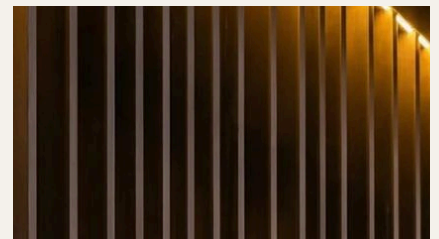


Fig. 04 Fins and soffit light


CONCEPTUAL Both drawings read the renders; sizes to be confirmed.




TIMBER SCREEN AND SOFFIT LIGHT

NTS · CONCEPT DETAIL · READS FIG. 04


MATERIAL STUDY — CROPPED FROM THE VISUALISATIONS

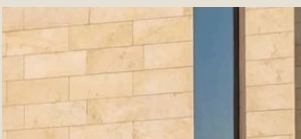


ST-01 Limestone

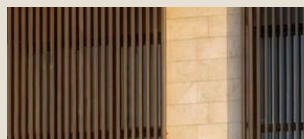

WD-01 Timber screen

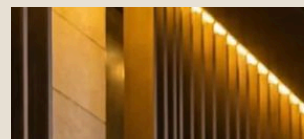

ST-01 Stone at dusk

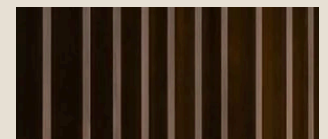

LT-01 Fins, lit



Fig. 01 Open-plan living and dining with a linear fireplace, timber wall and garden views.

05 Living by the garden

CATEGORY	LOCATION	YEAR	ROLE	SCOPE
Residential — Living	To confirm	To confirm	To confirm	To confirm


A warm family living and dining space with garden views, textured fabrics and a linear fireplace.



B Clerestory light — Fig. 02




C Boucle chair — Fig. 05

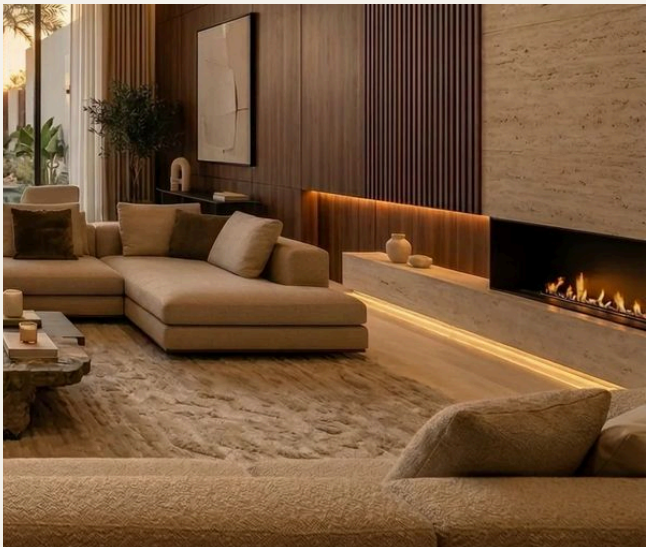

A Linear fireplace in travertine and walnut — Fig. 01

One open room — *cook, gather, look out.*

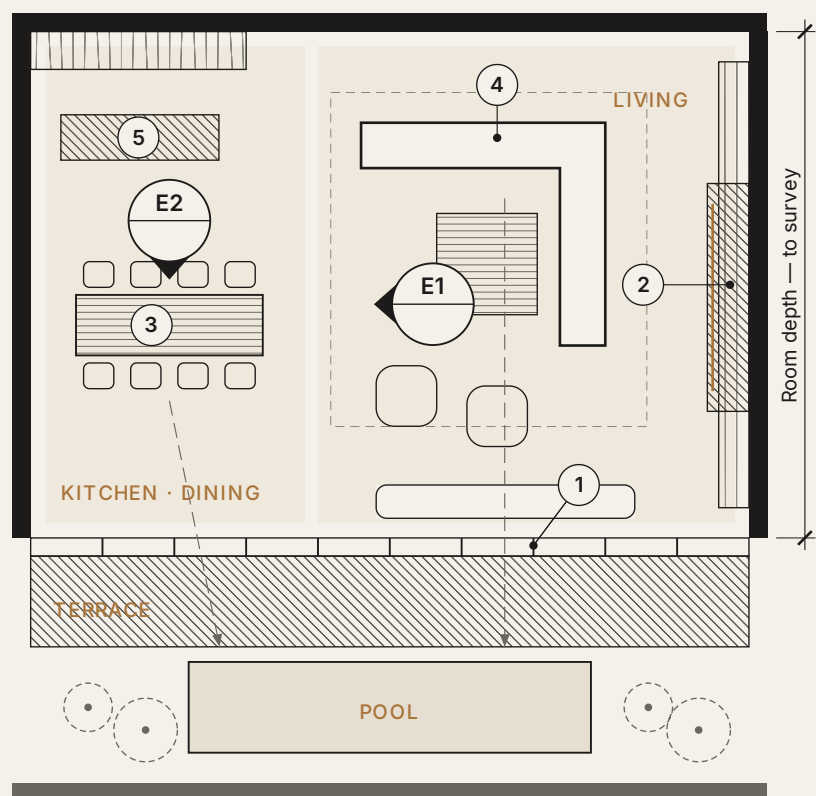

- KEYNOTES
- 1

Sliding glazing to the terrace
- 2

Fireplace wall — DD-G2
- 3

Timber dining table
- 4

L-shaped sofa
- 5

Kitchen island



E1 to the garden — Fig. 01




E2 from the dining table — Fig. 02

SPACE STUDY Reads Figs. 01 and 02 to show zoning, views and the indoor–outdoor link. Not a surveyed plan; sizes to survey.

01
DD-G1

LAYOUT READING

NTS · SPACE STUDY · FIGS. 01 + 02

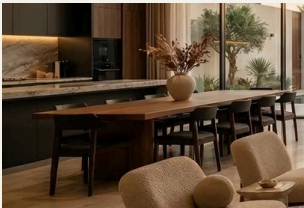

KITCHEN

Stone island, dark timber joinery



DINING

Long timber table, woven chairs



LIVING

Deep sofa, textured lounge chairs




TERRACE

Pool, palms and desert planting

PROJECT	SHEET TITLE	DWG NO.	STATUS	SCALE	ISSUE
Living by the garden	Layout reading — living	DD-G1	Conceptual space study	NTS	2026–27



Fig. 02 Timber dining table beneath a skylight, with palm-lined garden views at sunset.

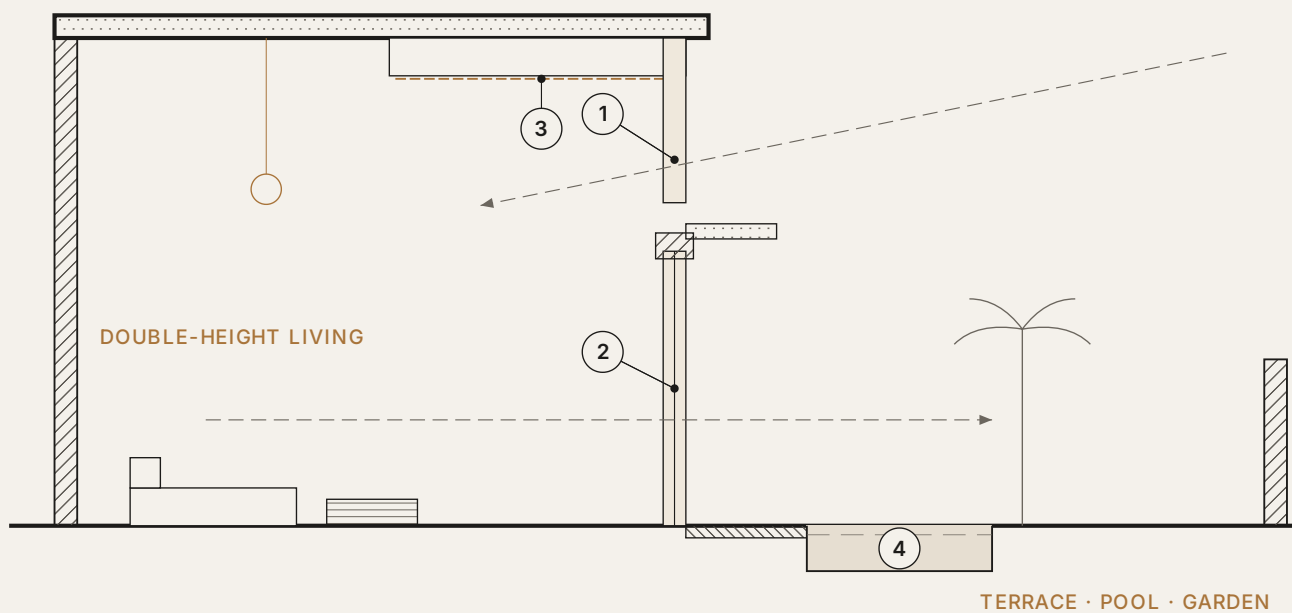

S1
DD-G3

INDOOR / OUTDOOR SECTION

NTS · CONCEPTUAL SECTION STUDY · READS FIGS. 01 + 02

- | | | | |
|---|------------------------------------|---|----------------------------|
| 1 | Clerestory glazing above the doors | 3 | Cove light at the bulkhead |
| 2 | Full-height sliding doors | 4 | Pool on the terrace |

SECTION STUDY The garden as the fourth wall. Heights and depths are not measured — to survey.



Fig. 03 Linear fireplace set into a textured stone wall with timber slats.



Fig. 05 Boucle lounge chair


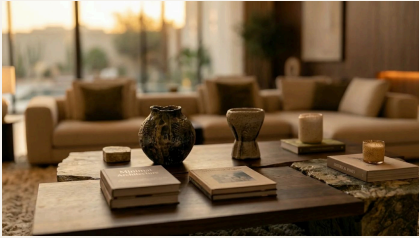


Fig. 04 Ceramics and layered textiles

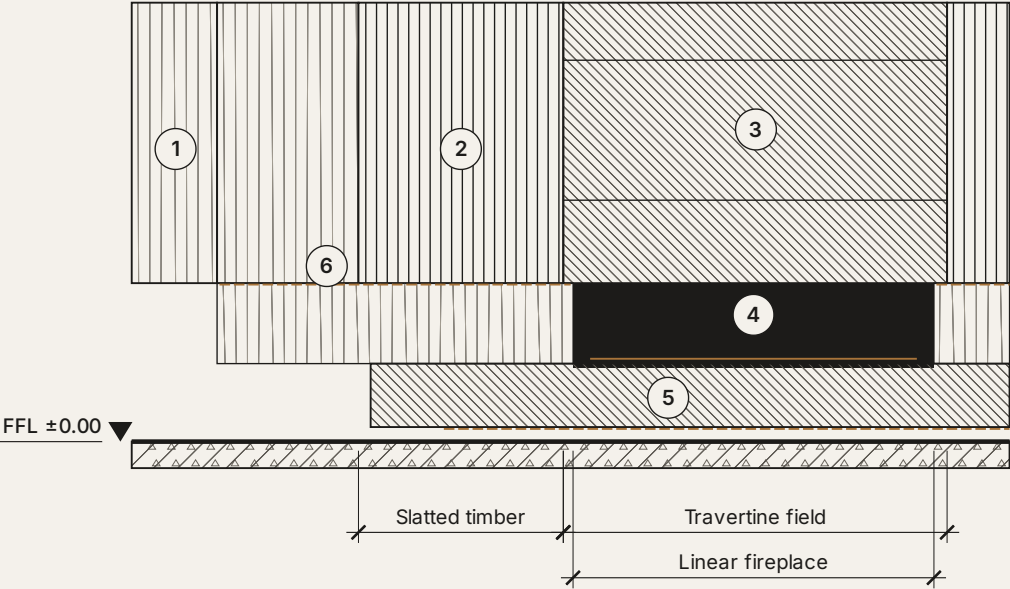

FIREPLACE WALL — ELEVATION

NTS · DESIGN DEVELOPMENT DIAGRAM · TRACED FROM FIG. 03

- | | | |
|----------------------|--------------------|-----------------------------|
| 1 Flat walnut panels | 3 Travertine field | 5 Travertine plinth |
| 2 Walnut slats | 4 Linear fireplace | 6 LED lines above and below |

MATERIAL STUDY — CROPPED FROM THE VISUALISATIONS




WD-01 Walnut slats



ST-01 Travertine



UP-01 Boucle

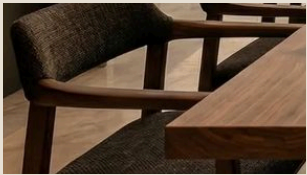

UP-02 Charcoal weave

Codes are portfolio references; products and suppliers to specify.

06 The burgundy salon

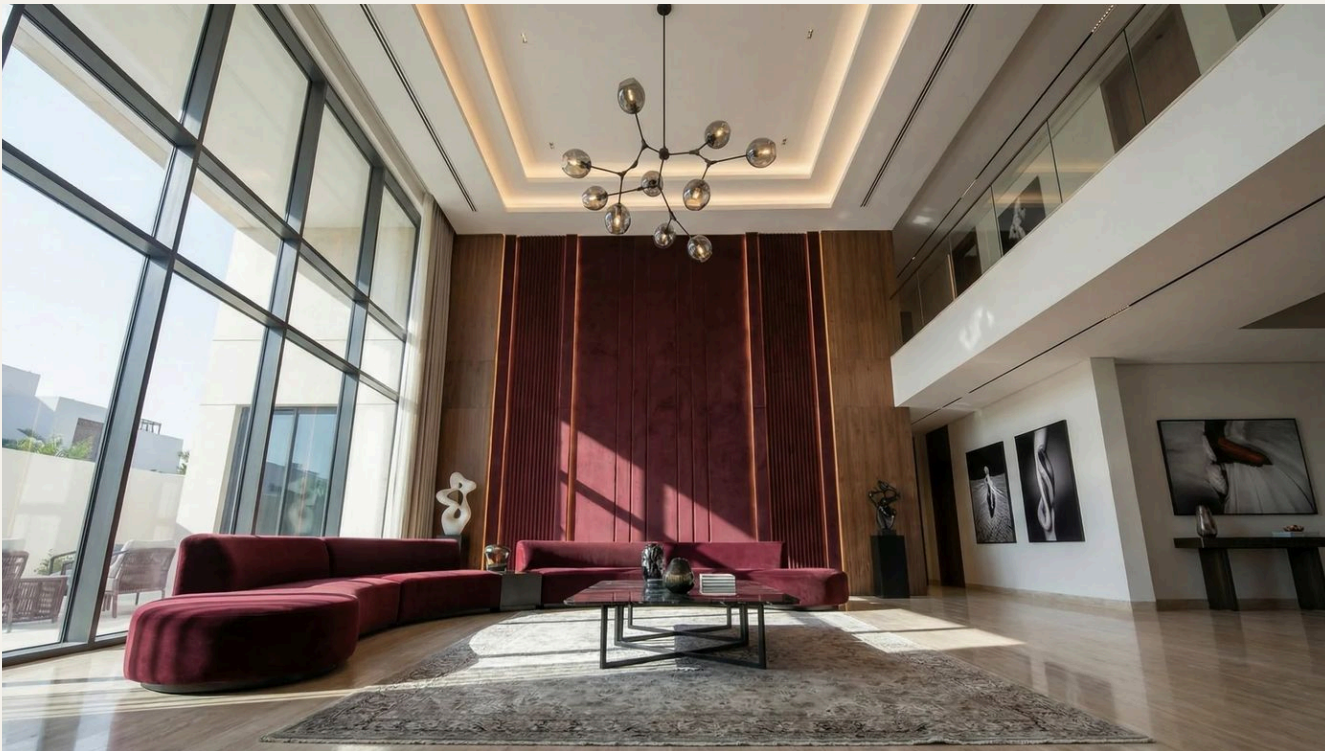


Fig. 01 Double-height salon with a curved burgundy sofa, full-height glazing and a burgundy feature wall.

CATEGORY
Residential — Living


LOCATION
To confirm

YEAR
To confirm

ROLE
To confirm

SCOPE
To confirm

A double-height salon defined by burgundy seating, tall windows and fine architectural detailing.

 


Velvet
#3E1C1C




Walnut
#64432B



Timber floor
#A69E93

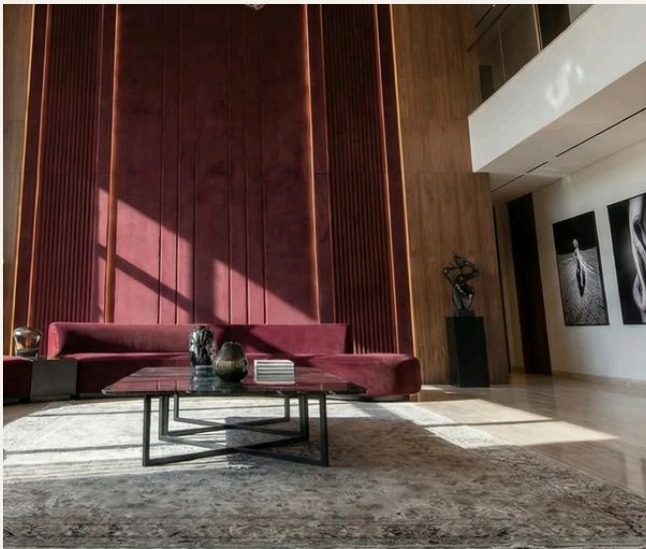


A Pleated velvet between walnut flanks — Fig. 01

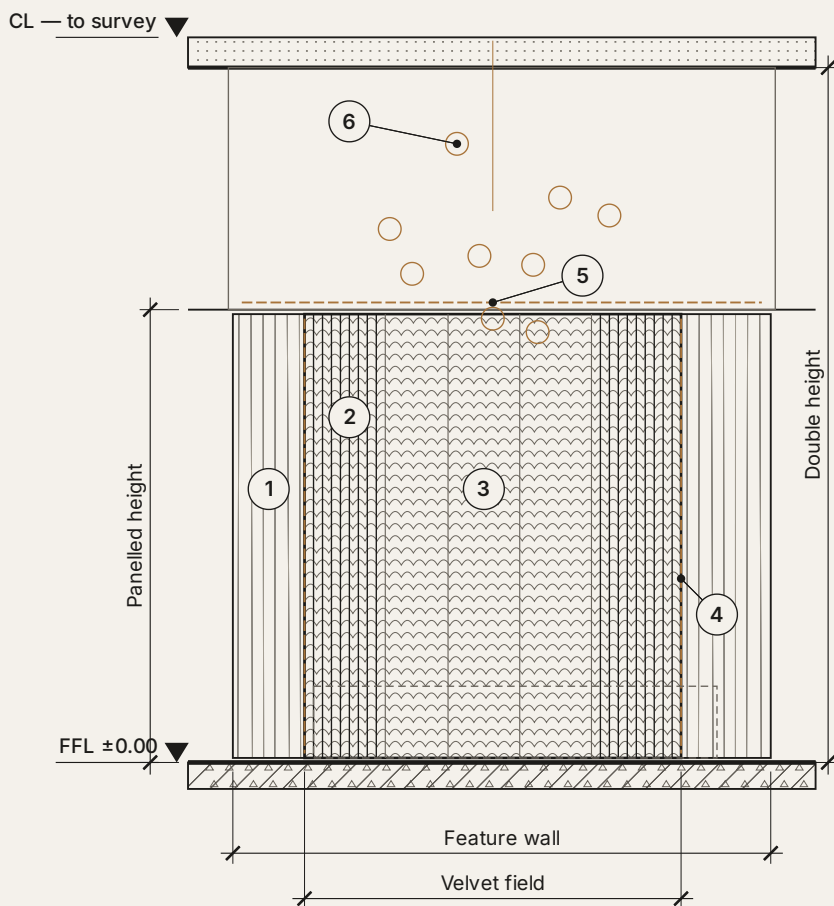

KEYNOTES

- 1 Walnut flank
- 2 Pleated velvet
- 3 Flat velvet field
- 4 Lit reveals
- 5 Ceiling cove
- 6 Glass pendant

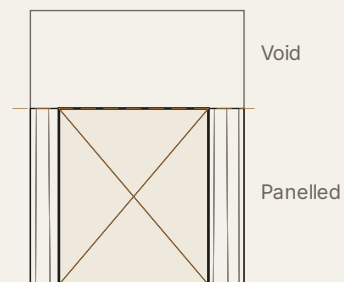

The velvet field rises through the panelled height beneath a double-height void. Read from Fig. 01; not measured.

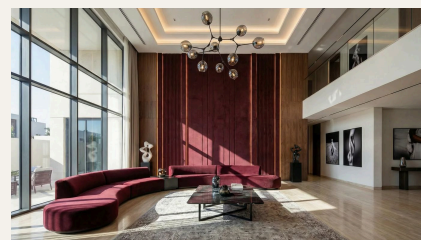


Fig. 02 Pendant and gallery level



FEATURE WALL

NTS · DESIGN DEVELOPMENT · FIG. 01



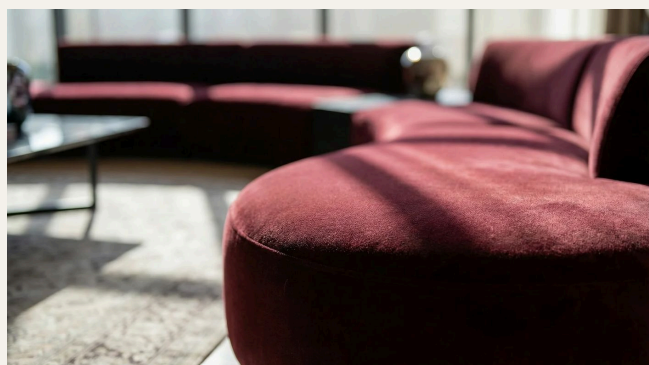


Fig. 03 Burgundy velvet seating in afternoon light.

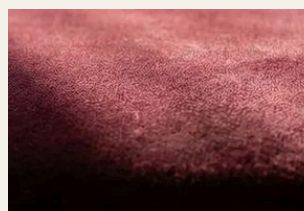

UP-01 Velvet

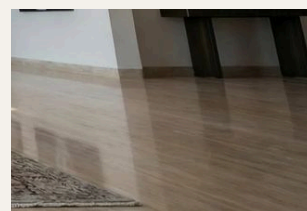

WD-01 Timber floor

COVE

Continuous light in the stepped ceiling

REVEALS

Light lines between velvet and walnut

DIAGRAM DD-B1 is traced from the proportions of Fig. 01; heights are named, not measured.



SELECTED WORKS — 07 / 07

Fig. 01 Majlis with low perimeter seating, a patterned frieze and a softly lit plaster feature wall.

07 An earthy welcome

Soft neutral seating, warm timber and patterned walls create a generous space for gathering.

THE FIRST VIEW — AS VISUALISED

- 1 Lit plaster feature wall on the axis
- 2 Light oak wall cladding
- 3 Patterned frieze band
- 4 Low seating on a plinth
- 5 Cove light in the ceiling tray

CATEGORY	Residential — Majlis
LOCATION	To confirm
YEAR	To confirm
ROLE	To confirm
SCOPE	To confirm

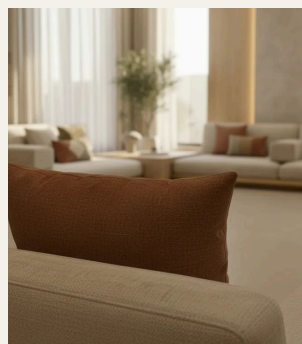


Fig. 02 Terracotta, frieze


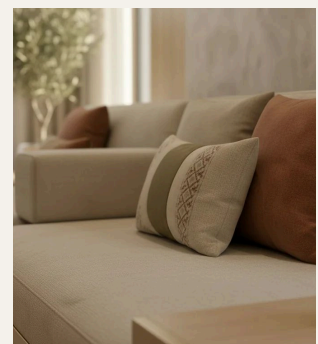


Fig. 05 Woven cushions

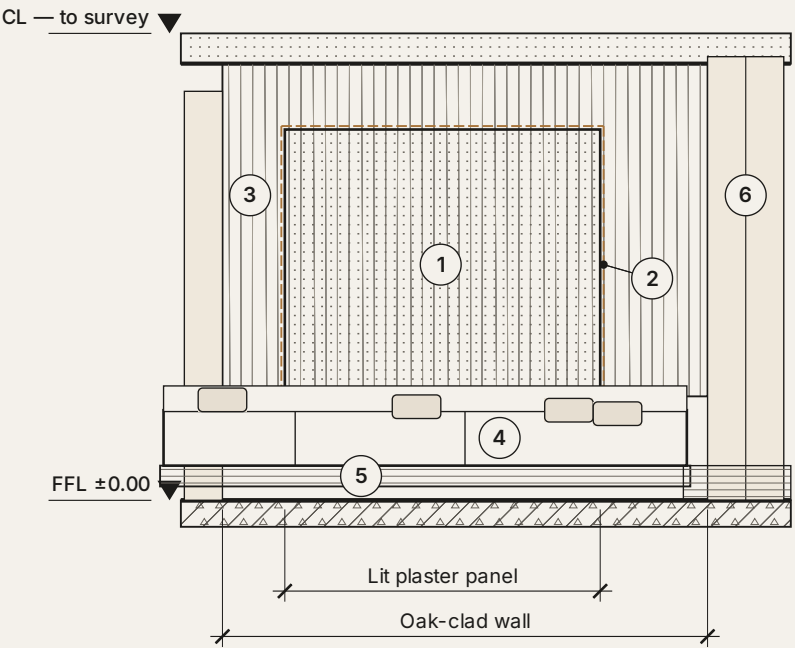

DD-M1 · KEYNOTES

- 1 Textured plaster panel
- 2 Concealed light around it
- 3 Light oak cladding
- 4 Low seating, cushions
- 5 Oak plinth
- 6 Window with sheers

DIAGRAM Traced from the proportions of Fig. 01; sizes to survey.


E1
DD-M1
FEATURE WALL

NTS · DESIGN DEVELOPMENT · FIG. 01




Fig. 03 Lit timber shelving and ceramics beside the frieze.

ELEVATION

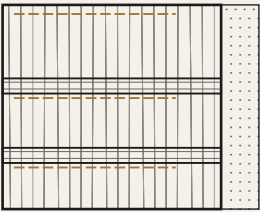

SECTION

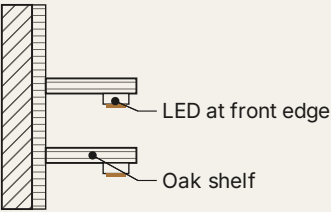

01
CD-M1

LIT OAK SHELF

NTS · CONCEPT DETAIL · FIG. 03

MATERIAL STUDY — FRIEZE MOTIF TRACED FROM FIGS. 01 + 03



Vector trace: stepped diamonds between two borders of small diamonds. Right: the frieze as visualised.




Plaster	Light oak	Terracotta	Linen	Frieze	Stone floor
#9D8A70	#AA8F70	#7B4E2F	#AA977D	#87644A	#C2BAB1

Drawn to be *built*.

Managing interior projects end to end — concept and design development, technical drawings, material selection, BOQ preparation, pricing, supplier and contractor coordination, and final execution on site.

REPRESENTATIVE EXAMPLES The drawings on pages 38–39 were prepared for this portfolio to show drawing standards. They are not construction documents of a specific project; real project documents will be added when supplied.

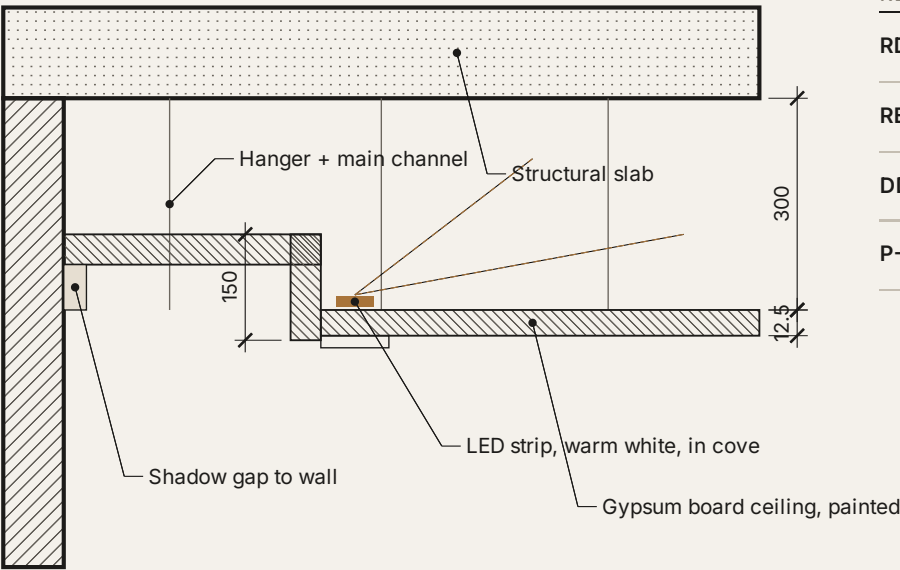

REF	DRAWING REGISTER
RD-02	Ceiling section — representative
RE-02	Wardrobe — shop drawing format
DD · CD	Project studies, pp. 09–37
P—	Project documents — to be supplied



LIGHTING COVE — CEILING SECTION

1 : 10 · REPRESENTATIVE DETAIL · TYPICAL SIZES

DRAWING CONVENTIONS

LINE WEIGHTS

—	Cut · 0.55 mm
—	Heavy · 0.35 mm
—	Medium · 0.25 mm
—	Fine · 0.15 mm

HATCHES

	Masonry / wall
	Concrete / gypsum
	Timber / board
	Upholstery
	Stone / marble


SYMBOLS

	Elevation / section
	Grid reference
	Finish / note key

DIMENSIONING

	1 200
	mm, to finished faces
	CH = clear ceiling height
	NTS = not to scale

PROJECT	SHEET TITLE	DWG NO.	STATUS	SCALE	ISSUE
Representative set	Ceiling section · conventions	RD-02	Representative detail	1:10 typ.	2026–27

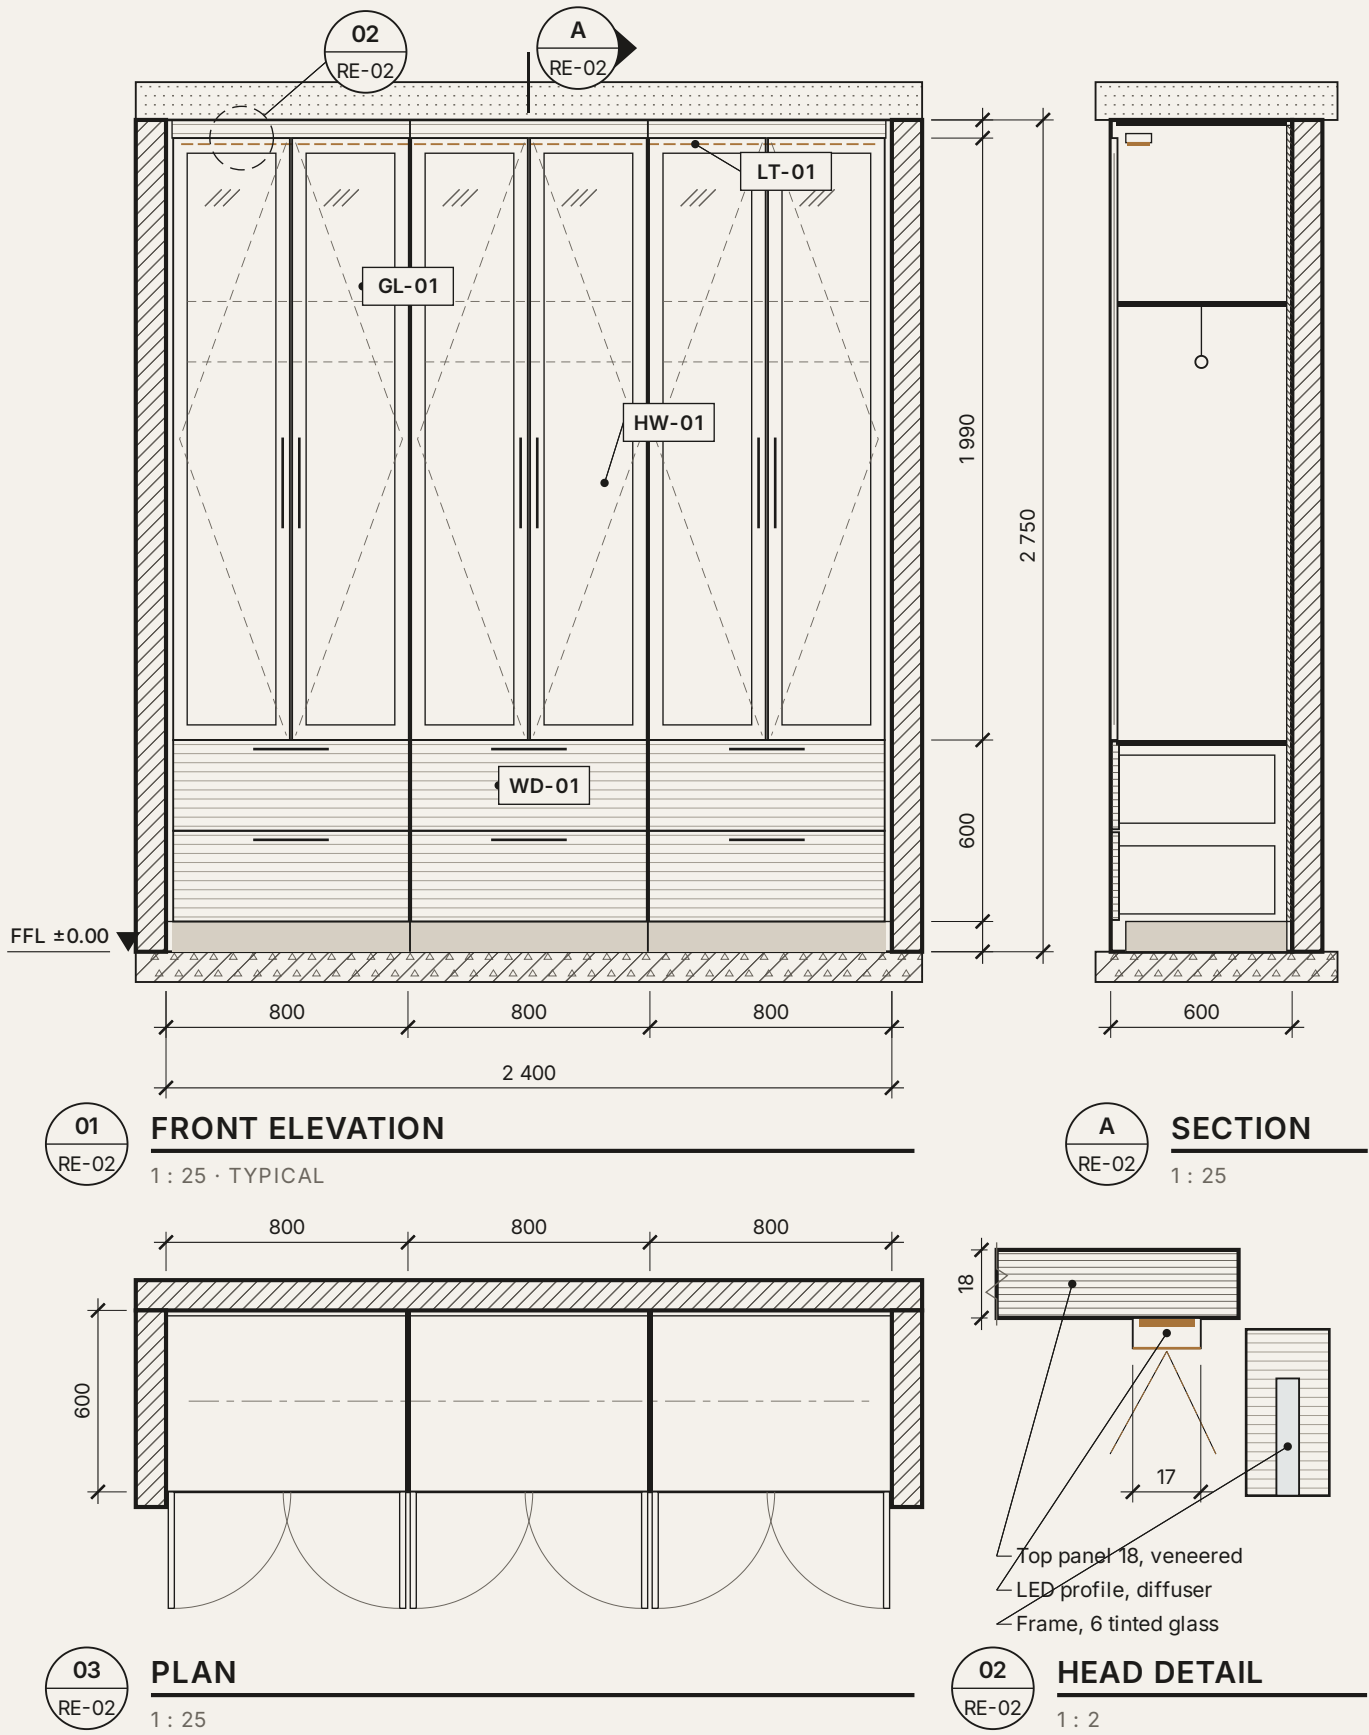

PROJECT	SHEET TITLE	DWG NO.	STATUS	SCALE	ISSUE
Typical wardrobe	Wardrobe – shop drawing	RE-02	Representative example	1:25 / 1:2	2026–27

Professional *experience*

ROLE · RIYADH, SAUDI ARABIA

Senior Interior Designer · Interior Architect · Project Coordinator

Managing and developing interior design projects from concept through execution and final handover.

CAREER RECORD — EMPLOYERS, POSITIONS AND DATES TO BE ADDED

POSITION	EMPLOYER / STUDIO	LOCATION	YEARS
To confirm	To confirm	To confirm	To confirm
To confirm	To confirm	To confirm	To confirm
To confirm	To confirm	To confirm	To confirm

DESIGN

Developing creative, functional interior concepts. Space planning and furniture layouts. Mood boards; selecting materials, finishes, colours and furniture. Luxury residential interiors — feature walls, entrances, ceilings, partitions, custom furniture.

TECHNICAL

Technical drawings and shop-drawing coordination for execution. BOQs, quantity take-offs and cost estimations. Pricing interior works; quotations with suppliers and subcontractors.

COORDINATION

Coordinating carpentry workshops, steel fabricators, stone and glass suppliers. Reviewing samples against project specifications. Coordinating clients, contractors, suppliers, factories and site teams.

EXECUTION

Following up execution; resolving technical and design issues. Site inspections and quality control. Managing detail from design approval to final handover.

INTERNATIONAL EXPERIENCE

Saudi Arabia
Qatar
United Arab Emirates
Lebanon

RESIDENTIAL

Luxury villas · apartments · living rooms · majlis & reception · TV feature walls · entrance & foyer · bedrooms · staircases · decorative ceilings · custom furniture

COMMERCIAL

Offices · retail spaces · showrooms · commercial and hospitality interiors · custom joinery packages

Let's create *spaces* that last.

EMAIL info@alaamasri.com

PHONE +966 57 053 3358

WHATSAPP +966 57 053 3358


ONLINE alaamasri.com

BASED IN Riyadh, Saudi Arabia

SELECTED WORKS — INDEX

01	An arched retreat	09
02	The skyline suite	15
03	The walnut suite	20
04-07	Villa · garden · salon · majlis	26
—	Technical capability	38

For private clients, developers, contractors, consultants and design studios — project enquiries, collaborations and professional opportunities.

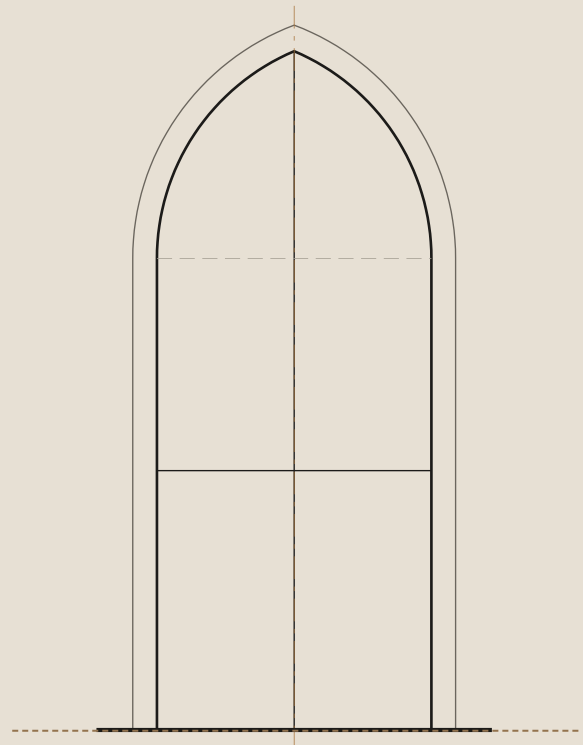

ARCHED OPENING · DD DIAGRAM



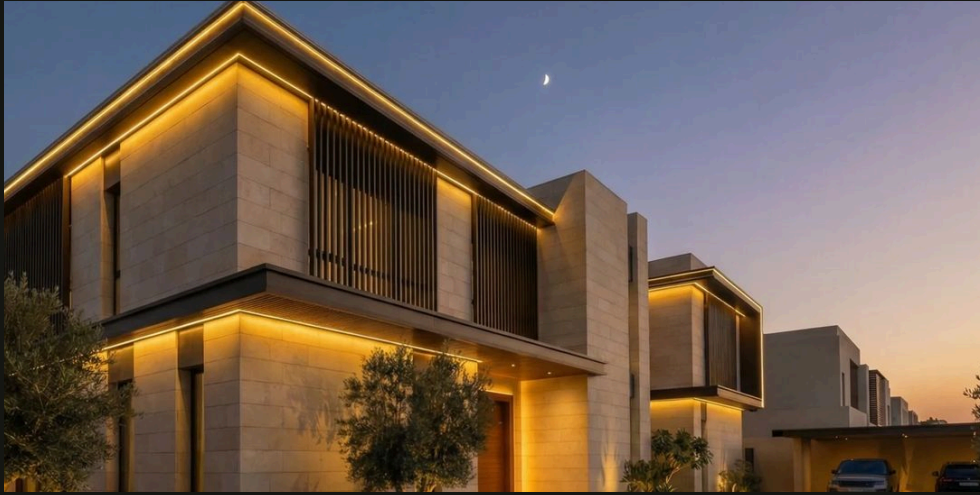


Fig. 02 The illuminated villa at dusk

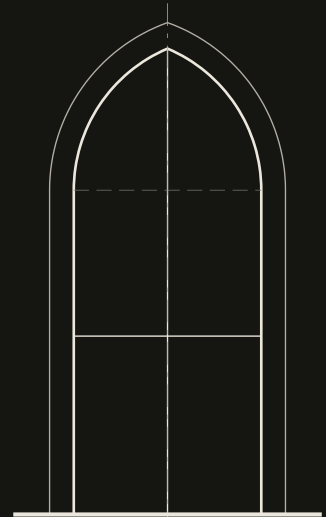

ARCHED OPENING
DD DIAGRAM

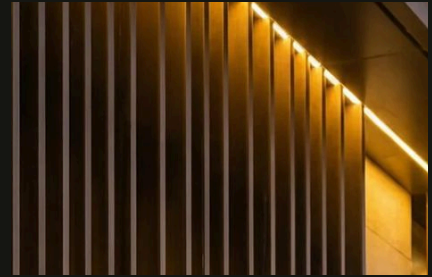

ARCH · JOINERY · FACADE — DETAILS FROM THE SELECTED WORKS

Alaa Masri

INTERIOR DESIGNER · INTERIOR ARCHITECT
PORTFOLIO 2026-2027