


Alaa

AN ARCHED RETREAT — GUEST ROOM
ELEVATION STUDY · VISUALISATION



DESIGN DEVELOPMENT
DIAGRAM · OPENING

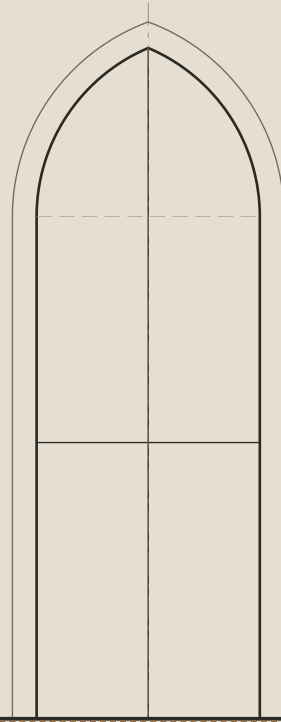

VISUALISATION
FIG. 07

Masri

Interior design and interior architecture — from the first concept to the final handover.

Design. Technical development. Execution.

PRACTICE

15+

years in interior design, interior architecture, fit-out and project coordination

COUNTRIES

4

Saudi Arabia · Qatar · United Arab Emirates · Lebanon

SELECTED WORKS

7


residential, hospitality and architectural projects in this book

STUDIES


30+

drawings, details and material studies prepared for this portfolio


FOUR DISCIPLINES — DETAILS FROM THE SELECTED WORKS

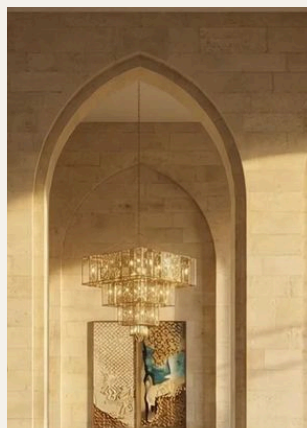

Architecture The arch as a system — An arched retreat

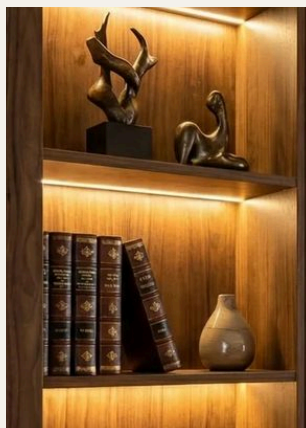

Joinery Walnut, stone and light — The walnut suite

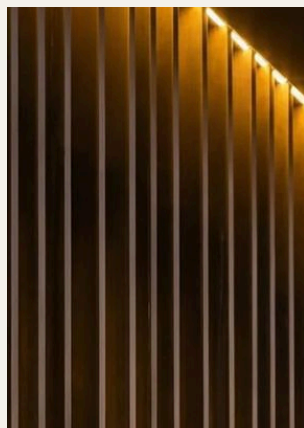

Facade Screens and linear light — The illuminated villa



Material Travertine and fire — Living by the garden

BASED IN

Riyadh, Saudi Arabia

EMAIL

info@alaamasri.com

PHONE

+966 57 053 3358 · WhatsApp

ONLINE

alaamasri.com

Each project is shown through its visualisations and through studies drawn from them — the way it would be explained in a design review.

Contents

ALAA MASRI
INTERIOR DESIGNER
INTERIOR ARCHITECT

Profile	04
Expertise	06
Selected works	08
01 An arched retreat	09
02 The skyline suite	15
03 The walnut suite	20
04 The illuminated villa	26
05 Living by the garden	30
06 The burgundy salon	34
07 An earthy welcome	36
Technical capability	38
Experience	40
Contact	41

HOW TO READ THE DRAWINGS

The studies in this book were drawn for this portfolio to explain each design. They read the visualisations — they are not surveys, approved drawings or construction documents. Every sheet carries one of these labels in its title block.

REF	LABEL	WHAT IT CLAIMS
DD	Design development diagram · space / section / massing study	Proportions read from the named render; dimensions named, not measured
CD	Concept detail	How the junction seen in a render could be built
RD · RE	Representative detail · example	Generic, typical sizes, tied to no project
MS	Material study	Swatches cropped from renders, colours sampled; products to specify

PROFILE

Imagination.

With the knowledge to make it real.


Interior design and interior architecture — from the first concept to the final handover.

Design. Technical development. Execution.

ALAA MASRI · RIYADH, SAUDI ARABIA



SELECTED WORK

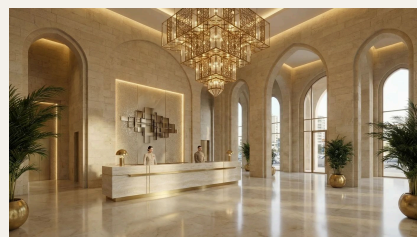

01 An arched retreat · p. 09



03 The walnut suite · p. 20



04 The illuminated villa · p. 26

Seven projects · pages 09–37

I’m Alaa Masri, a Lebanese interior designer and interior architect based in Riyadh. Over 15 years of practice across the Gulf and Lebanon have shaped my approach to space.

I work from the first concept through to final handover, connecting design, materials and craftsmanship with the precision that execution demands.

My work spans luxury residential, hospitality, commercial and retail interiors — coordinating clients, consultants, contractors, workshops, factories and site teams so that the design holds from drawing to site.


15+

years in interior design, interior architecture, fit-out and project coordination.

PRACTICE ACROSS	SECTORS	EDUCATION	LANGUAGES
Saudi Arabia Qatar United Arab Emirates Lebanon	Residential · commercial · hospitality · retail	BT — Interior Decoration / Interior Design, Lebanon · TS studies, Interior Design	Arabic — native English — professional working proficiency

DESIGN TOOLKIT	BEYOND THE DRAWING BOARD
AutoCAD · 3ds Max · V-Ray · Chaos Vantage · Blender · Photoshop · Illustrator	AI-assisted design & visualization · Figma · Design presentation

CONCEPT TO HANDOVER — HOW A PROJECT IS CARRIED

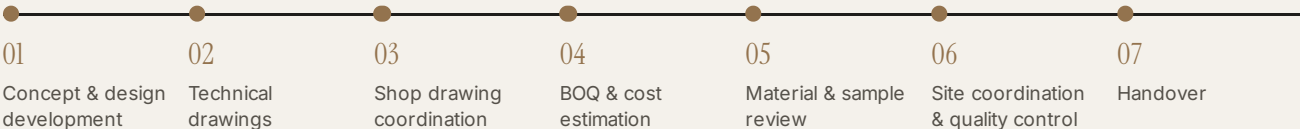

Steps condensed from the professional profile: concept and design development, technical drawings, material selection, BOQ preparation and pricing, supplier and contractor coordination, execution on site.


Every space. Every detail.

From the first sketch to the final handover — design authorship backed by the technical and site knowledge to deliver it.

01 Interior design

Creative, functional concepts for luxury residential, commercial and retail interiors — planned around the way each space will be lived in and used.

Space planning & furniture layouts · Concept design & mood boards · Material & finish selection · Furniture design & custom joinery

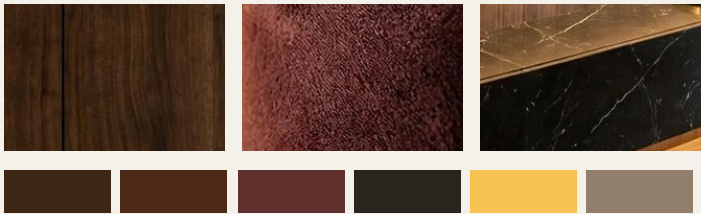


CONCEPT & MATERIAL STUDY

02 Interior architecture

The architectural elements of the interior — entrances, ceilings, partitions and feature walls — designed as one coherent whole.

Entrance & foyer design · Decorative ceilings · Feature walls & partitions · Staircase areas

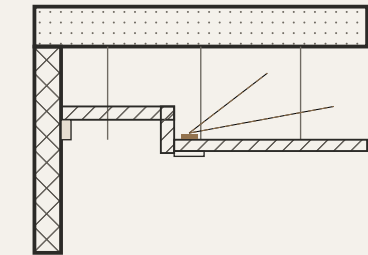


Bulkhead, lighting cove and shadow gap to the wall

REPRESENTATIVE SECTION

03 Technical & shop drawings

Preparing technical drawings and coordinating shop drawings so that the design can be built exactly as intended.

Technical drawings · Shop drawing coordination · Construction & execution details

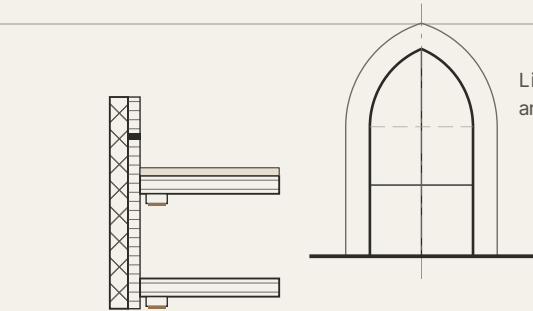

Lit shelf section · arched opening

REPRESENTATIVE DETAIL

04 BOQ & cost estimation

Bills of quantities, take-offs and cost estimates, with interior works priced and quotations coordinated with suppliers and subcontractors.

BOQ & quantity take-off · Cost estimation & pricing · Supplier quotations

REF	ITEM	UNIT	QTY	RATE
1.01	Gypsum ceiling with lighting cove	m ²	48.0	—
1.02	Veneer wall panelling on battens	m ²	22.5	—
1.03	Built-in wardrobe, glass doors, LED	m	4.8	—

BOQ FORMAT · SAMPLE VALUES

05 Fit-out & coordination

Coordinating clients, contractors, suppliers, factories and site teams, and reviewing material samples against the project specifications.

Joinery & woodwork · Stone, marble & glass · Steel & metal fabrication · Lighting coordination



COORDINATION — FROM THE PROFILE

06 Site supervision

Following execution on site, resolving technical and design issues and maintaining quality from design approval through to final handover.

Site inspections · Quality control · Handover


- ☒ Material samples reviewed against specification
- ☒ Shop drawings coordinated for execution
- ☒ Site inspection — quality standards
- ☒ Technical and design issues resolved
- ☒ Detail managed through to handover

REPRESENTATIVE CHECKLIST FORMAT

07 3D visualization

Concepts made tangible through 3D modeling, rendering and design presentation — exploring proportion, light and texture before execution begins.

3ds Max · V-Ray · Chaos Vantage · Blender · Design presentation

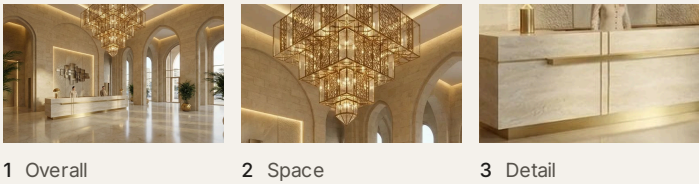

1 Overall 2 Space 3 Detail

FROM RENDER TO DETAIL — AN ARCHED RETREAT, FIG. 01

TOOLKIT

AutoCAD · 3ds Max · V-Ray · Chaos Vantage · Blender · Photoshop · Illustrator · Figma

TYPICAL DELIVERABLES

Concept and mood boards · space planning and furniture layouts · technical and shop drawings · BOQs and cost estimates · material selections · 3D visualisation

REPRESENTATIVE FORMATS

The small drawings, tables and checklists on this spread were prepared for this portfolio to show working method. Project renders are Alaa Masri’s visualisations.

Selected *works*

A closer look. *Seven design stories — each told through its own strengths.*

01	An arched retreat	HOSPITALITY — DESIGN STUDY	09
02	The skyline suite	RESIDENTIAL — BEDROOM	15
03	The walnut suite	RESIDENTIAL — BEDROOM	20
04	The illuminated villa	ARCHITECTURE — EXTERIOR	26
05	Living by the garden	RESIDENTIAL — LIVING	30
06	The burgundy salon	RESIDENTIAL — LIVING	34
07	An earthy welcome	RESIDENTIAL — MAJLIS	36



01 p. 09



02 p. 15



03 p. 20



04 p. 26



05 p. 30



06 p. 34



07 p. 36


Locations, years, roles, scope and project status are marked "To confirm" until verified.




SELECTED WORKS — 01 / 07

Fig. 01 Arched reception hall with a stone-clad counter, gold chandelier and polished marble floor.


01 An arched *retreat*

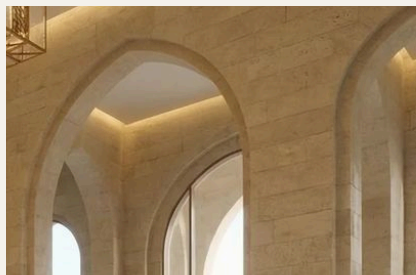

A Arched glazing, reception — Fig. 01

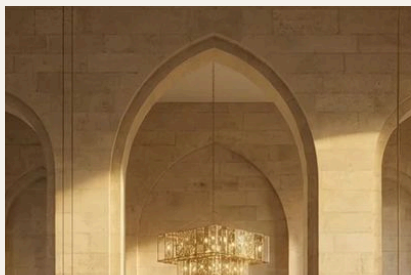

B Pointed arcade, dining — Fig. 03

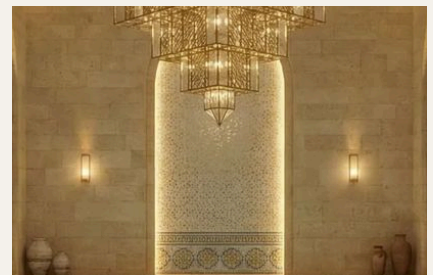

C Lit mosaic niche, pool — Fig. 05

CATEGORY

Hospitality — Design study

LOCATION

To confirm

YEAR

To confirm

ROLE

To confirm

SCOPE

To confirm

CONCEPT

A hospitality design study connecting vaulted interiors, dining spaces, guest accommodation and quiet leisure areas.



Limestone
#957953 · Fig. 01



Marble floor
#AC9B80 · Fig. 01



Gold metalwork
#916733 · Fig. 01




Lit mosaic
#998661 · Fig. 05

The arch as a system — *pier, opening, light.*



Fig. 03 All-day dining space with timber tables, a central bar and arched stone walls.

KEY ELEMENTS — AS VISUALISED	
01	Pointed stone arches and arcades
02	Stone piers and columns
03	Integrated cove lighting
04	Gold chandeliers
05	Polished marble floors

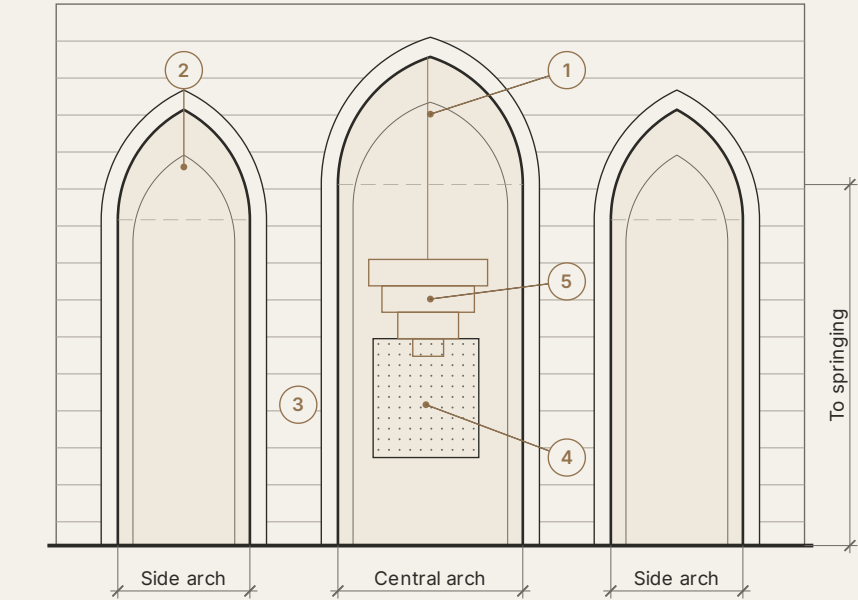

DD-A1 · KEY	
1	Central pointed arch, framing the end wall
2	Side arches, lower springing
3	Stone piers with coursed joints
4	Artwork panel on the axis
5	Gold chandelier on the axis

DESIGN DEVELOPMENT DIAGRAM

Traced from the proportions of Fig. 03 to show the arcade rhythm. Not a survey: arch sizes are named, not measured.

AN ARCHED RETREAT · TRACED FROM FIG. 03	
Dining — end wall, arcade elevation	
DESIGN DEVELOPMENT DIAGRAM	DD-A1 · NTS

THE SAME RHYTHM, ROOM BY ROOM

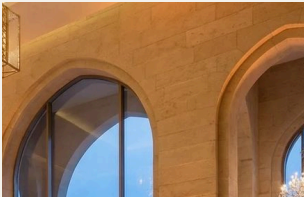


Fig. 04 Banquet hall windows

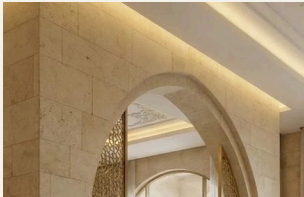




Fig. 02 Guest suite arches



Fig. 05 Pool arcade



Fig. 06 Rooftop loggia

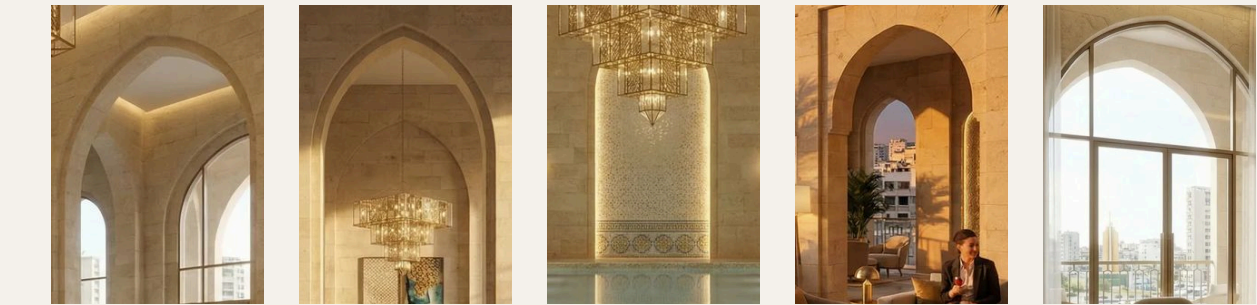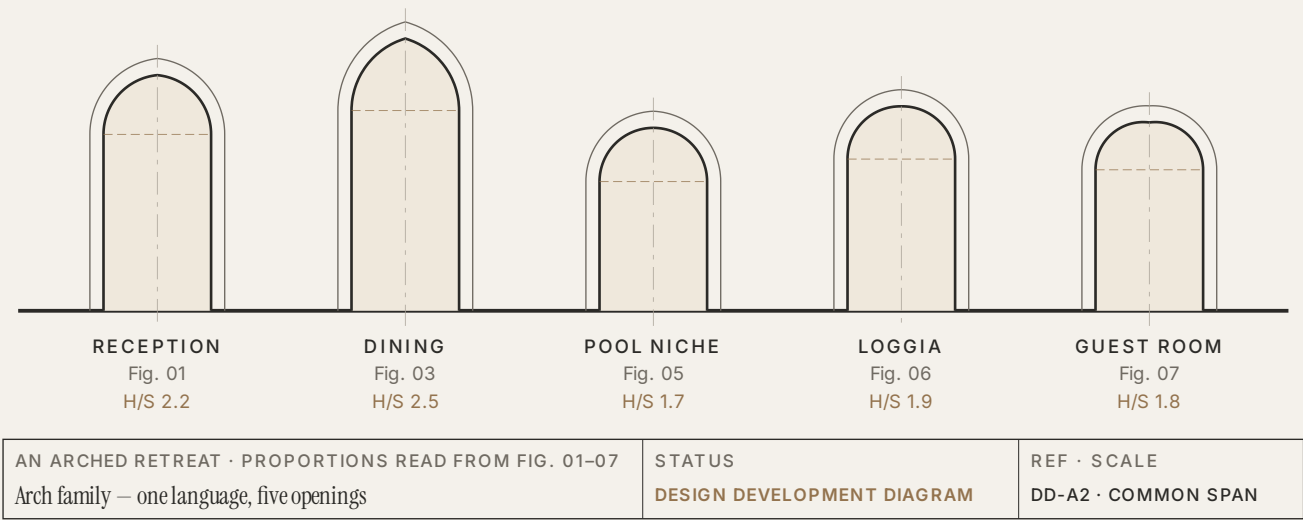

Above: each opening drawn to one span. Below: the same opening as visualised. H/S compares overall height to span, read from the renders with their perspective — a way of showing one arch language adapted to five rooms.



Fig. 02 Guest suite set beneath tall arches, with a lounge area and city views.

SPACES IN THE STUDY	
Reception hall	FIG. 01
Guest suite	FIG. 02
All-day dining	FIG. 03
Banquet hall	FIG. 04
Indoor pool	FIG. 05
Rooftop lounge	FIG. 06
Guest bedroom	FIG. 07

OPENING Pointed arches in public rooms, rounded niches at the pool, arched glazing in the guest rooms	PIER Coursed limestone piers and columns carry the rhythm from room to room	LIGHT Cove light at the ceiling, lit niches and reveals, chandeliers on the axis
---	---	--


Design intent — to confirm, in Alaa's words.



01 — AN ARCHED RETREAT

Fig. 05 Indoor pool framed by illuminated arched niches and stone columns.

Light as material — *the pool hall.*

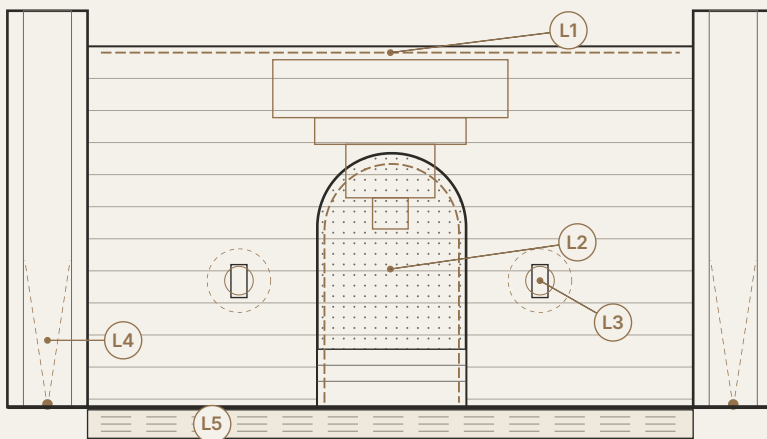

LIGHTING LAYERS — AS VISUALISED

- L1** Continuous cove light around the ceiling tray
- L2** Back-lit mosaic niche on the axis
- L3** Wall sconces either side
- L4** Up-light washing each stone pier
- L5** Underwater light in the pool

DESIGN DEVELOPMENT DIAGRAM

DD-A3 is traced from Fig. 05. It reads the lighting visible in the render; it is not a lighting design.


AN ARCHED RETREAT · TRACED FROM FIG. 05

Pool hall — back wall and lighting layers


DESIGN DEVELOPMENT DIAGRAM

DD-A3 · NTS


LIGHTING DETAILS, ENLARGED

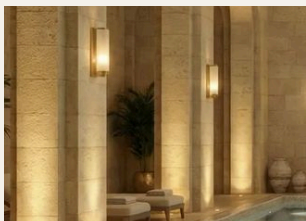


L4 Pier up-light

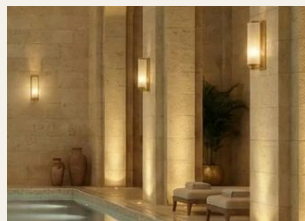

L3 Wall sconce

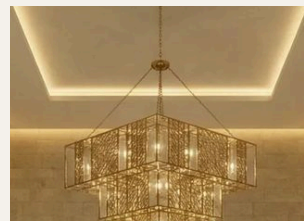

L1 Cove and chandelier

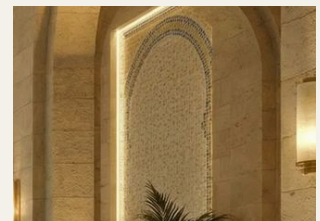


L2 Lit niche, side bay



Fig. 04 Banquet hall laid for an event beneath chandeliers and tall arched windows at dusk.



Fig. 06 Rooftop lounge beneath an arched loggia, overlooking the city skyline at sunset.

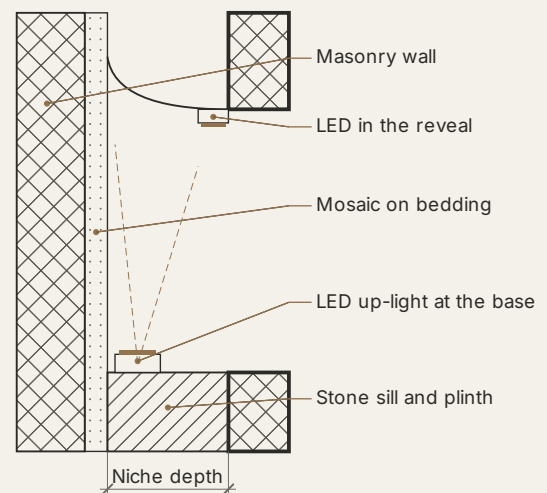

CONCEPT DETAIL

CD-A1 suggests how a lit niche like the one in Fig. 05 could be built: a stone reveal, a mosaic back and concealed light at the base and perimeter. Sizes to be confirmed.

AN ARCHED RETREAT · READS FIG. 05

Lit arched niche – section

CONCEPT DETAIL

CD-A1 · NTS

GOLD METALWORK — THREE CHANDELERS, ONE FAMILY

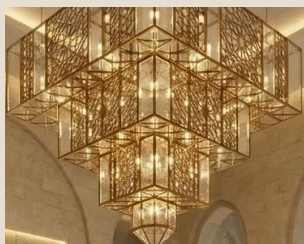


Fig. 01 Reception

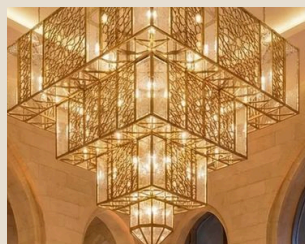


Fig. 04 Banquet hall



Fig. 06 Rooftop lounge




Gold metalwork
#916733 · Fig. 01




Fig. 07 Guest bedroom with arched windows, a stone feature wall and integrated cove lighting.


MATERIAL STUDY — CROPPED FROM THE RENDERS

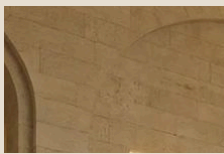


Limestone
Walls, arches · Fig. 01

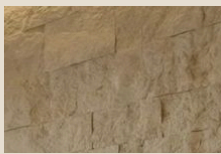


Split-face stone
Feature wall · Fig. 07

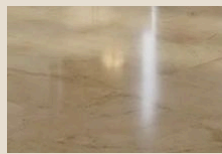


Polished marble
Floors · Fig. 01

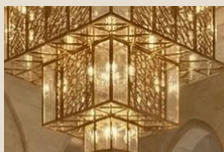

Gold metalwork
Chandeliers · Fig. 01

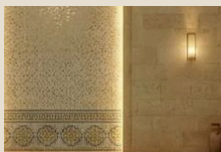

Mosaic
Pool niche · Fig. 05

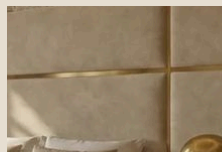

Upholstery
Headboard · Fig. 07

COLOUR — SAMPLED FROM THE RENDERS



Limestone
#957953 · Fig. 01



Polished marble floor
#AC9B80 · Fig. 01



Gold metalwork
#916733 · Fig. 01



Lit mosaic niche
#998661 · Fig. 05

FINISH CODES — MATERIAL STUDY, NOT A SPECIFICATION

- ST-01** Limestone — walls, arches, piers
- ST-02** Split-face stone — guest room feature wall
- ST-03** Polished marble — floors

- MT-01** Gold metalwork — chandeliers, planters
- MO-01** Mosaic — pool niche and pool edge
- LT-01** Integrated cove and niche lighting

Swatches are cropped pixels of the renders; colours are median values sampled from named regions. Products and suppliers: to specify.



SELECTED WORKS — 02 / 07

Fig. 01 Timber-lined bedroom with floor-to-ceiling windows overlooking a city skyline at night.

02 The skyline suite

CATEGORY

Residential — Bedroom

LOCATION

To confirm

YEAR

To confirm


ROLE

To confirm

SCOPE

To confirm

A timber-lined bedroom with skyline views, illuminated wardrobes and coordinated material details.

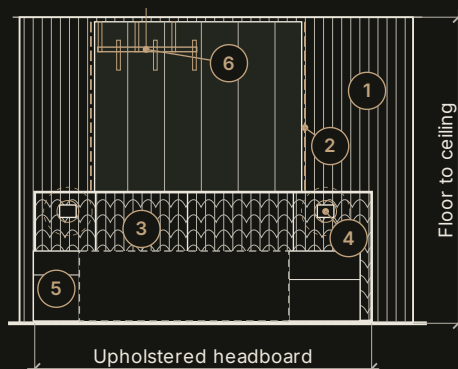

THE SKYLINE SUITE · TRACED FROM FIG. 01
Headboard wall — elevation

DESIGN DEVELOPMENT DIAGRAM

DD-S1 · NTS



- 1 Walnut panels
- 2 Lit recess
- 3 Headboard
- 4 Wall lights
- 5 Bedside
- 6 Pendant



02 — THE SKYLINE SUITE

Fig. 02 The bedroom looking towards the illuminated glass-fronted wardrobes.

Wood, fabric, leather — *warm tones.*

Bedroom, illuminated walk-in wardrobe and a coordinated palette of timber, fabric and leather.

MATERIAL PALETTE — CROPPED FROM THE PROJECT MATERIAL BOARD (FIG. 06), LABELS AS ON THE BOARD

Wall panelling Walnut, vertical grain	Flooring Dark oak hardwood	Headboard Taupe velvet	Bedding Beige linen	Curtains Gold-beige drapery	Rug Cream shag pile	Bench Dark brown leather	Accent pillow Woven brown leather

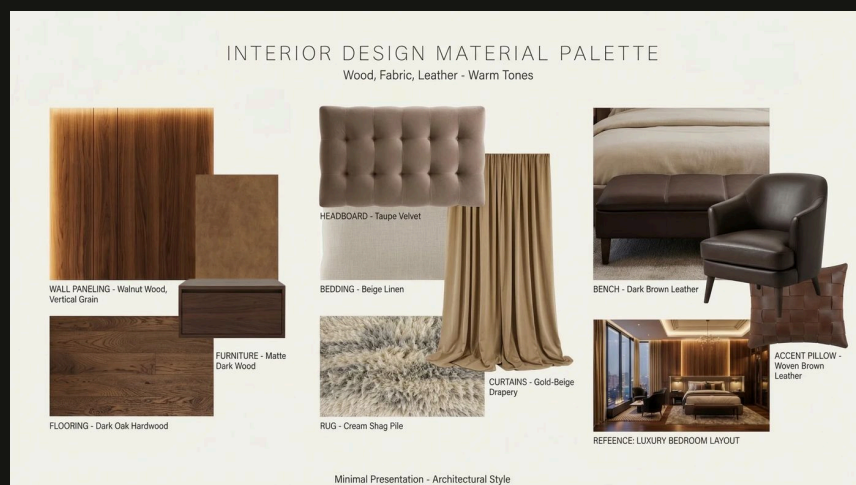


Fig. 06 Material palette board for the suite: wall panelling, flooring, bedding, curtains, rug and leather samples.


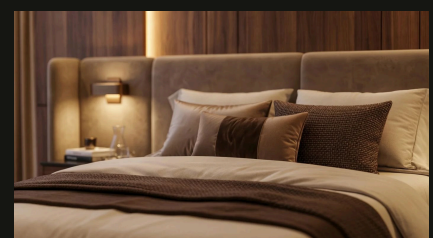


Fig. 03 Bed detail with layered linens and an upholstered headboard.

Walnut wall panelling #552D14	Taupe velvet headboard #533721



Fig. 04 Illuminated walk-in wardrobe with glass doors and walnut frames.

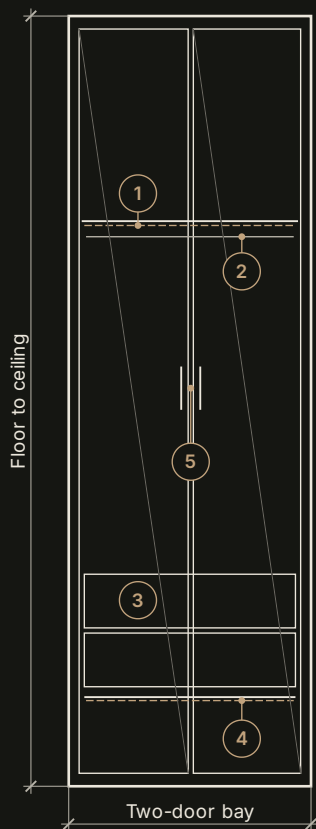

TRACED FROM FIG. 04
Wardrobe bay – elevation

DESIGN DEVELOPMENT DIAGRAM

DD-04 · NTS



One bay, from Fig. 04



Fig. 05 Brass and glass pendant light against timber panelling.

DD-04 · KEY

- 1 LED to the top shelf
- 2 Hanging rail
- 3 Drawers
- 4 Lit shoe display
- 5 Glass doors in walnut frames

DESIGN DEVELOPMENT DIAGRAM

DD-04 traced from the proportions of Fig. 04; not a shop drawing.


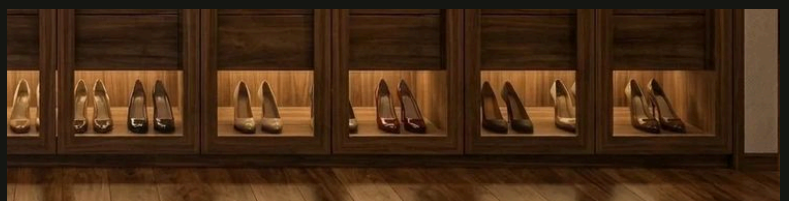


Fig. 04 Lit shoe display along the base of the wardrobe, enlarged

Sleep, lounge, dress — *one room, three zones.*

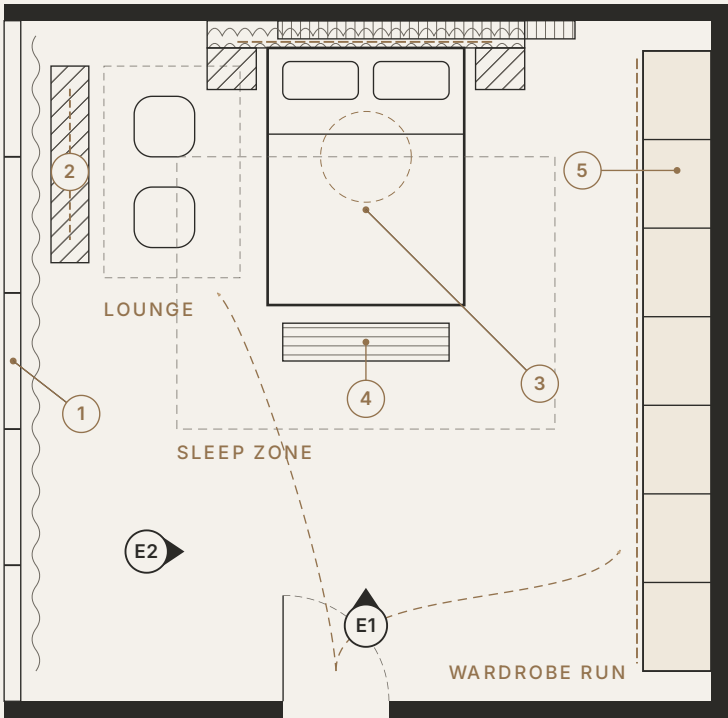

DD-S2 · KEY

- 1 Floor-to-ceiling glazing, skyline view
- 2 Linear fire feature by the window
- 3 Bed on the panelled headboard wall
- 4 Leather bench at the foot of the bed
- 5 Glass-fronted wardrobe run



E1 looking to the headboard — Fig. 01




E2 looking to the wardrobes — Fig. 02

READS FIG. 01 + 02 · NOT A SURVEYED PLAN

The skyline suite — layout reading

CONCEPTUAL SPACE STUDY

DD-S2 · NTS

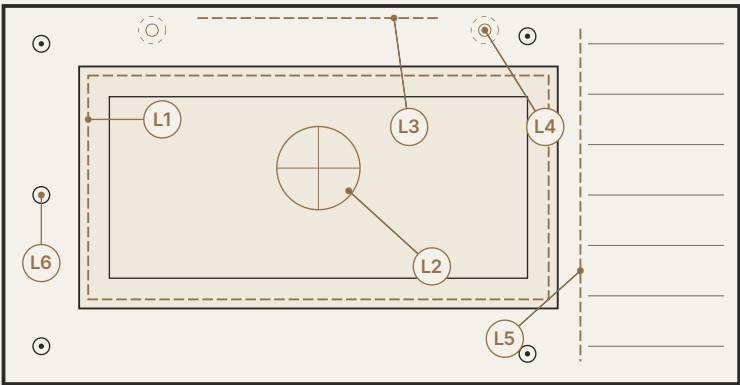

DD-S3 · LIGHTING LAYERS

- L1 Cove in the stepped ceiling tray
- L2 Brass and glass pendant — Fig. 05
- L3 Lit vertical recess, headboard wall
- L4 Wall lights either side of the bed
- L5 LED inside the wardrobes
- L6 Recessed downlights

THE SKYLINE SUITE · READS FIG. 01, 02, 04

Lighting layers — reflected ceiling reading

CONCEPTUAL SPACE STUDY

DD-S3 · NTS

CONCEPTUAL SPACE STUDY

DD-S2 and DD-S3 read the room from Fig. 01, 02 and 04 to show zoning and the layering of light. Not a survey or a lighting design: sizes, positions and fittings to be confirmed.



L2 Pendant — brass frame, glass rods · Fig. 05



L4 Wall lights on the upholstered headboard · Fig. 01



L1 · L3 Cove and lit panel reveals · Fig. 02



L5 Lit hanging bays behind glass · Fig. 04

MATERIAL STUDY — SAMPLED FROM THE VISUALISATIONS



Walnut wall panelling
#552D14 · Fig. 01



Taupe velvet headboard
#533721 · Fig. 01



Dark oak floor
#4D2711 · Fig. 01



Dark leather bench
#462D1B · Fig. 01

TIMBER

Walnut wall panelling, vertical grain; dark oak floor

FABRIC

Taupe velvet headboard, beige linen, gold-beige drapery

LEATHER

Dark brown bench, woven leather accent pillow

LIGHT

Cove, lit reveals, wall lights, wardrobe LED

PALETTE AND JOINERY, ONE SEQUENCE



Fig. 06 Board



Fig. 02 Wardrobe

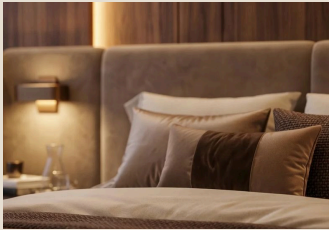


Fig. 03 Bed

Design intent — to confirm




SELECTED WORKS — 03 / 07

Fig. 01 Symmetrical bedroom with an upholstered burgundy headboard wall, walnut panelling and a glass pendant.


03 The walnut suite



A Headboard wall, lit reveals — Fig. 01

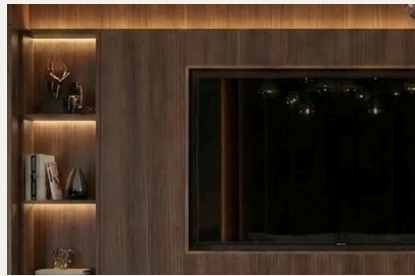

B Lit niche and media recess — Fig. 02

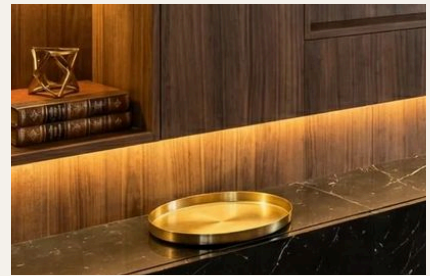

C Marble ledge and brass — Fig. 03

CATEGORY

Residential — Bedroom

LOCATION

To confirm

YEAR

To confirm

ROLE

To confirm

SCOPE

To confirm

CONCEPT

Rich walnut, burgundy accents and integrated lighting connect the bedroom and its bespoke joinery.



Walnut
#3E2615 · Fig. 03



Burgundy velvet
#5F302D · Fig. 05



Black marble
#28251F · Fig. 02



Brass
#F7C254 · Fig. 03



Beige linen
#917F6B · Fig. 01



Warm light
#E8A880 · Fig. 05



03 — THE WALNUT SUITE

Fig. 02 Opposite wall of the suite: a walnut media unit with lit shelving and a stone ledge.

Design language

Design intent — to confirm, in Alaa’s words.

KEY ELEMENTS — AS VISUALISED

- 01 Upholstered burgundy headboard wall
- 02 Walnut panelling and bespoke joinery
- 03 Integrated, concealed linear lighting
- 04 Lit display shelving and media recess
- 05 Black marble ledge and bedside surfaces

COLOUR — SAMPLED FROM THE VISUALISATIONS

		
Walnut veneer #3E2615 · Fig. 03	Walnut, lit #4D2A18 · Fig. 05	Burgundy velvet #5F302D · Fig. 05
		
Black marble #28251F · Fig. 02	Brass accent #F7C254 · Fig. 03	Beige linen #917F6B · Fig. 01

PALETTE

Walnut, burgundy velvet, black marble, brass

LIGHT

Concealed linear light in joinery, niches, reveals and ceiling

JOINERY

Walnut media unit with lit shelving and a stone ledge

ACCENT

Burgundy upholstered headboard wall and drapery

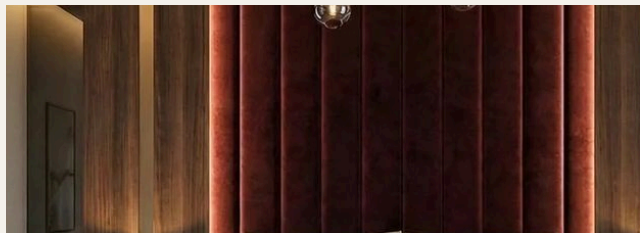


Fig. 01 Walnut panel and lit reveal, enlarged


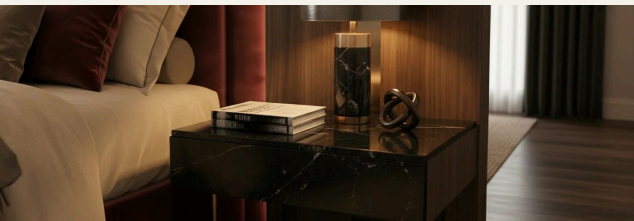


Fig. 04 Bedside: marble table, lamp, upholstered panels

Space study — *sleep zone, media wall, circulation.*

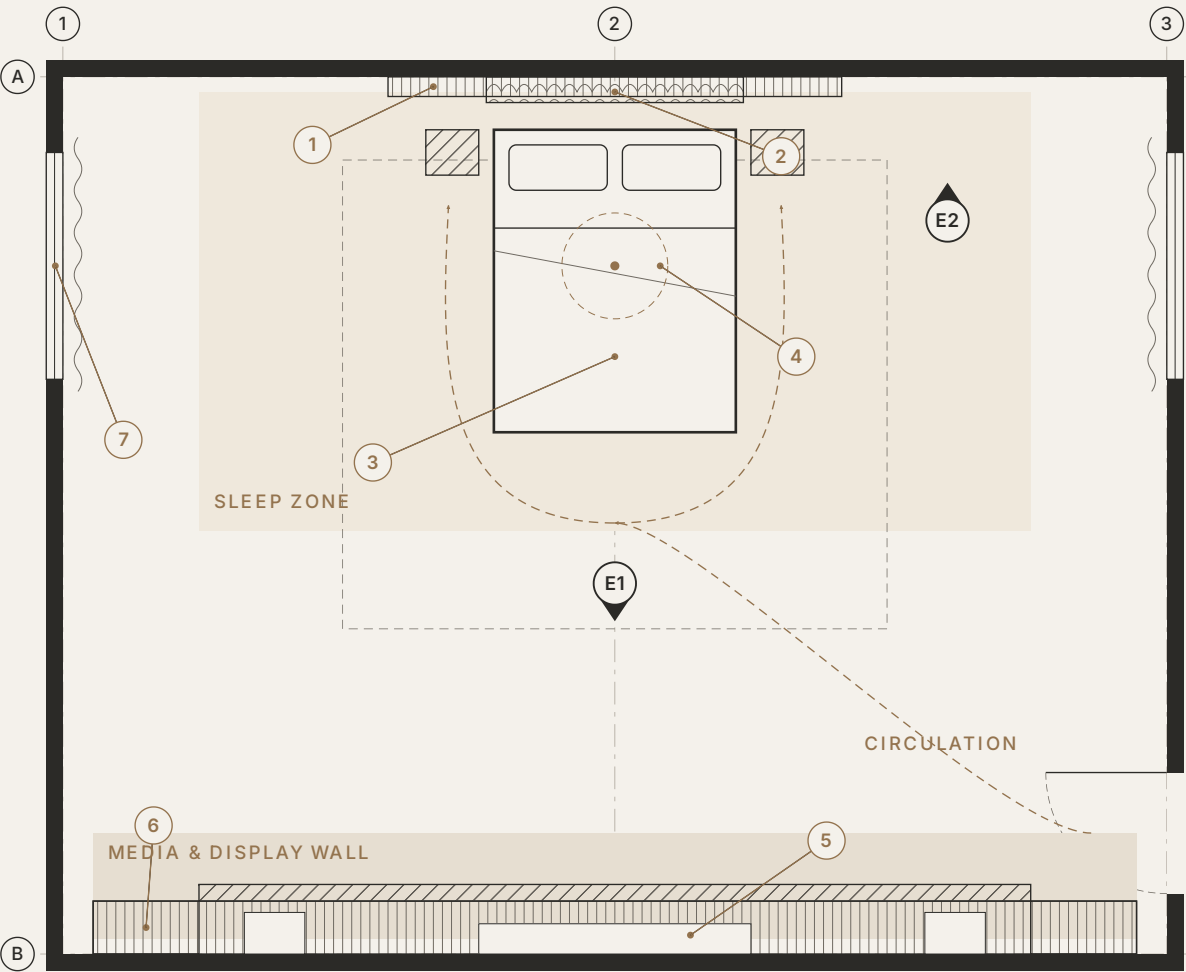


READS FIG. 01 + 02 · NOT A SURVEYED PLAN	STATUS	REF · SCALE
The walnut suite — layout reading	CONCEPTUAL SPACE STUDY	DD-01 · NTS

KEY

- 1 Headboard feature wall — walnut panels either side
- 2 Upholstered burgundy centre panel
- 3 Bed with bedside tables
- 4 Glass pendant cluster over the bed (ceiling)
- 5 Media wall joinery with stone ledge
- 6 Tall storage units
- 7 Window with full-height drapery




E1 to the media wall — Fig. 02

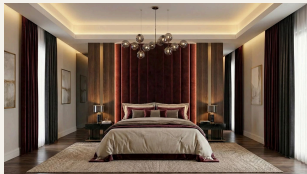

E2 to the headboard — Fig. 01

CONCEPTUAL SPACE STUDY

A reading of the room from the two visualised elevations, drawn to show zoning and circulation. Not a surveyed or approved plan: sizes, openings and orientation to be confirmed from the project drawings.

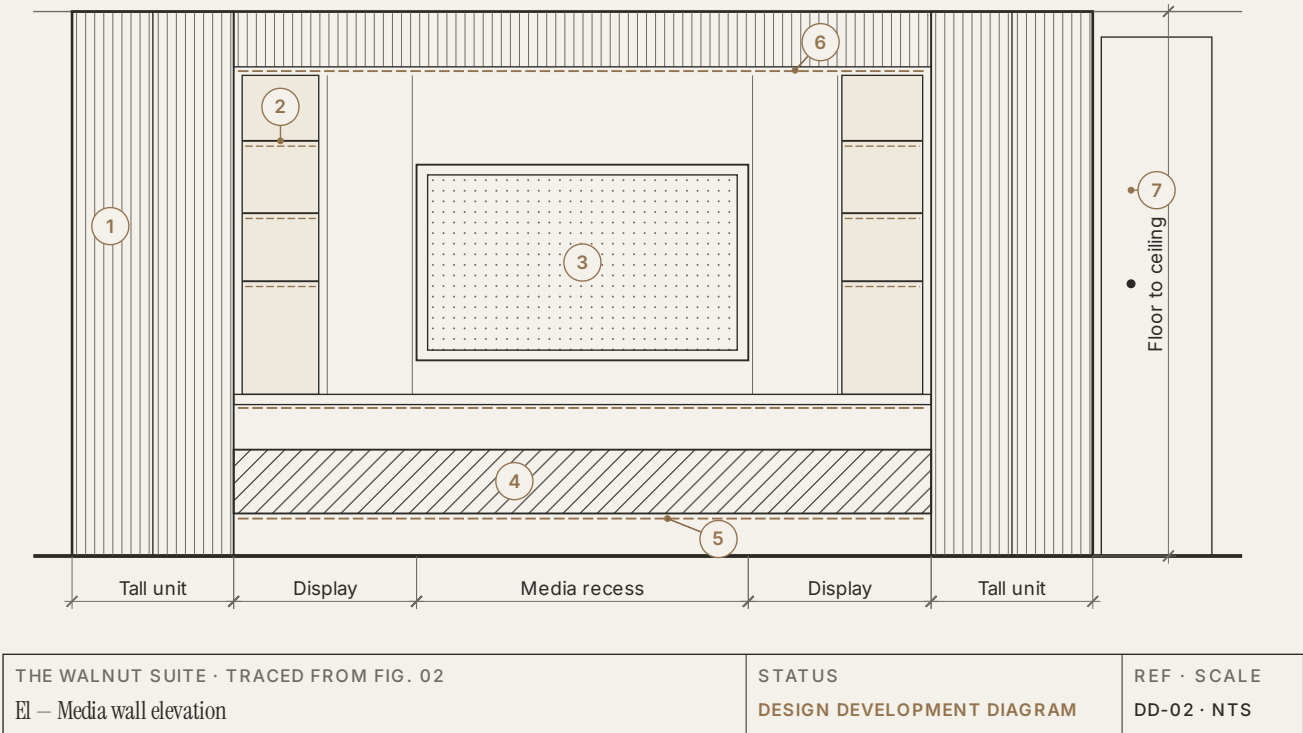

- 1 Tall unit — walnut veneer, flush doors

2 Lit display niche — LED under each shelf

3 Media recess in a framed panel

4 Black marble ledge
- 5 Concealed LED below the ledge

6 Continuous LED line below the top panel

7 Door

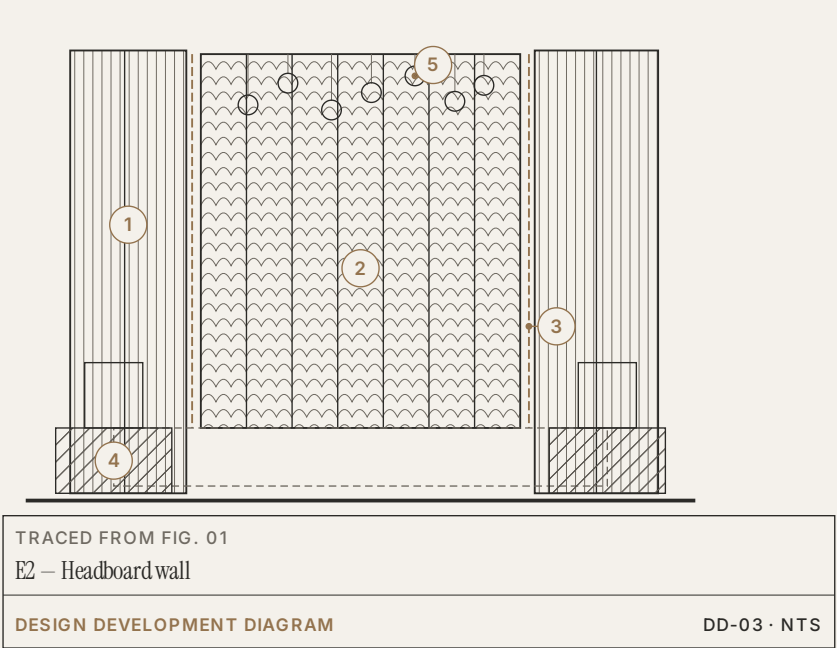


Fig. 01 Headboard wall, as visualised

- 1 Walnut panel

2 Upholstered channels

3 Lit reveal

4 Bedside table, marble

5 Glass pendant cluster

DD-02 and DD-03 are traced from the proportions of the visualisations (Fig. 02 and Fig. 01) to explain the joinery and lighting strategy. They are not construction drawings; dimensions are named, not measured, until a survey is available.



Fig. 03 Detail of the walnut joinery, integrated shelving and concealed linear lighting.

- 1

LED under each shelf
- 2



Walnut veneer, vertical grain
- 3

Lit display niche
- 4

Framed media recess
- 5

Black marble ledge
- 6

Light below the top band

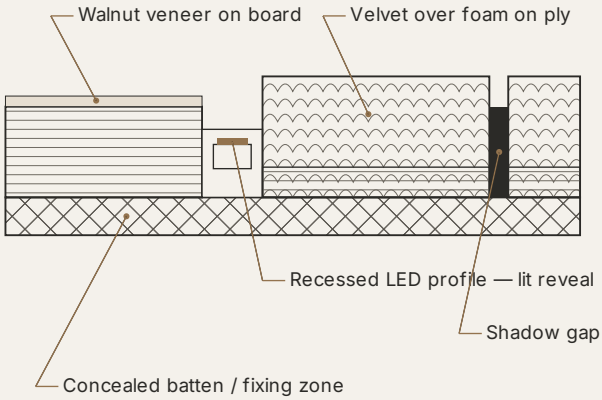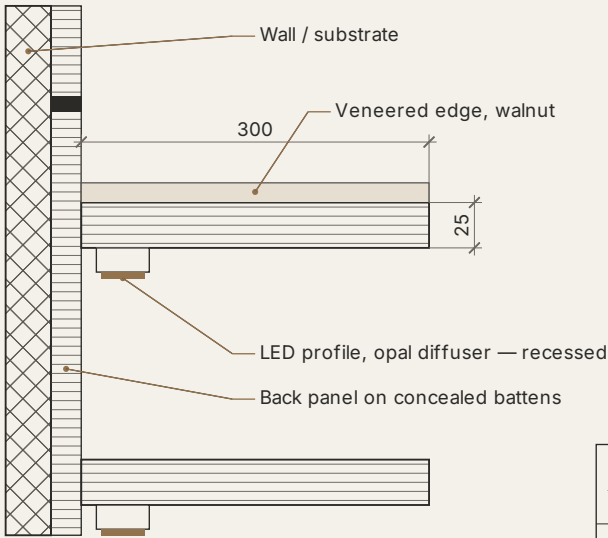

THE WALNUT SUITE · READS FIG. 05

Walnut/light/velvet junction — plan

CONCEPT DETAIL

CD-01 · NTS

ALAA MASRI · INTERIOR ARCHITECTURE

Lit display shelf — section

REPRESENTATIVE DETAIL

RD-01 · 1:5 TYPICAL

Details at typical sizes; project dimensions to be confirmed.

REPRESENTATIVE / CONCEPT DETAILS

RD-01 shows how a lit shelf of this kind is typically built (typical sizes). CD-01 reads the junction visible in Fig. 05. Neither is a construction detail of this project.

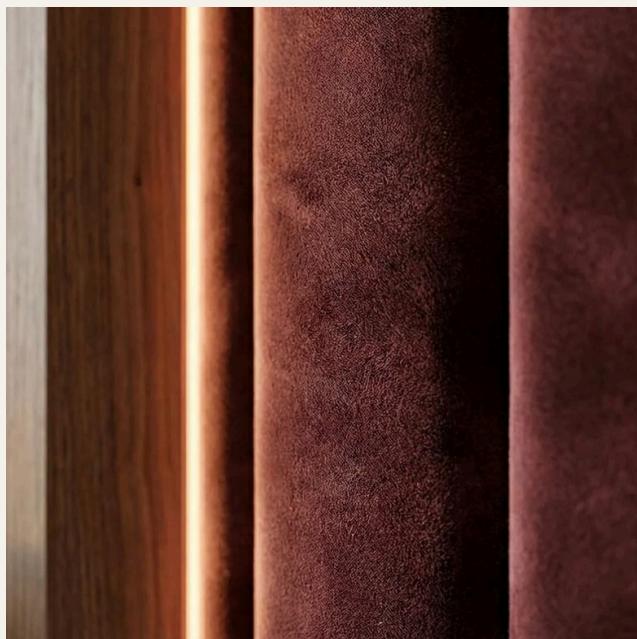


Fig. 05 Burgundy velvet meets walnut and a lit reveal — see CD-01

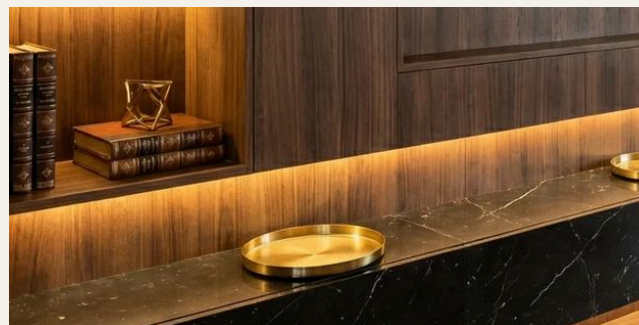


Fig. 03 Lit shelf, ledge and brass, enlarged




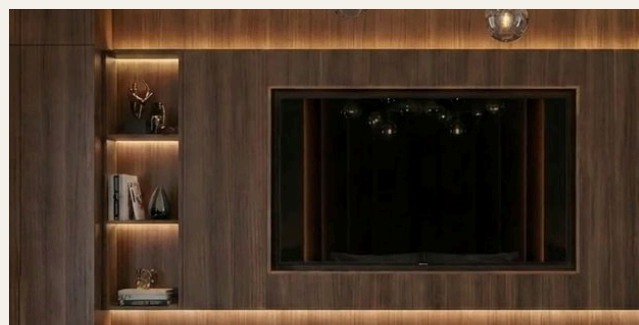


Fig. 02 Niche and media recess, enlarged

MATERIAL STUDY — SCHEDULE FORMAT

CODE	SAMPLE	MATERIAL (AS VISUALISED)	CHARACTER	LOCATION	PRODUCT
WD-01		Walnut veneer	Vertical grain, warm dark tone	Panelling, media wall, joinery	To specify
UP-01		Burgundy velvet	Channel-upholstered panels	Headboard wall	To specify
ST-01		Black marble, white veining	Polished	Ledge, bedside tables	To specify
LT-01		Concealed linear light	Warm white, as visualised	Shelves, reveals, ledge, cove	To specify
MT-01		Brass	Polished accent	Trays, accessories	To specify
TX-01		Beige linen	Soft woven texture	Bedding	To specify

Samples are cropped from the project visualisations; colours below are sampled from the renders as lit. Product and supplier columns stay open until specified.

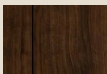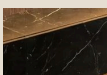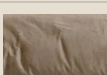

Walnut veneer
#3E2615



Walnut, lit
#4D2A18



Burgundy velvet
#5F302D



Black marble
#28251F



Brass accent
#F7C254



Beige linen
#917F6B



SELECTED WORKS — 04 / 07

Fig. 02 The villa facade at dusk, showing cantilevered volumes, vertical screens and linear lighting.

04 The illuminated villa

CATEGORY

Architecture — Exterior

LOCATION

To confirm

YEAR

To confirm


ROLE

To confirm


SCOPE

To confirm

A contemporary villa study exploring stone, vertical screening and architectural lighting from day to dusk.

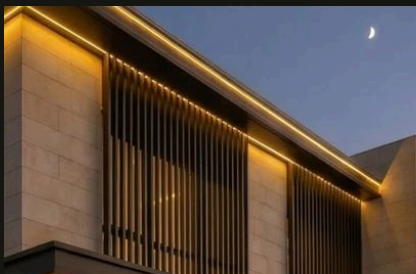

A Linear light under the eaves — Fig. 02

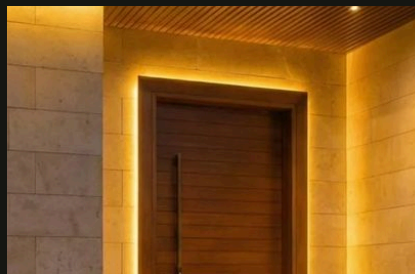

B Lit entrance canopy and door — Fig. 03



C Wall washers and lit planting — Fig. 01

Limestone

#F1D3B1 · Fig. 05

Timber screen

#5C4734 · Fig. 05

Bronze fascia

#705845 · Fig. 05

Warm facade light

#D09A58 · Fig. 04


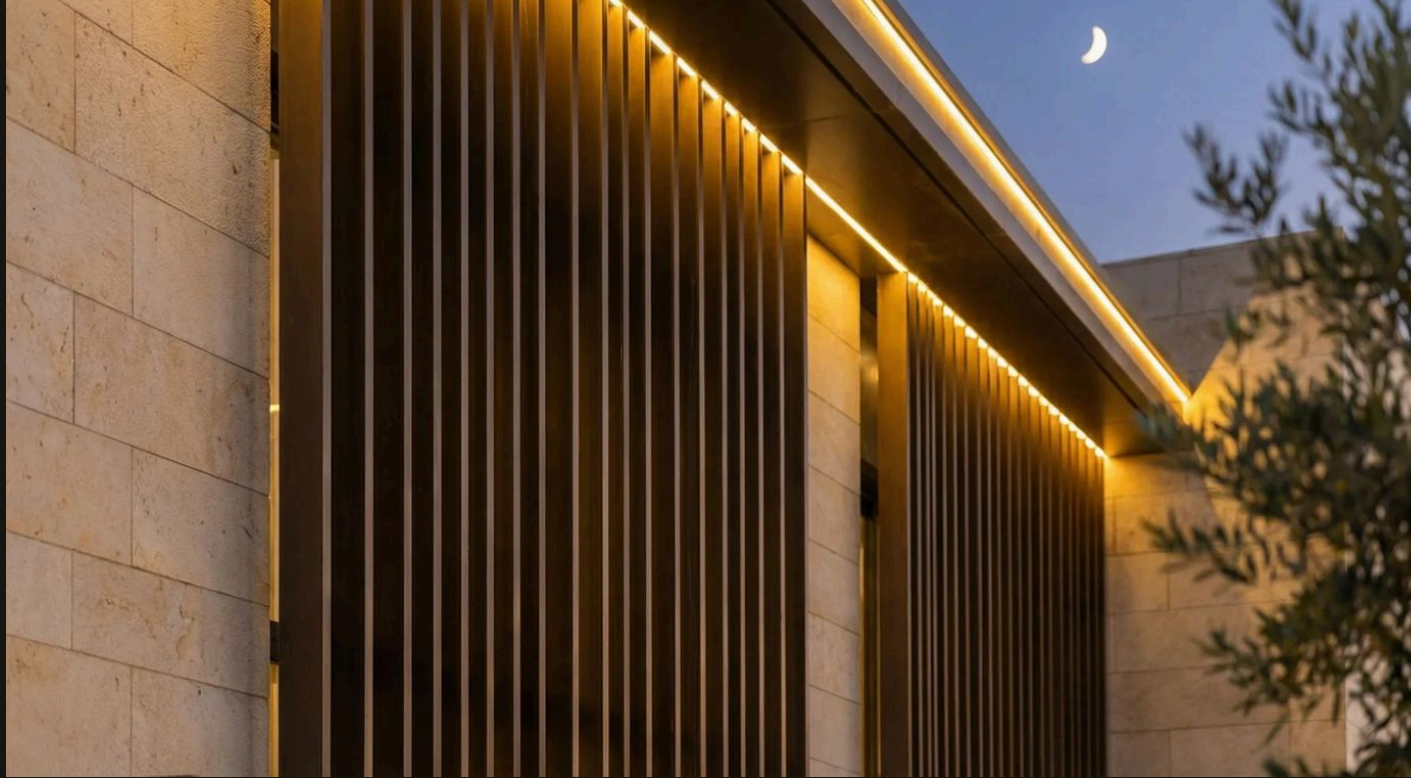


Fig. 04 Detail of vertical timber screening and concealed lighting along the parapet.

FACADE LIGHTING

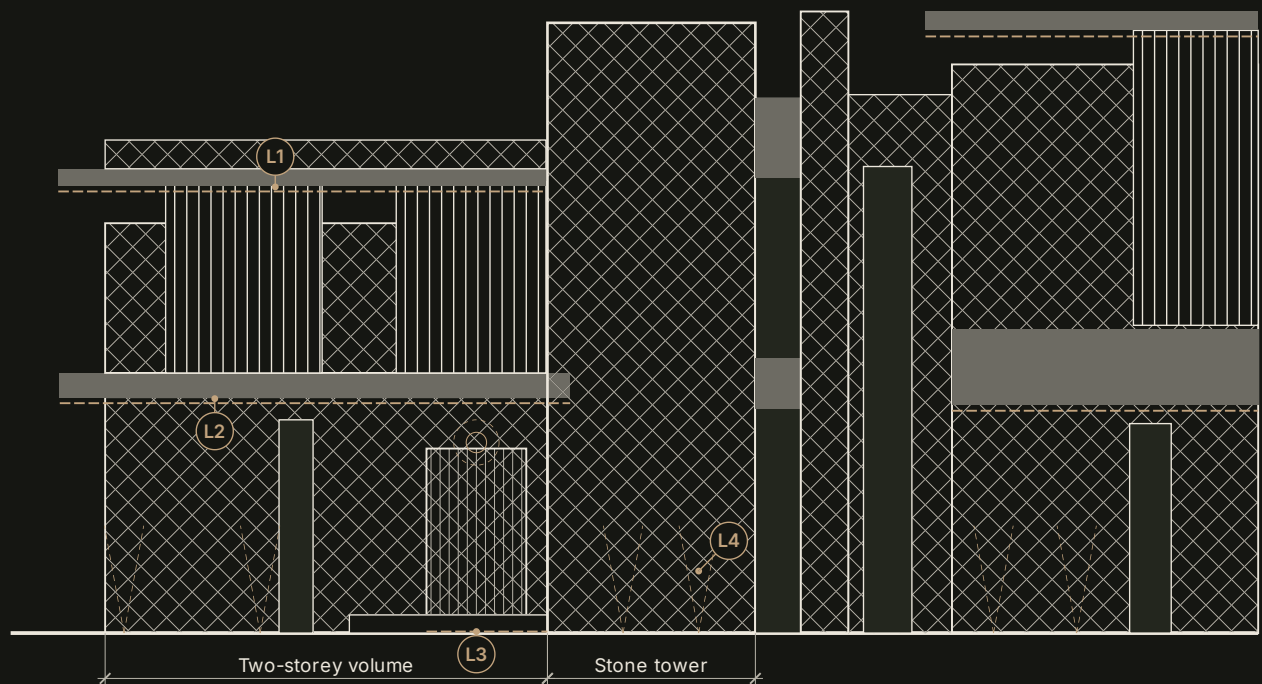

ILLUMINATED VILLA · FIG. 05, LIGHT FROM 02-04
Front elevation – facade lighting strategy

STATUS
DESIGN DEVELOPMENT DIAGRAM

REF · SCALE
DD-V2 · NTS

L1 Linear light under the roof eaves

L2 Linear light under the first-floor canopy


L3 Light line at the entrance step and door

L4 Ground up-lights washing the stone

DD-V2 overlays the lighting visible in the dusk views (Fig. 02-04) on the daylight elevation (Fig. 05). A design development diagram — not a lighting or electrical layout.



Fig. 05 The villa in daylight: stone volumes, timber screens and a recessed entrance.

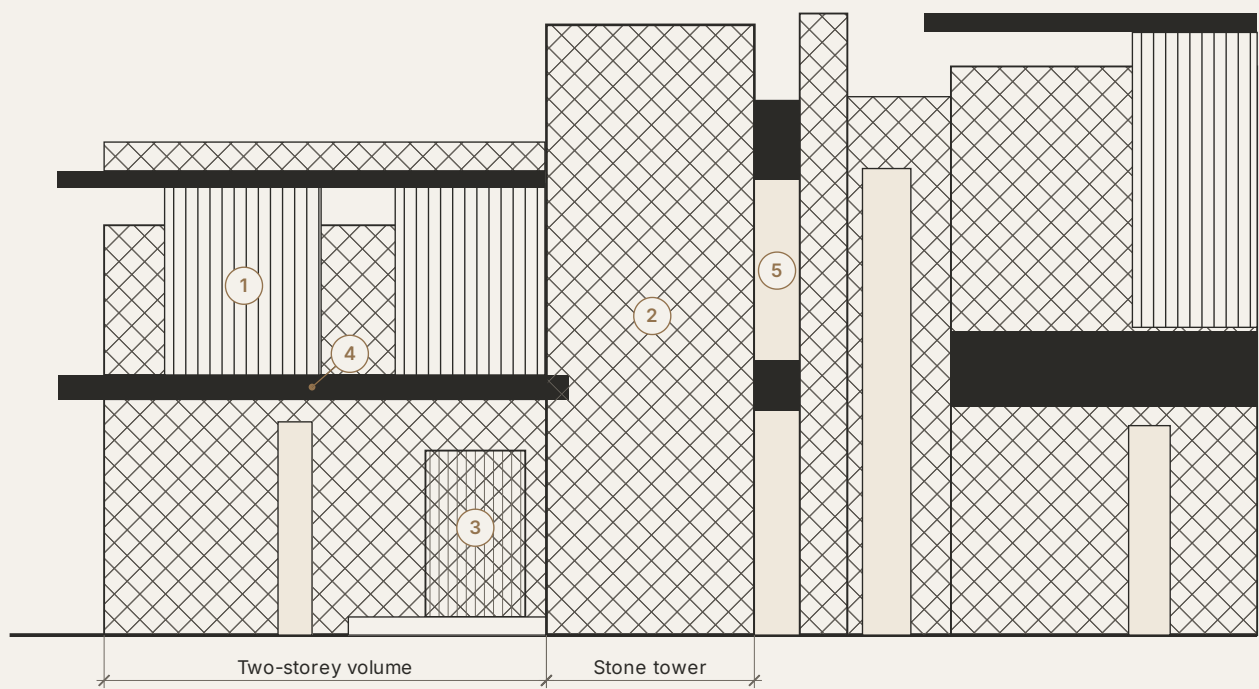

THE ILLUMINATED VILLA · TRACED FROM FIG. 05	STATUS	REF · SCALE
Front elevation — massing and materials	DESIGN DEVELOPMENT DIAGRAM	DD-V1 · NTS


- 1 Vertical timber screens
- 2 Stone tower — full height
- 3 Recessed timber entrance
- 4 Cantilevered canopy slab
- 5 Glazed slot between volumes

DD-V1 is traced from the proportions of Fig. 05 — a design development diagram, not a surveyed elevation.



Fig. 01 Aerial view of a contemporary stone villa with landscaped courtyards and warm facade lighting.

- | | |
|-----------------|------------------|
| 1 Main volume | 4 Carport canopy |
| 2 Stone tower | 5 Roof screen |
| 3 Second volume | 6 Boundary wall |

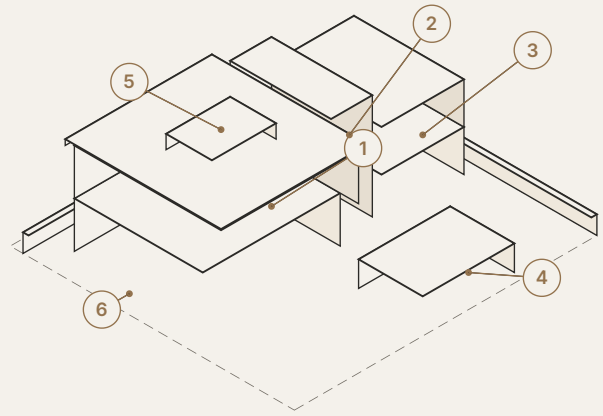


THE ILLUMINATED VILLA · READS FIG. 01
Massing — volumes read from the aerial view

CONCEPTUAL MASSING STUDY

DD-V3 · NTS

SECTION

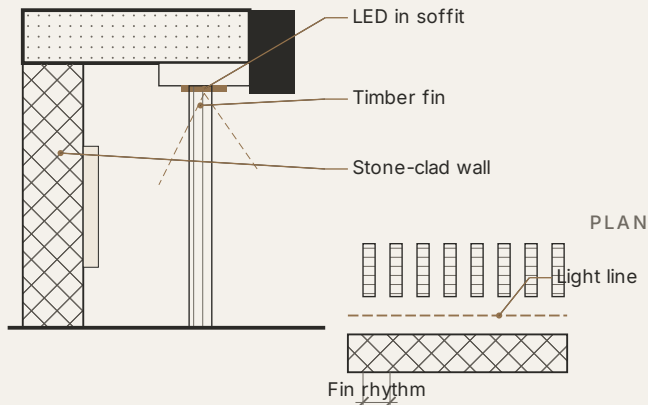

THE ILLUMINATED VILLA · READS FIG. 04

Timber screen and soffit light

CONCEPT DETAIL

CD-V1 · NTS

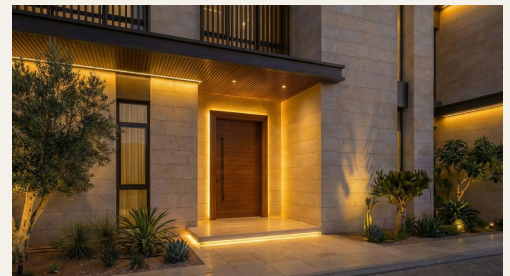



Fig. 03 Entrance canopy with a timber door, stone cladding and lit planting.

DD-V3 reads the volumes of the aerial view; CD-V1 suggests how the screen and soffit light seen in Fig. 04 could be built. Both are conceptual.


MATERIAL STUDY — CROPPED FROM THE VISUALISATIONS



Limestone
Fig. 05

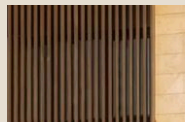


Timber screen
Fig. 05

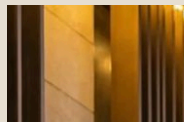

Stone at dusk
Fig. 04



Fins, lit
Fig. 04

 

Limestone cladding
#F1D3B1 · Fig. 05



Timber screen
#5C4734 · Fig. 05

ST-01 Limestone cladding, coursed

WD-01 Vertical timber screens and door

MT-01 Dark bronze fascias and canopies


LT-01 Linear facade light, warm white



SELECTED WORKS — 05 / 07

Fig. 01 Open-plan living and dining space with a linear fireplace, timber wall and garden views.

05 Living by *the garden*

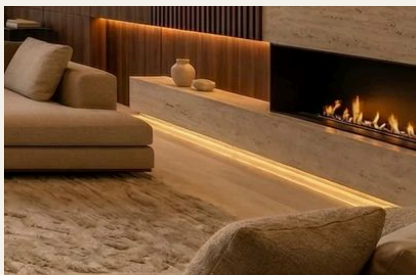

A Linear fireplace in stone — Fig. 01



B Clerestory and garden light — Fig. 02



C Boucle lounge chair — Fig. 05

CATEGORY

Residential — Living

LOCATION

To confirm

YEAR

To confirm

ROLE

To confirm

SCOPE

To confirm

CONCEPT

A warm family living and dining space with garden views, textured fabrics and a linear fireplace.



Walnut slats
#5F412B · Fig. 03




Travertine
#AA8966 · Fig. 03



Boucle
#D6B493 · Fig. 05




Sofa fabric
#AF8D72 · Fig. 01

 

Charcoal weave
#382B1E · Fig. 02

One open room — *cook, gather, look out.*

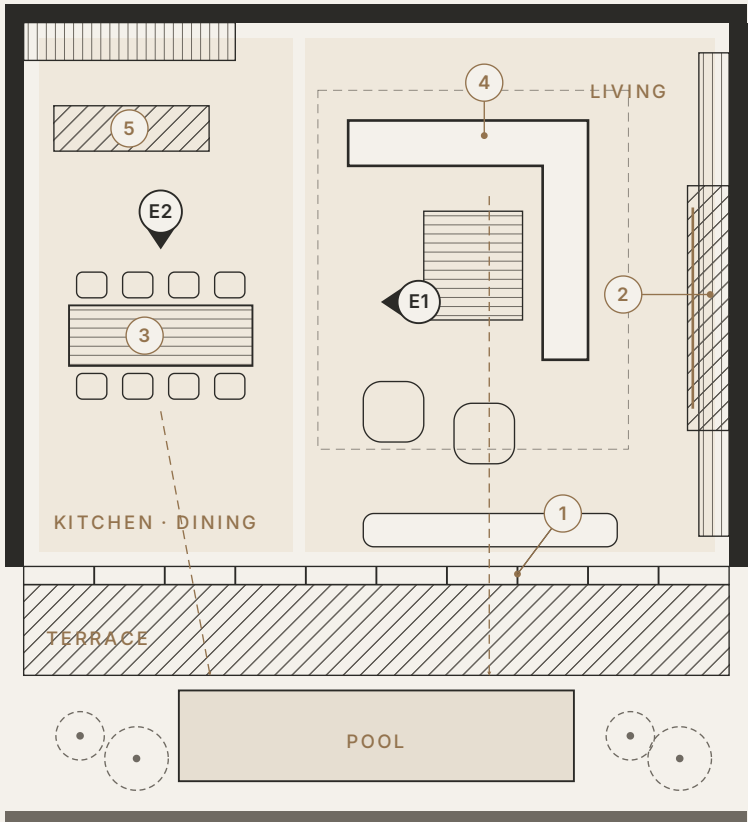

DD-G1 · KEY

- 1 Full-height sliding glazing to the terrace
- 2 Fireplace wall — travertine and walnut slats
- 3 Timber dining table
- 4 L-shaped sofa and coffee tables
- 5 Kitchen island



E1 to the garden — Fig. 01



E2 from the dining table — Fig. 02

READS FIG. 01 + 02 · NOT A SURVEYED PLAN	
Living by the garden — layout reading	
CONCEPTUAL SPACE STUDY	DD-G1 · NTS

FURNITURE ZONING — AS VISUALISED



KITCHEN
Stone-topped island, dark timber joinery



DINING
Long timber table, woven dining chairs, garden view



LIVING
Deep sofa, textured lounge chairs, layered rug



TERRACE
Pool, palms and desert planting beyond the glass

CONCEPTUAL SPACE STUDY	
DD-G1 reads Fig. 01 and 02 to show zoning, views and the indoor–outdoor link. Not a surveyed plan.	

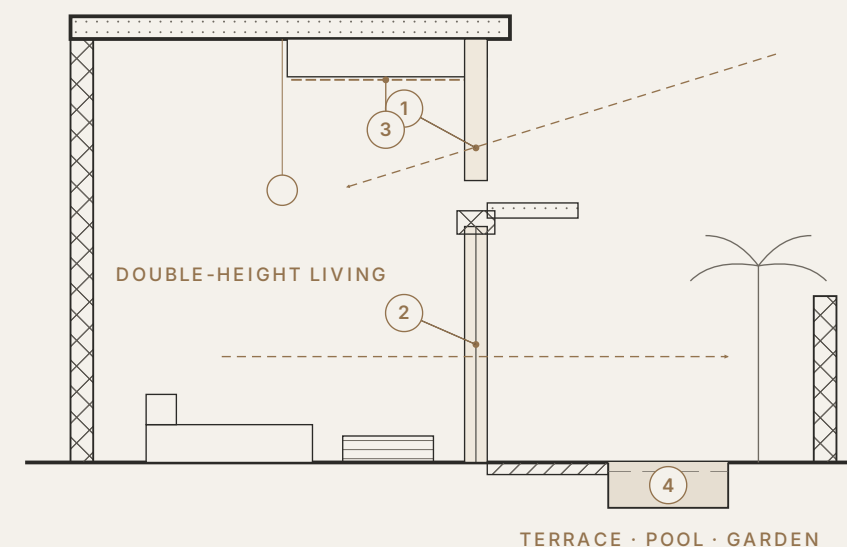


Fig. 02 Timber dining table beneath a skylight, with palm-lined garden views at sunset.

The garden as the fourth wall.

- 1 Clerestory glazing above the doors
- 2 Full-height sliding doors
- 3 Cove light at the bulkhead
- 4 Pool on the terrace

DD-G3 is a conceptual section read from Fig. 01 and Fig. 02. Heights and depths are not measured.



LIVING BY THE GARDEN · READS FIG. 01 + 02	
Indoor / outdoor section	
CONCEPTUAL SECTION STUDY	DD-G3 · NTS

LOOKING OUT — ENLARGED FROM THE VISUALISATIONS




1 Clerestory — Fig. 01



4 Pool and palms — Fig. 01



2 Sliding doors — Fig. 02

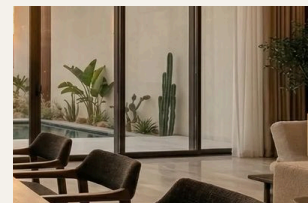

— Desert planting — Fig. 02

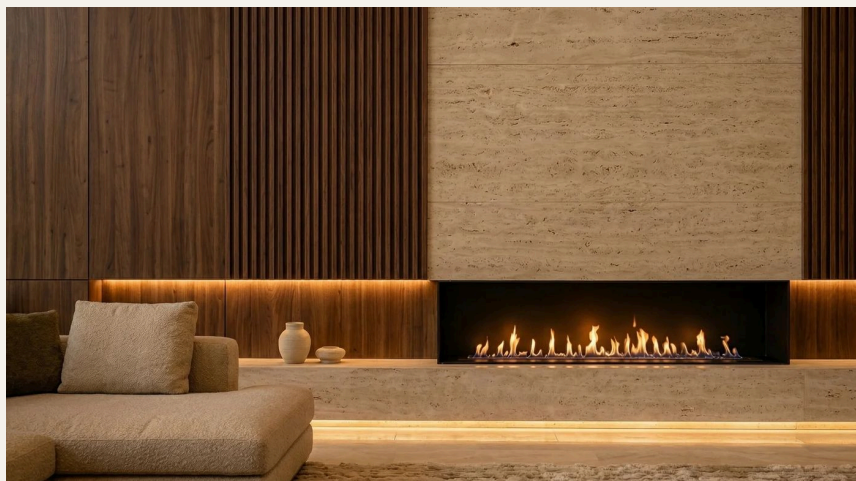


Fig. 03 Linear fireplace set into a textured stone wall with timber slats.

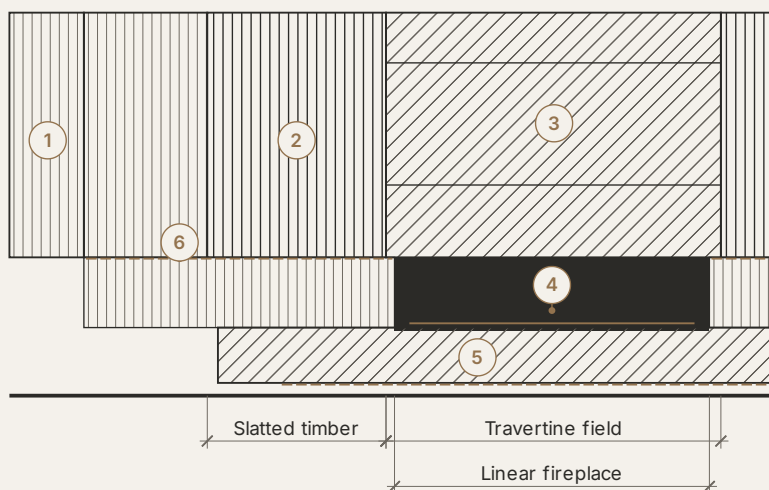


Fig. 05 Boucle lounge chair and cushion in the corner of the living room.

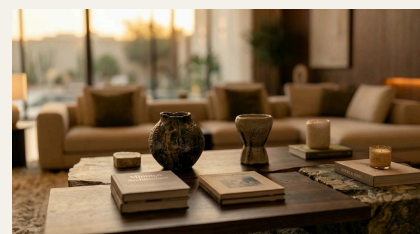


Fig. 04 Coffee table with ceramics, books and layered textiles.

DD-G2 · KEY

- 1 Flat walnut panels
- 2 Walnut slats
- 3 Travertine field
- 4 Linear fireplace
- 5 Travertine plinth
- 6 LED lines above and below


DD-G2 traced from the frontal view in Fig. 03; not a construction drawing.

LIVING BY THE GARDEN · TRACED FROM FIG. 03
Fireplace wall — elevation


DESIGN DEVELOPMENT DIAGRAM

DD-G2 · NTS

MATERIAL STUDY — SWATCHES CROPPED FROM THE VISUALISATIONS

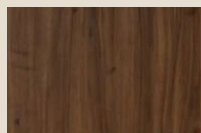


Walnut
Fig. 03

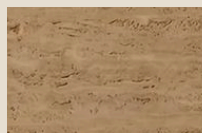


Travertine
Fig. 03



Boucle
Fig. 05

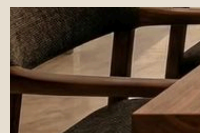

Charcoal weave
Fig. 02

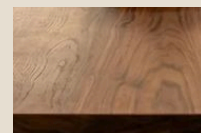

Timber table
Fig. 02



Walnut slats
#5F412B



Travertine
#AA8966



Boucle upholstery
#D6B493



Charcoal chair
weave
#382B1E



Sofa fabric
#AF8D72



SELECTED WORKS — 06 / 07

Fig. 01 Double-height salon with a curved burgundy sofa, full-height glazing and a burgundy feature wall.

06 The burgundy *salon*

CATEGORY

Residential — Living

LOCATION

To confirm

YEAR

To confirm

ROLE

To confirm


SCOPE

To confirm


A double-height salon defined by burgundy seating, tall windows and fine architectural detailing.



A Pleated velvet and lit reveals — Fig. 01

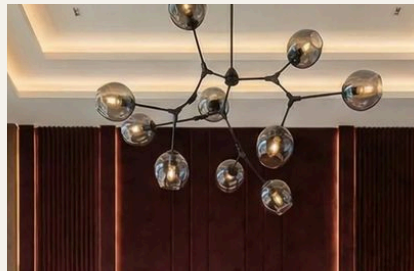

B Sculptural pendant — Fig. 02

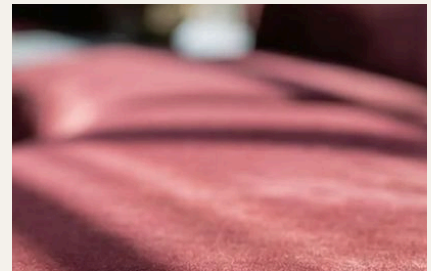

C Velvet in afternoon light — Fig. 03



Burgundy velvet
#3E1C1C · Fig. 01




Walnut panel
#64432B · Fig. 01



Pale timber floor
#A69E93 · Fig. 01



Gallery wall
#9F9E98 · Fig. 01

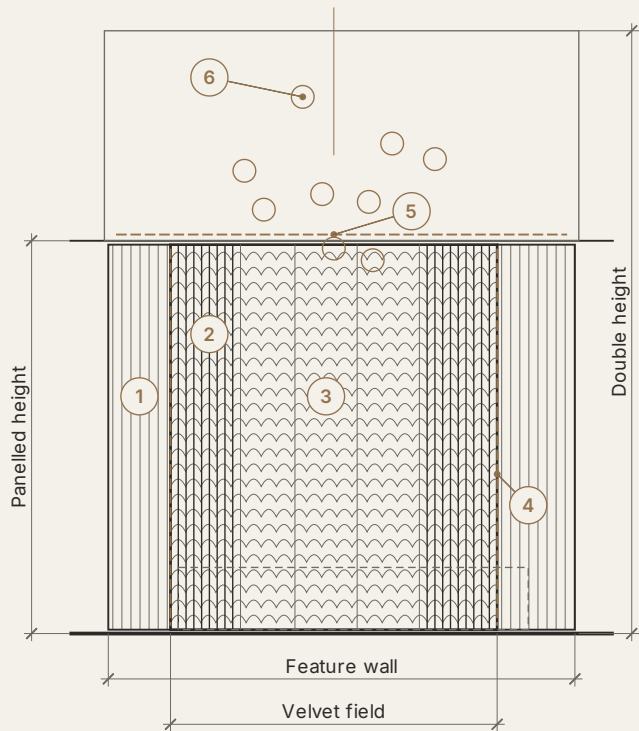

THE BURGUNDY SALON · TRACED FROM FIG. 01
Feature wall — elevation

DESIGN DEVELOPMENT DIAGRAM DD-B1 · NTS

- | | |
|---------------------|-----------------|
| 1 Walnut flank | 4 Lit reveals |
| 2 Pleated velvet | 5 Ceiling cove |
| 3 Flat velvet field | 6 Glass pendant |

DESIGN DEVELOPMENT DIAGRAM
DD-B1 is traced from the proportions of Fig. 01 to explain the feature wall. Heights are named, not measured.

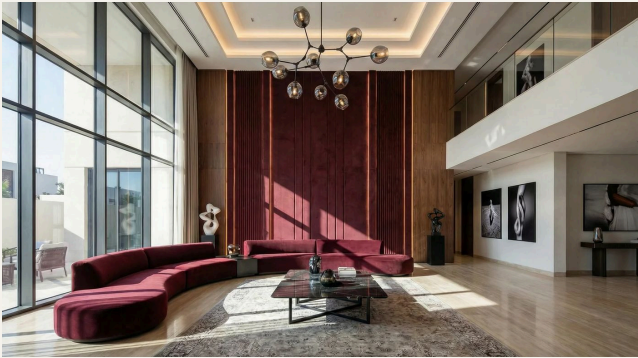


Fig. 02 The salon from a lower angle, showing the sculptural pendant, burgundy wall panel and gallery level above.



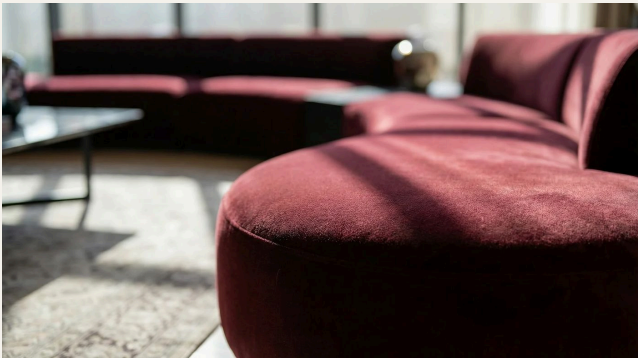


Fig. 03 Close view of the burgundy velvet seating in afternoon light.


MATERIAL STUDY · LIGHT ACCENTS

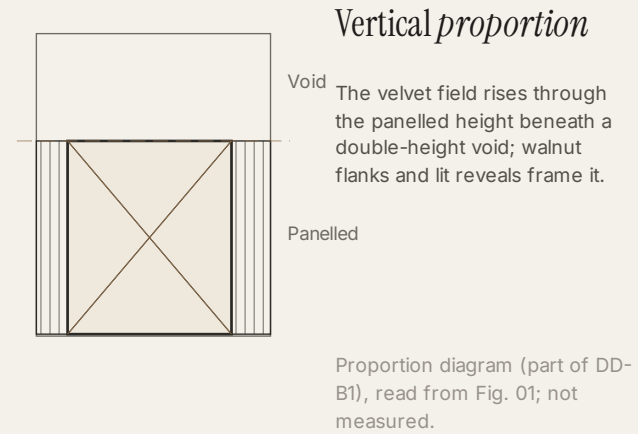

Velvet
Fig. 03

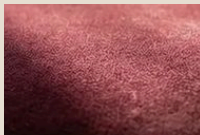

Rug
Fig. 01

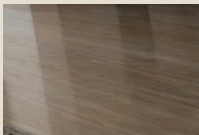

Timber floor
Fig. 01

COVE

Continuous light in the stepped ceiling

REVEALS

Light lines between velvet and walnut

PENDANT

Sculptural glass pendant in the double-height void



SELECTED WORKS — 07 / 07

Fig. 01 Majlis with low perimeter seating, a patterned frieze and a softly lit plaster feature wall.

07 An earthy welcome

CATEGORY

Residential — Majlis

LOCATION

To confirm

YEAR

To confirm

ROLE

To confirm

SCOPE

To confirm

Soft neutral seating, warm timber and patterned walls create a generous space for gathering.

THE FIRST VIEW — COMPOSITION, AS VISUALISED

1 Lit plaster feature wall on the axis

3 Patterned frieze band

5 Cove light in the ceiling tray

2 Light oak wall cladding

4 Low perimeter seating on a plinth

6 Full-height sheers

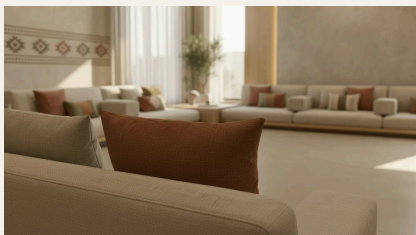


Fig. 02 Terracotta cushions and frieze

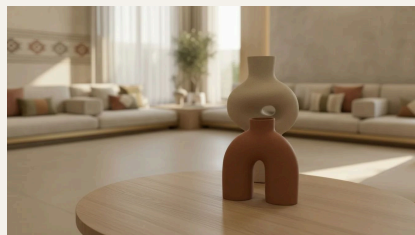


Fig. 04 Ceramic on the low table


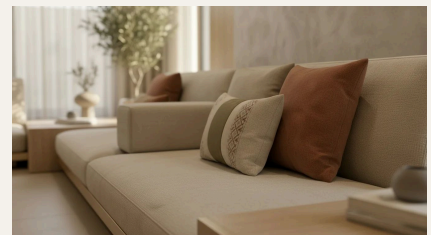


Fig. 05 Seating and woven cushions

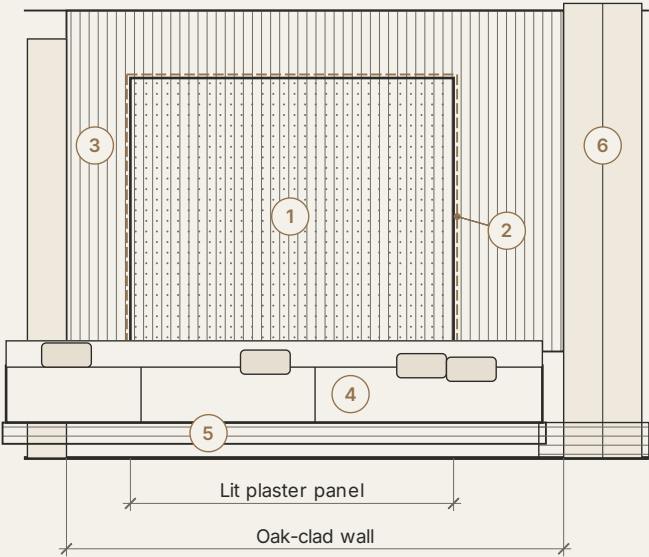

DD-M1 · KEY

- 1 Textured plaster panel
- 2 Concealed light around the panel
- 3 Light oak cladding
- 4 Low seating with cushions
- 5 Oak plinth
- 6 Full-height window, sheers

Traced from the proportions of Fig. 01 — a design development diagram.

AN EARTHY WELCOME · TRACED FROM FIG. 01	
Majlis — feature wall elevation	
DESIGN DEVELOPMENT DIAGRAM	DD-M1 · NTS

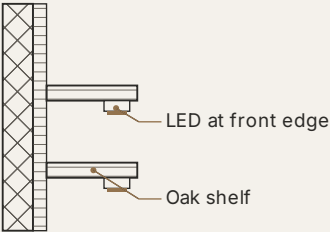


Fig. 03 Lit timber shelving with sculptural ceramic vessels beside the patterned frieze.

ELEVATION



SECTION



AN EARTHY WELCOME · READS FIG. 03	
Lit oak shelf niche	
CONCEPT DETAIL	CD-M1 · NTS

MATERIAL STUDY — FRIEZE MOTIF TRACED FROM FIG. 01 + 03



Vector trace of the band: stepped diamonds between two borders of small diamonds. Right: the frieze as visualised, Fig. 03.



Textured plaster
#9D8A70 · Fig. 01



Light oak
#AA8F70 · Fig. 01




Terracotta
#7B4E2F · Fig. 03



Linen seating
#AA977D · Fig. 01



Frieze pigment
#87644A · Fig. 03

 


Stone floor
#C2BAB1 · Fig. 01

Drawn to be *built.*

Managing interior projects end to end — concept and design development, technical drawings, material selection, BOQ preparation, pricing, supplier and contractor coordination, and final execution on site.

REPRESENTATIVE EXAMPLES

The drawings, schedules and tables on this spread were prepared for this portfolio to show drawing standards and method. They are not construction documents of a specific project; real project documents will be added when supplied.

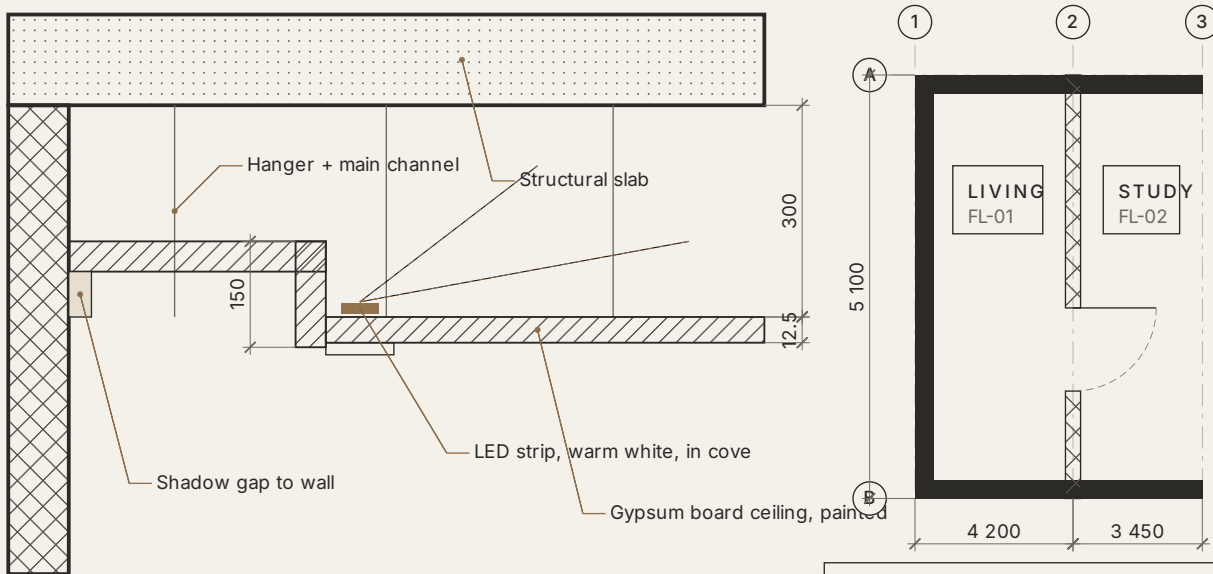

ALAA MASRI · INTERIOR ARCHITECTURE

Lighting cove — ceiling section

REPRESENTATIVE DETAIL

RD-02 · 1:10 TYPICAL

ALAA MASRI · INTERIOR ARCHITECTURE

Plan fragment — dimensioning

REPRESENTATIVE EXAMPLE

RE-01 · 1:50

DRAWING CONVENTIONS

LINE WEIGHTS

	Cut · 0.5 mm
	Heavy · 0.35 mm
	Medium · 0.25 mm
	Fine · 0.13 mm

HATCHES

	Masonry / wall
	Concrete / gypsum
	Timber / board
	Upholstery
	Stone / marble


SYMBOLS

	Elevation / section
	Grid reference
	Finish / note key

DIMENSIONING

	1 200
	mm, to finished faces
	CH = clear ceiling height
	NTS = not to scale

REF	DRAWING	STATUS	SOURCE
RE-01	Plan fragment — dimensioning	Representative example	This portfolio
RD-02	Lighting cove — ceiling section	Representative detail	This portfolio
RE-02	Wardrobe — shop drawing format	Representative example	This portfolio
P—	Project plans, elevations, shop drawings, BOQ	To be supplied	Project records

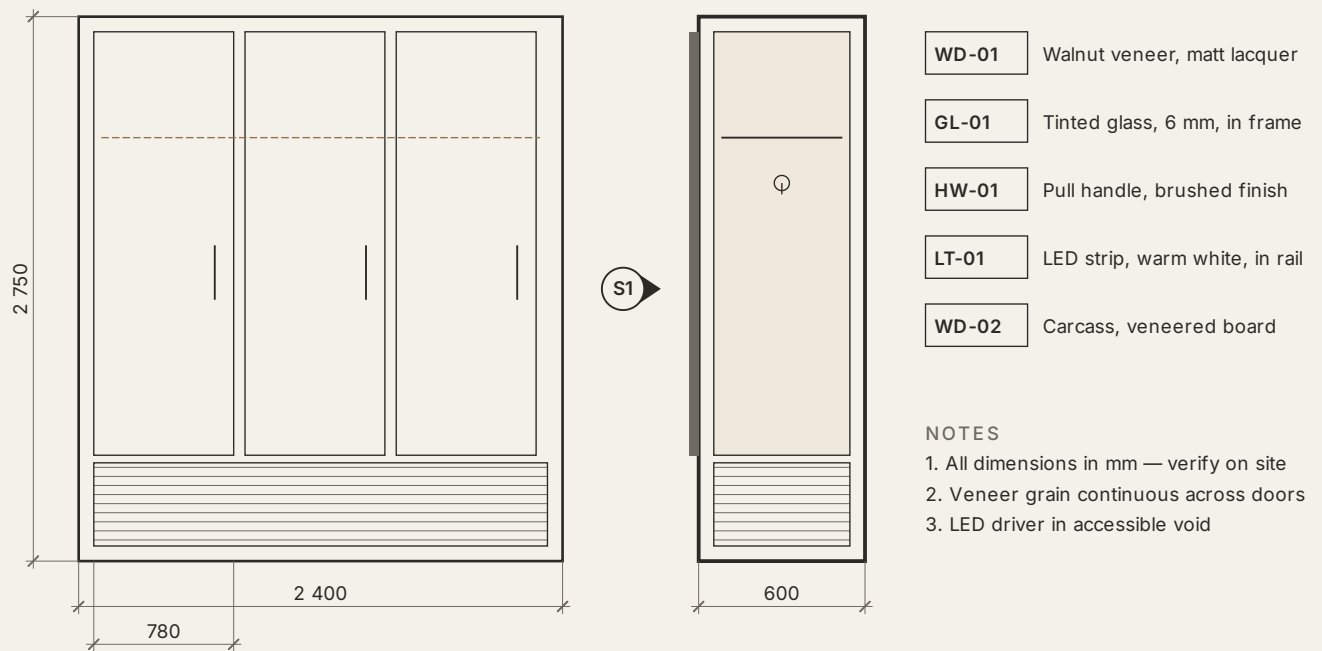

ALAA MASRI · INTERIOR ARCHITECTURE Wardrobe — shop drawing format	STATUS REPRESENTATIVE EXAMPLE	REF · SCALE RE-02 · 1:20 TYPICAL
--	----------------------------------	-------------------------------------

BILL OF QUANTITIES — REPRESENTATIVE FORMAT · SAMPLE VALUES

REF	DESCRIPTION	UNIT	QTY	RATE	AMOUNT
1.01	Suspended gypsum ceiling with lighting cove, painted	m ²	48.0	—	—
1.02	Timber veneer wall panelling on battens	m ²	22.5	—	—
1.03	Built-in wardrobe, veneered, glass doors, LED	m	4.8	—	—
1.04	Stone ledge, polished, with lit recess	m	3.6	—	—
1.05	Upholstered wall panels, fabric-wrapped	m ²	9.2	—	—
1.06	LED strip in aluminium profile, with driver	m	26.0	—	—

Quantities are sample values for format only; rates omitted.

FINISH SCHEDULE — FORMAT

CODE	FINISH
WD-01	Timber veneer, matt lacquer
ST-01	Stone, polished
UP-01	Upholstery fabric, velvet
GL-01	Tinted glass, 6 mm
LT-01	LED linear, warm white

COORDINATION MATRIX — FORMAT

TRADE / PACKAGE	DRAWINGS	SAMPLES	SITE
Carpentry workshop — joinery	●	●	●
Steel fabricator — metalwork	●	●	●
Stone supplier — marble	●	●	●
Glass supplier — doors, partitions	●	●	●
Lighting — coves, profiles	●	○	●

SITE INSPECTION — CHECKLIST FORMAT

☒	Setting-out checked against drawings
☒	Joinery samples approved before production
☒	Stone slabs viewed and matched
☒	Lighting positions checked before closing ceilings
☒	Finishes inspected — snag list issued
☒	Handover documents complete

Representative format — not a record of a specific project.

Professional *experience*

ROLE · RIYADH, SAUDI ARABIA

Senior Interior Designer · Interior Architect · Project Coordinator

Managing and developing interior design projects from concept through execution and final handover.

CAREER RECORD — EMPLOYERS, POSITIONS AND DATES TO BE ADDED

POSITION	EMPLOYER / STUDIO	LOCATION	YEARS
To confirm	To confirm	To confirm	To confirm
To confirm	To confirm	To confirm	To confirm
To confirm	To confirm	To confirm	To confirm

DESIGN

Developing creative, functional interior concepts.

Space planning and furniture layouts.

Mood boards; selecting materials, finishes, colours and furniture.

Designing luxury residential interiors — TV and feature walls, entrances, ceilings, partitions, custom furniture.

TECHNICAL

Technical drawings and shop-drawing coordination for execution.

BOQs, quantity take-offs and cost estimations.

Pricing interior works; quotations with suppliers and subcontractors.

COORDINATION

Coordinating carpentry workshops, steel fabricators, stone and glass suppliers.

Reviewing samples against project specifications.

Coordinating clients, contractors, suppliers, factories and site teams.

EXECUTION

Following up execution; resolving technical and design issues.

Site inspections and quality control.

Managing detail from design approval to final handover.

INTERNATIONAL EXPERIENCE

Saudi Arabia
Qatar
United Arab Emirates
Lebanon

RESIDENTIAL

Luxury villas · apartments · living rooms · majlis & reception · TV feature walls · entrance & foyer · bedrooms · staircase areas · decorative ceilings · custom furniture

COMMERCIAL

Offices · retail spaces · showrooms · commercial interiors · hospitality interiors · custom joinery packages

Let's create *spaces* that last.

SELECTED WORKS — INDEX



01 p. 09



02 p. 15



03 p. 20



04 p. 26



05 p. 30



06 p. 34



07 p. 36

EMAIL

info@alaamasri.com

PHONE

+966 57 053 3358

WHATSAPP

+966 57 053 3358


ONLINE

alaamasri.com



BASED IN

Riyadh, Saudi Arabia

For private clients, developers, contractors, consultants and design studios — project enquiries, collaborations and professional opportunities.

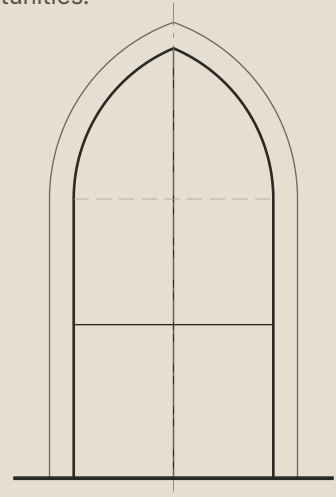

ARCHED OPENING · DESIGN
DEVELOPMENT DIAGRAM

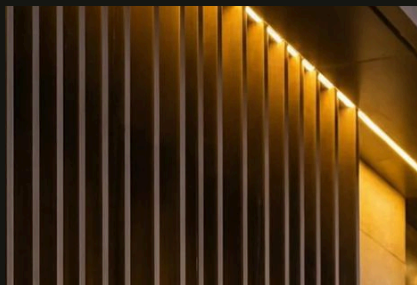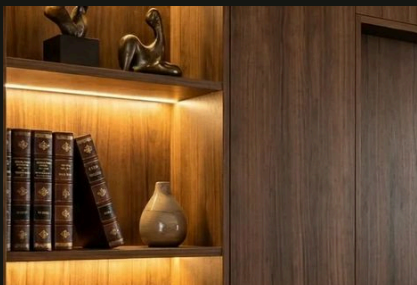

ARCH · JOINERY · FACADE — DETAILS FROM THE SELECTED WORKS


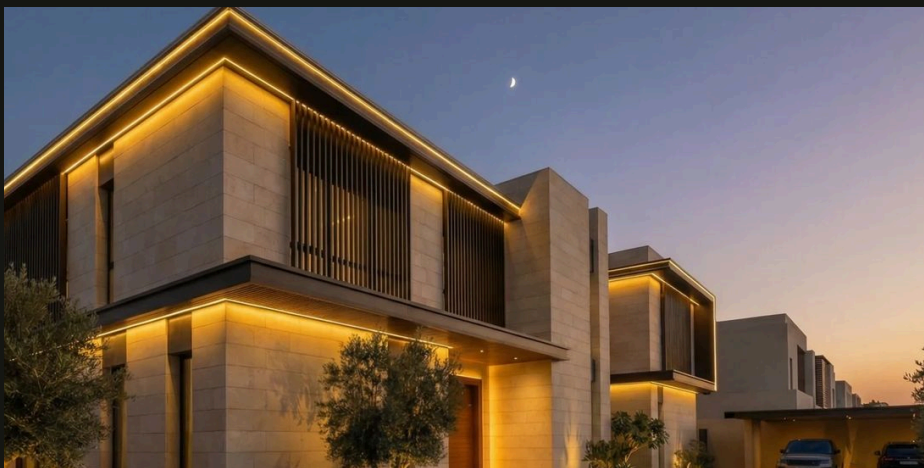


Fig. 02 The illuminated villa at dusk

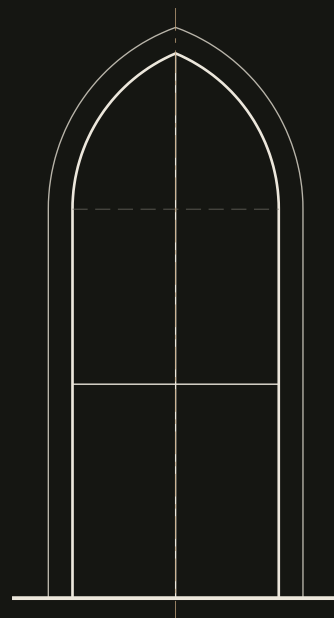

ARCHED OPENING
DESIGN DEVELOPMENT
DIAGRAM

Alaa Masri

INTERIOR DESIGNER · INTERIOR ARCHITECT

PORTFOLIO 2026-2027